


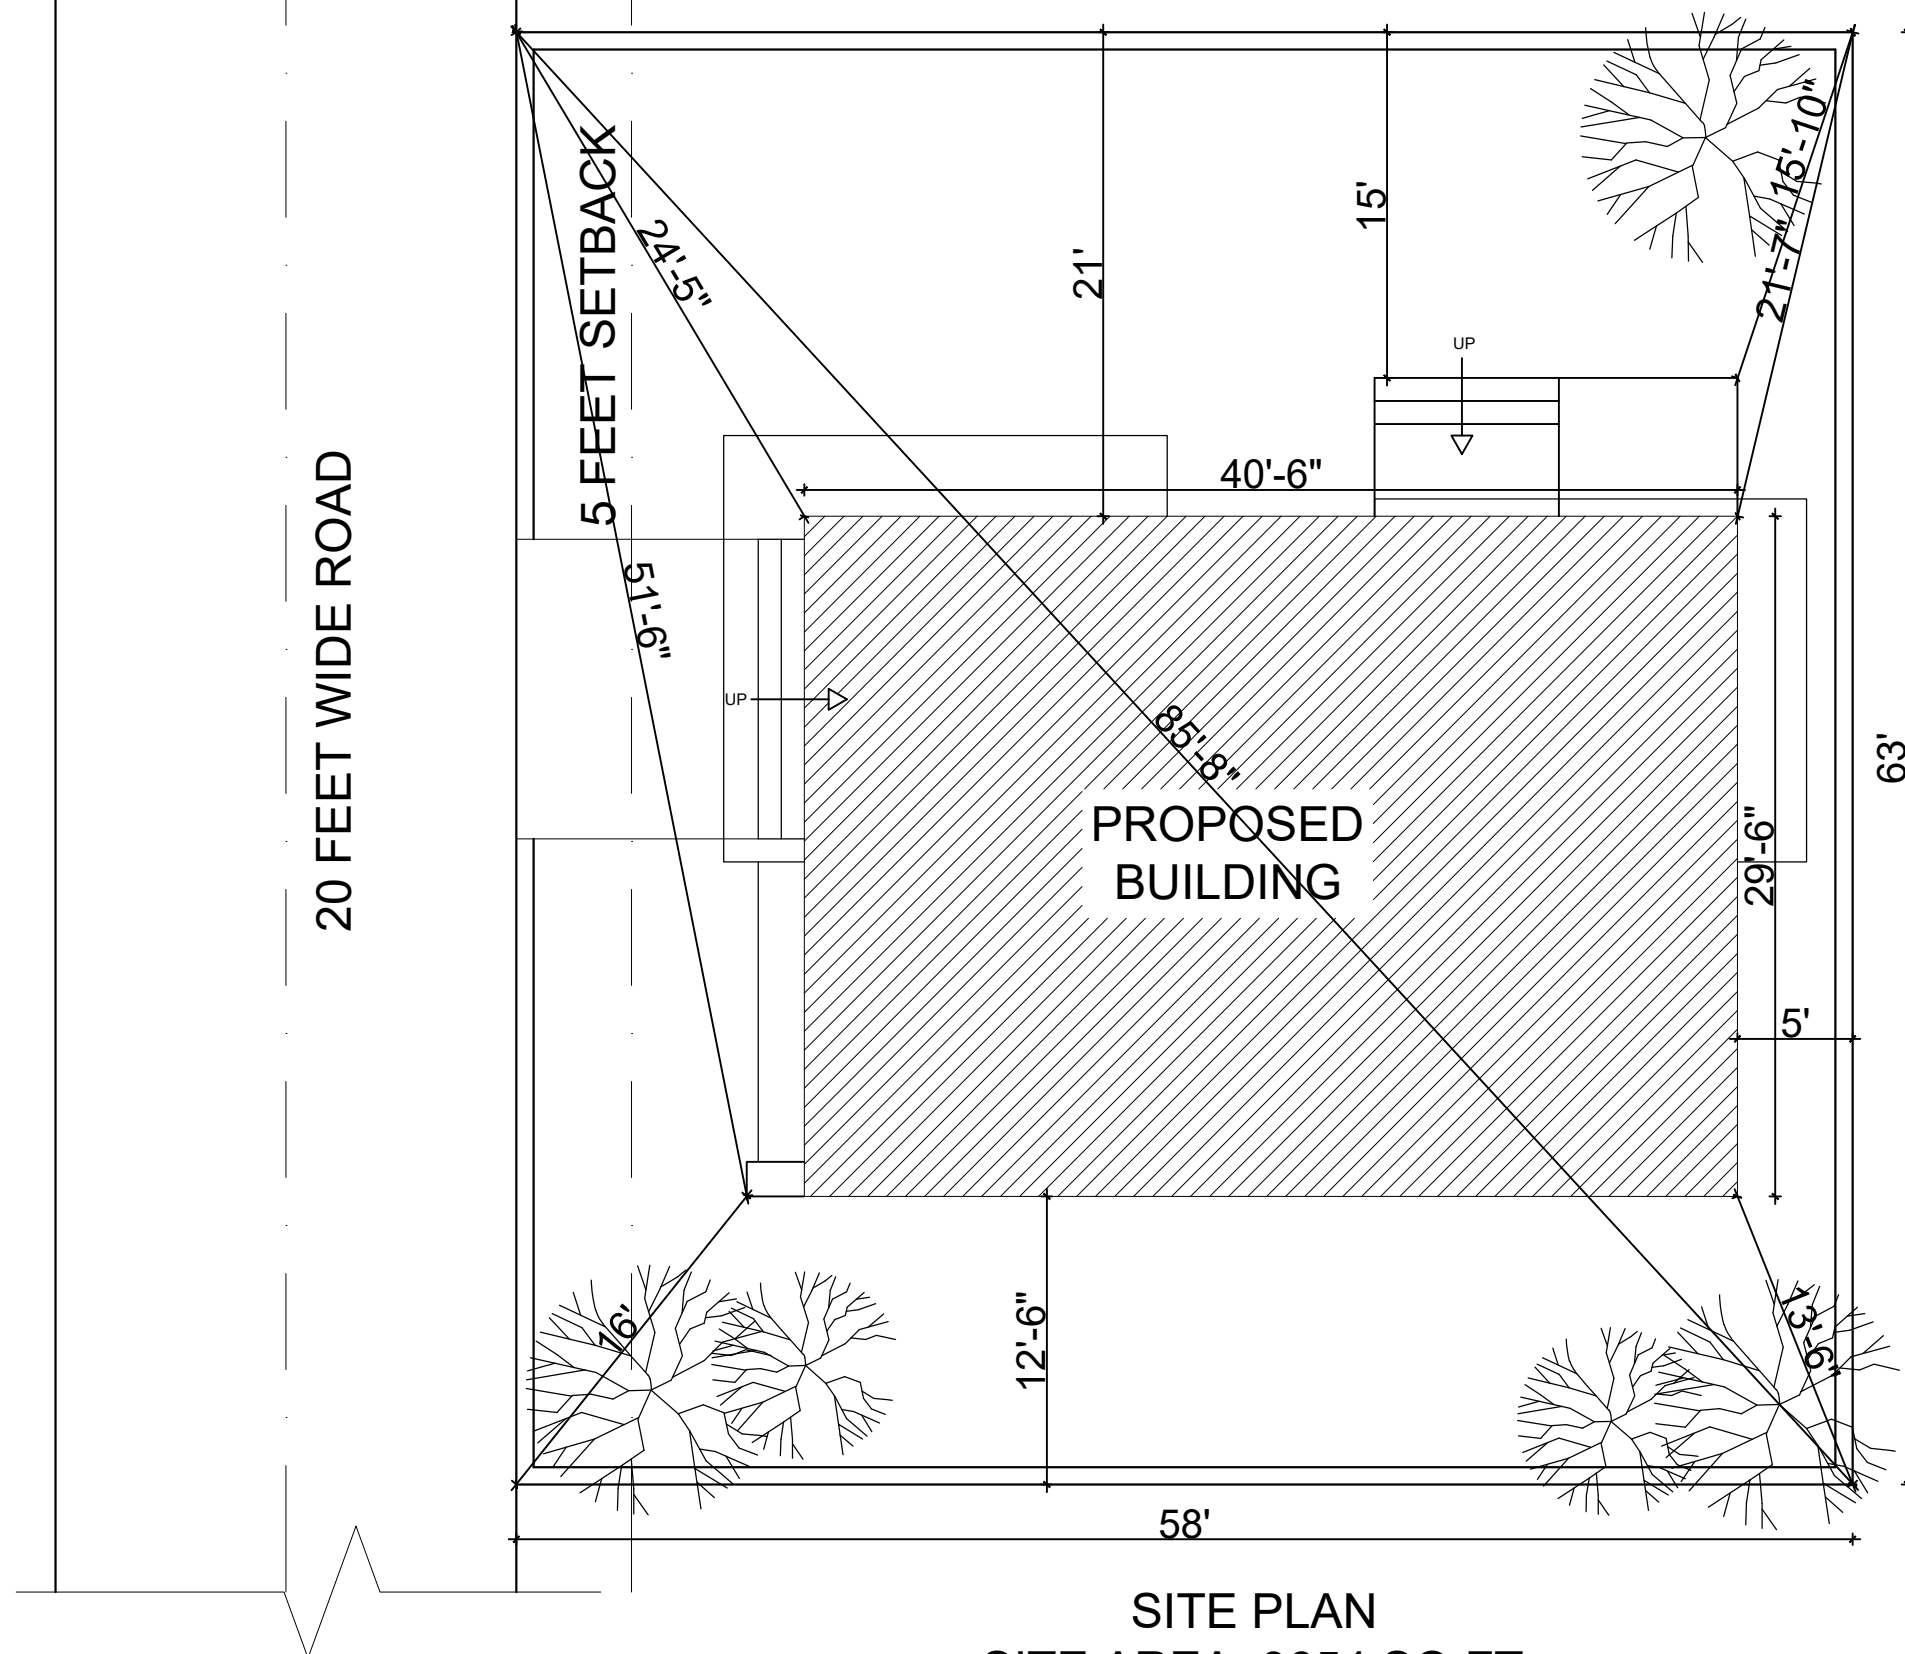

SITE PLAN
 SITE AREA: 3654 SQ.FT
 GCR: 32.69%
 FAR: 1.2
 TOTAL BUILT UP AREA: 2959.37 SQ.FT

URBAN PARK PVT.LTD

KATHMANDU, NEPAL

RESIDENCE DESIGN

ARCHITECTURAL DRAWING

ARCHITECT:

AR.APIL KC

DRAWN BY:

AR.SAMJHANA MAHARJAN

DATE :

March, 2021


SCALE :

1:100

SHEET NO.

AR

00

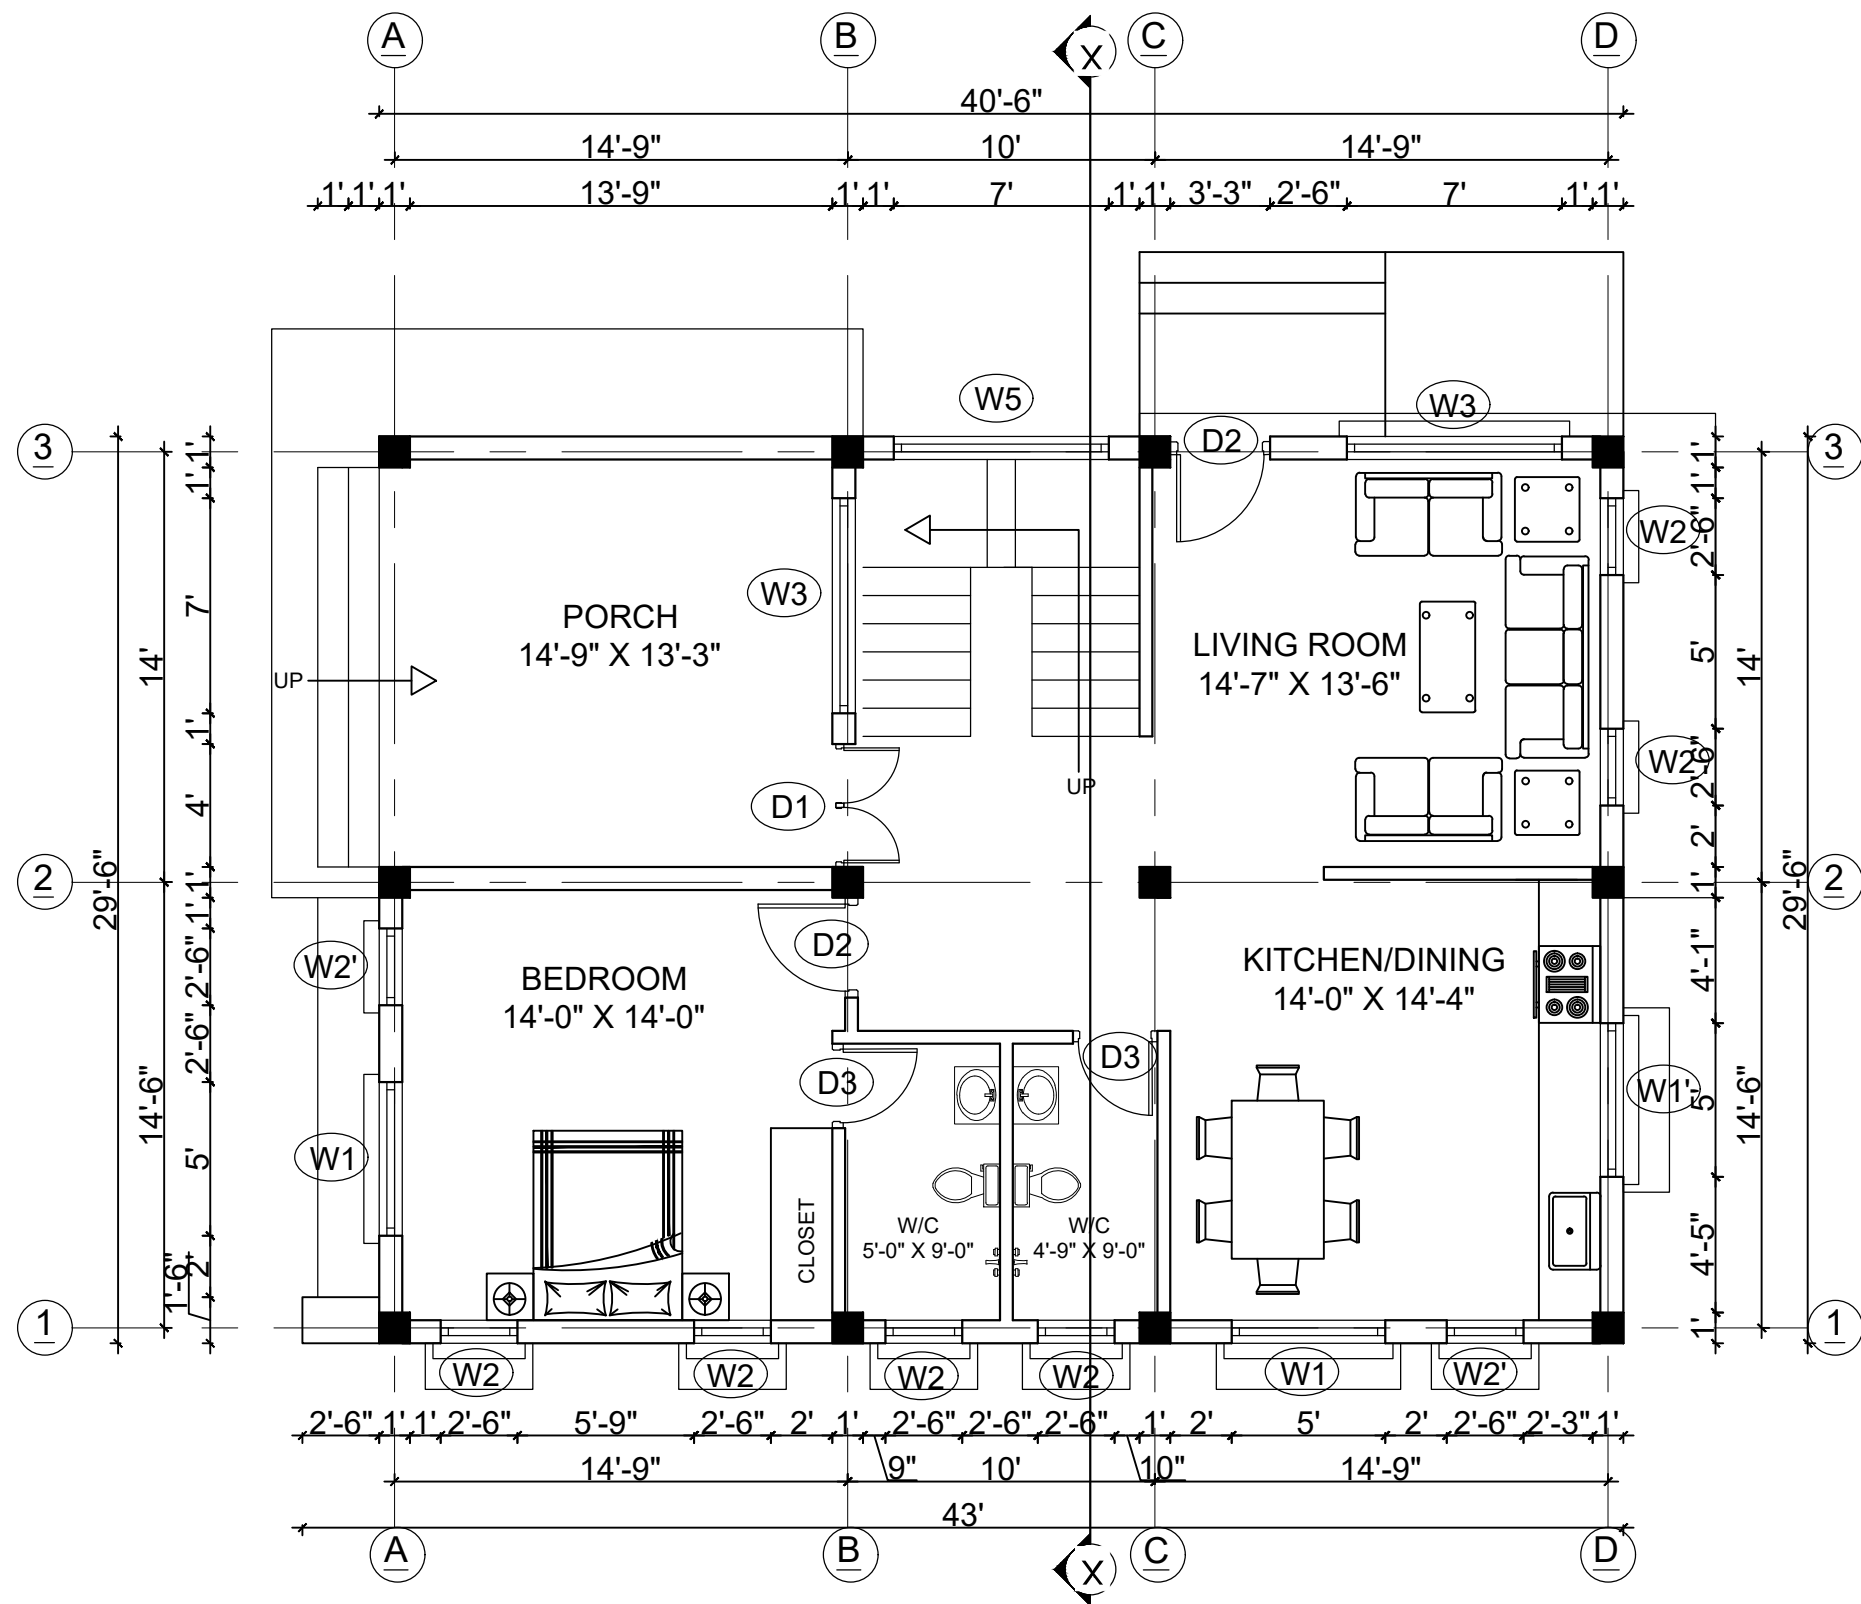

GROUND FLOOR PLAN
FLOOR AREA: 1194.75 SQ.FT

URBAN PARK PVT.LTD

KATHMANDU, NEPAL

RESIDENCE DESIGN

ARCHITECTURAL DRAWING

ARCHITECT:

AR.APIL KC

DRAWN BY:

AR.SAMJHANA MAHARJAN

DATE :

March, 2021


SCALE :

1:75

SHEET NO.

AR

01

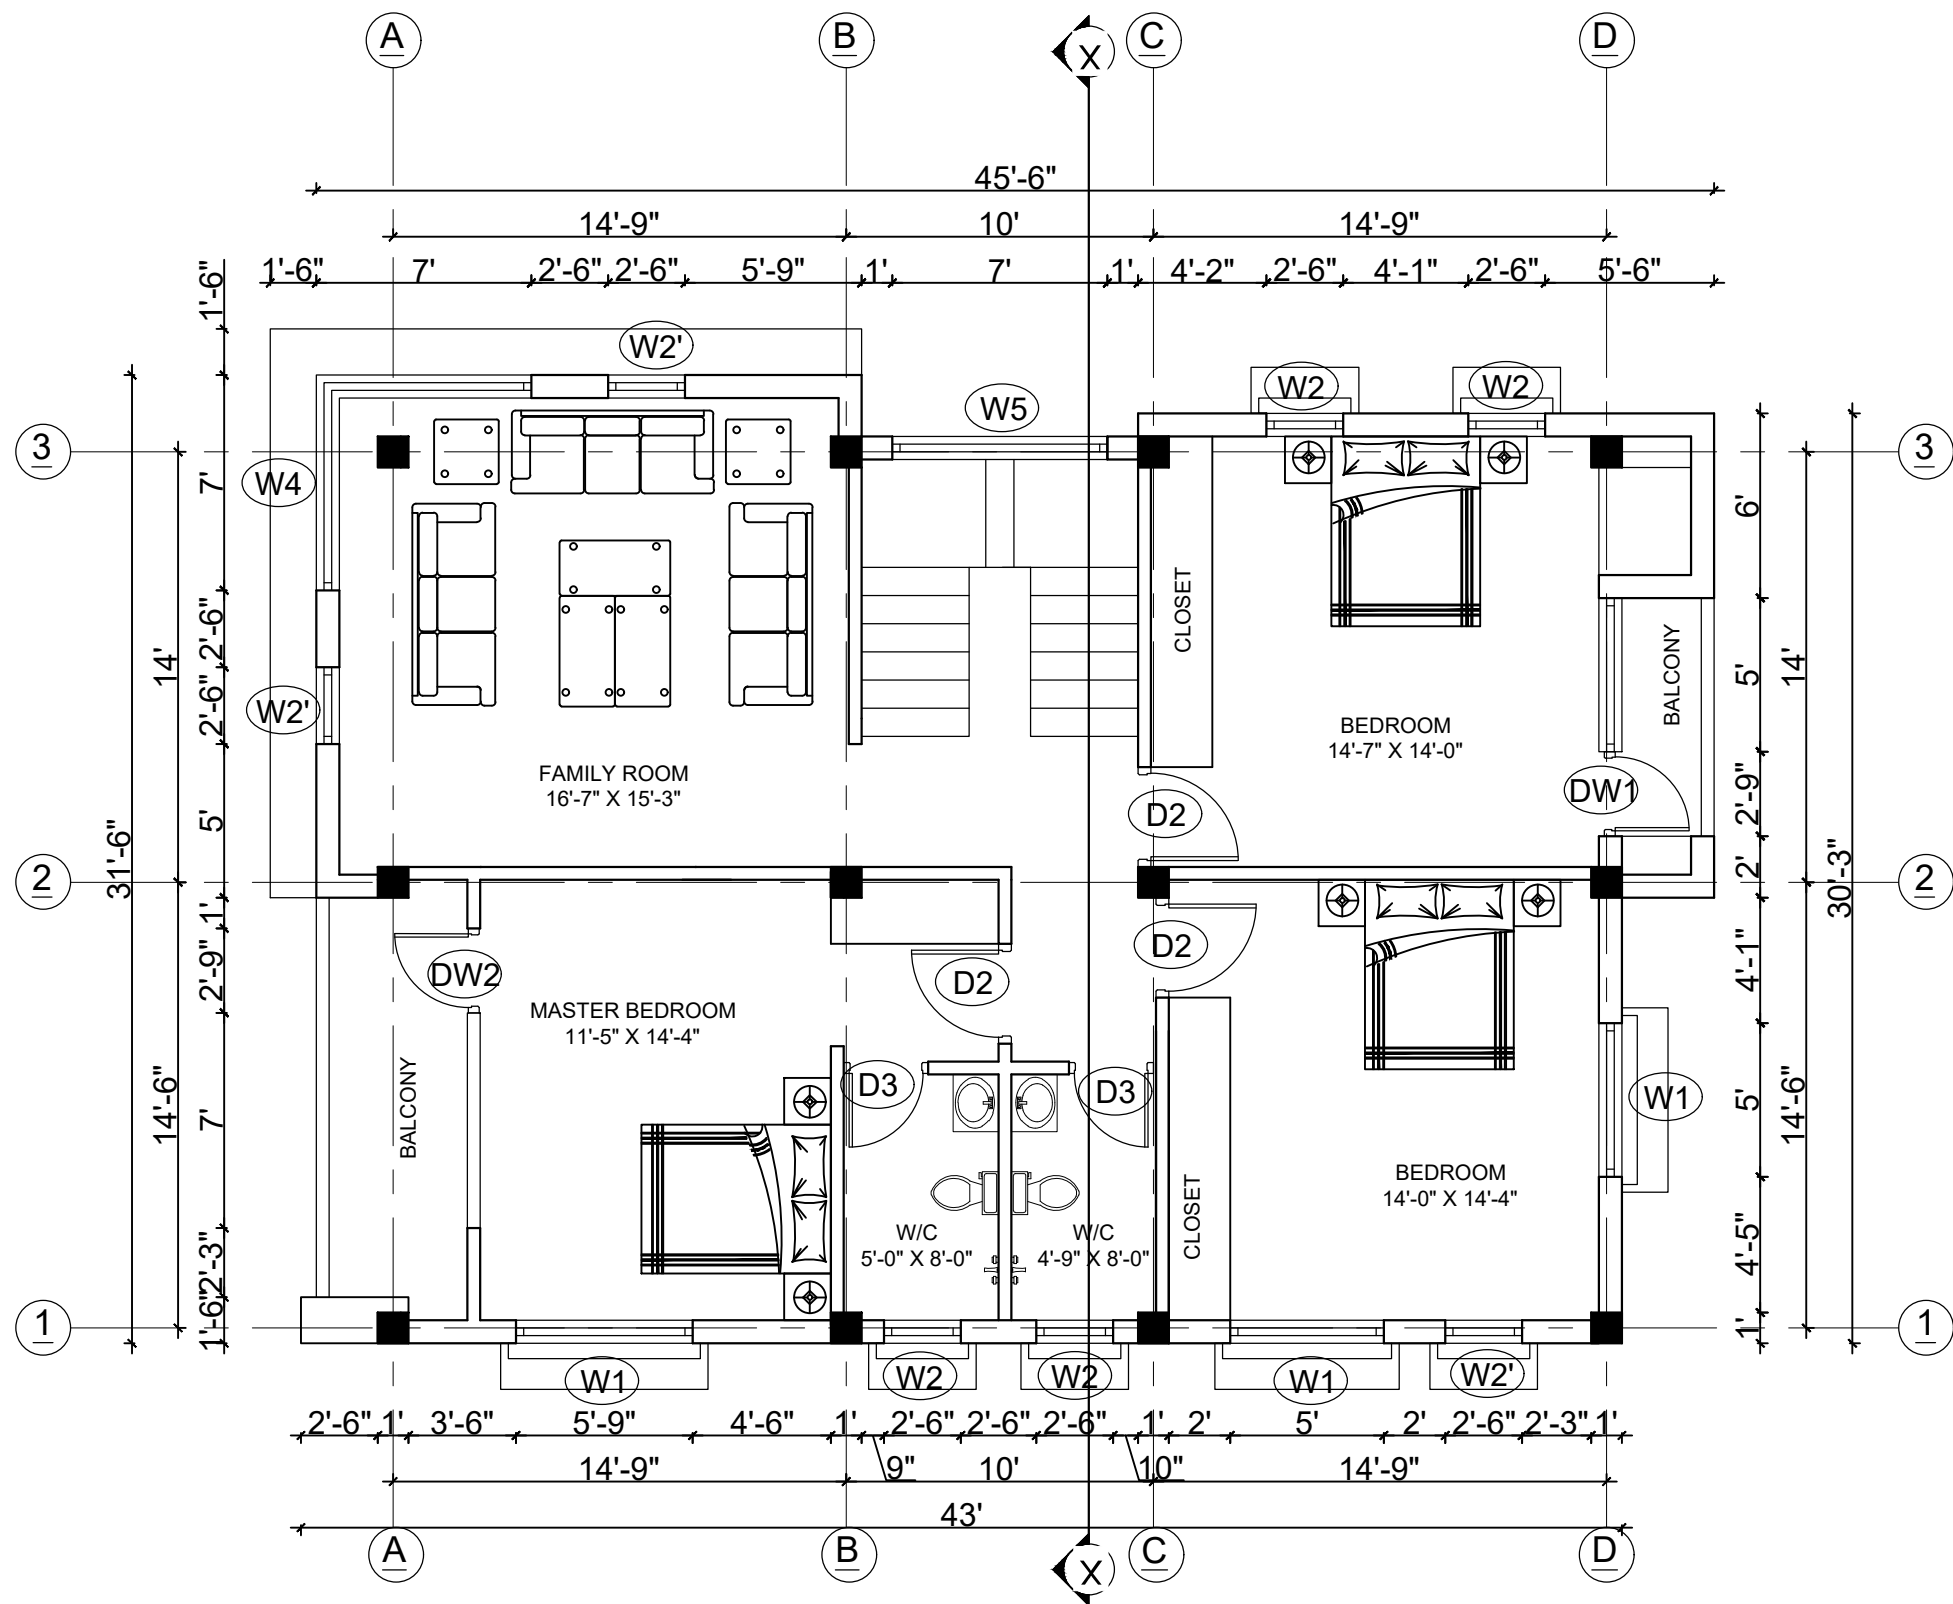

FIRST FLOOR PLAN
FLOOR AREA: 1319.31 SQ.FT

URBAN PARK PVT.LTD

KATHMANDU, NEPAL

RESIDENCE DESIGN

ARCHITECTURAL DRAWING

ARCHITECT:

AR.APIL KC

DRAWN BY:

AR.SAMJHANA MAHARJAN

DATE :

March, 2021


SCALE :

1:75

SHEET NO.

AR

02

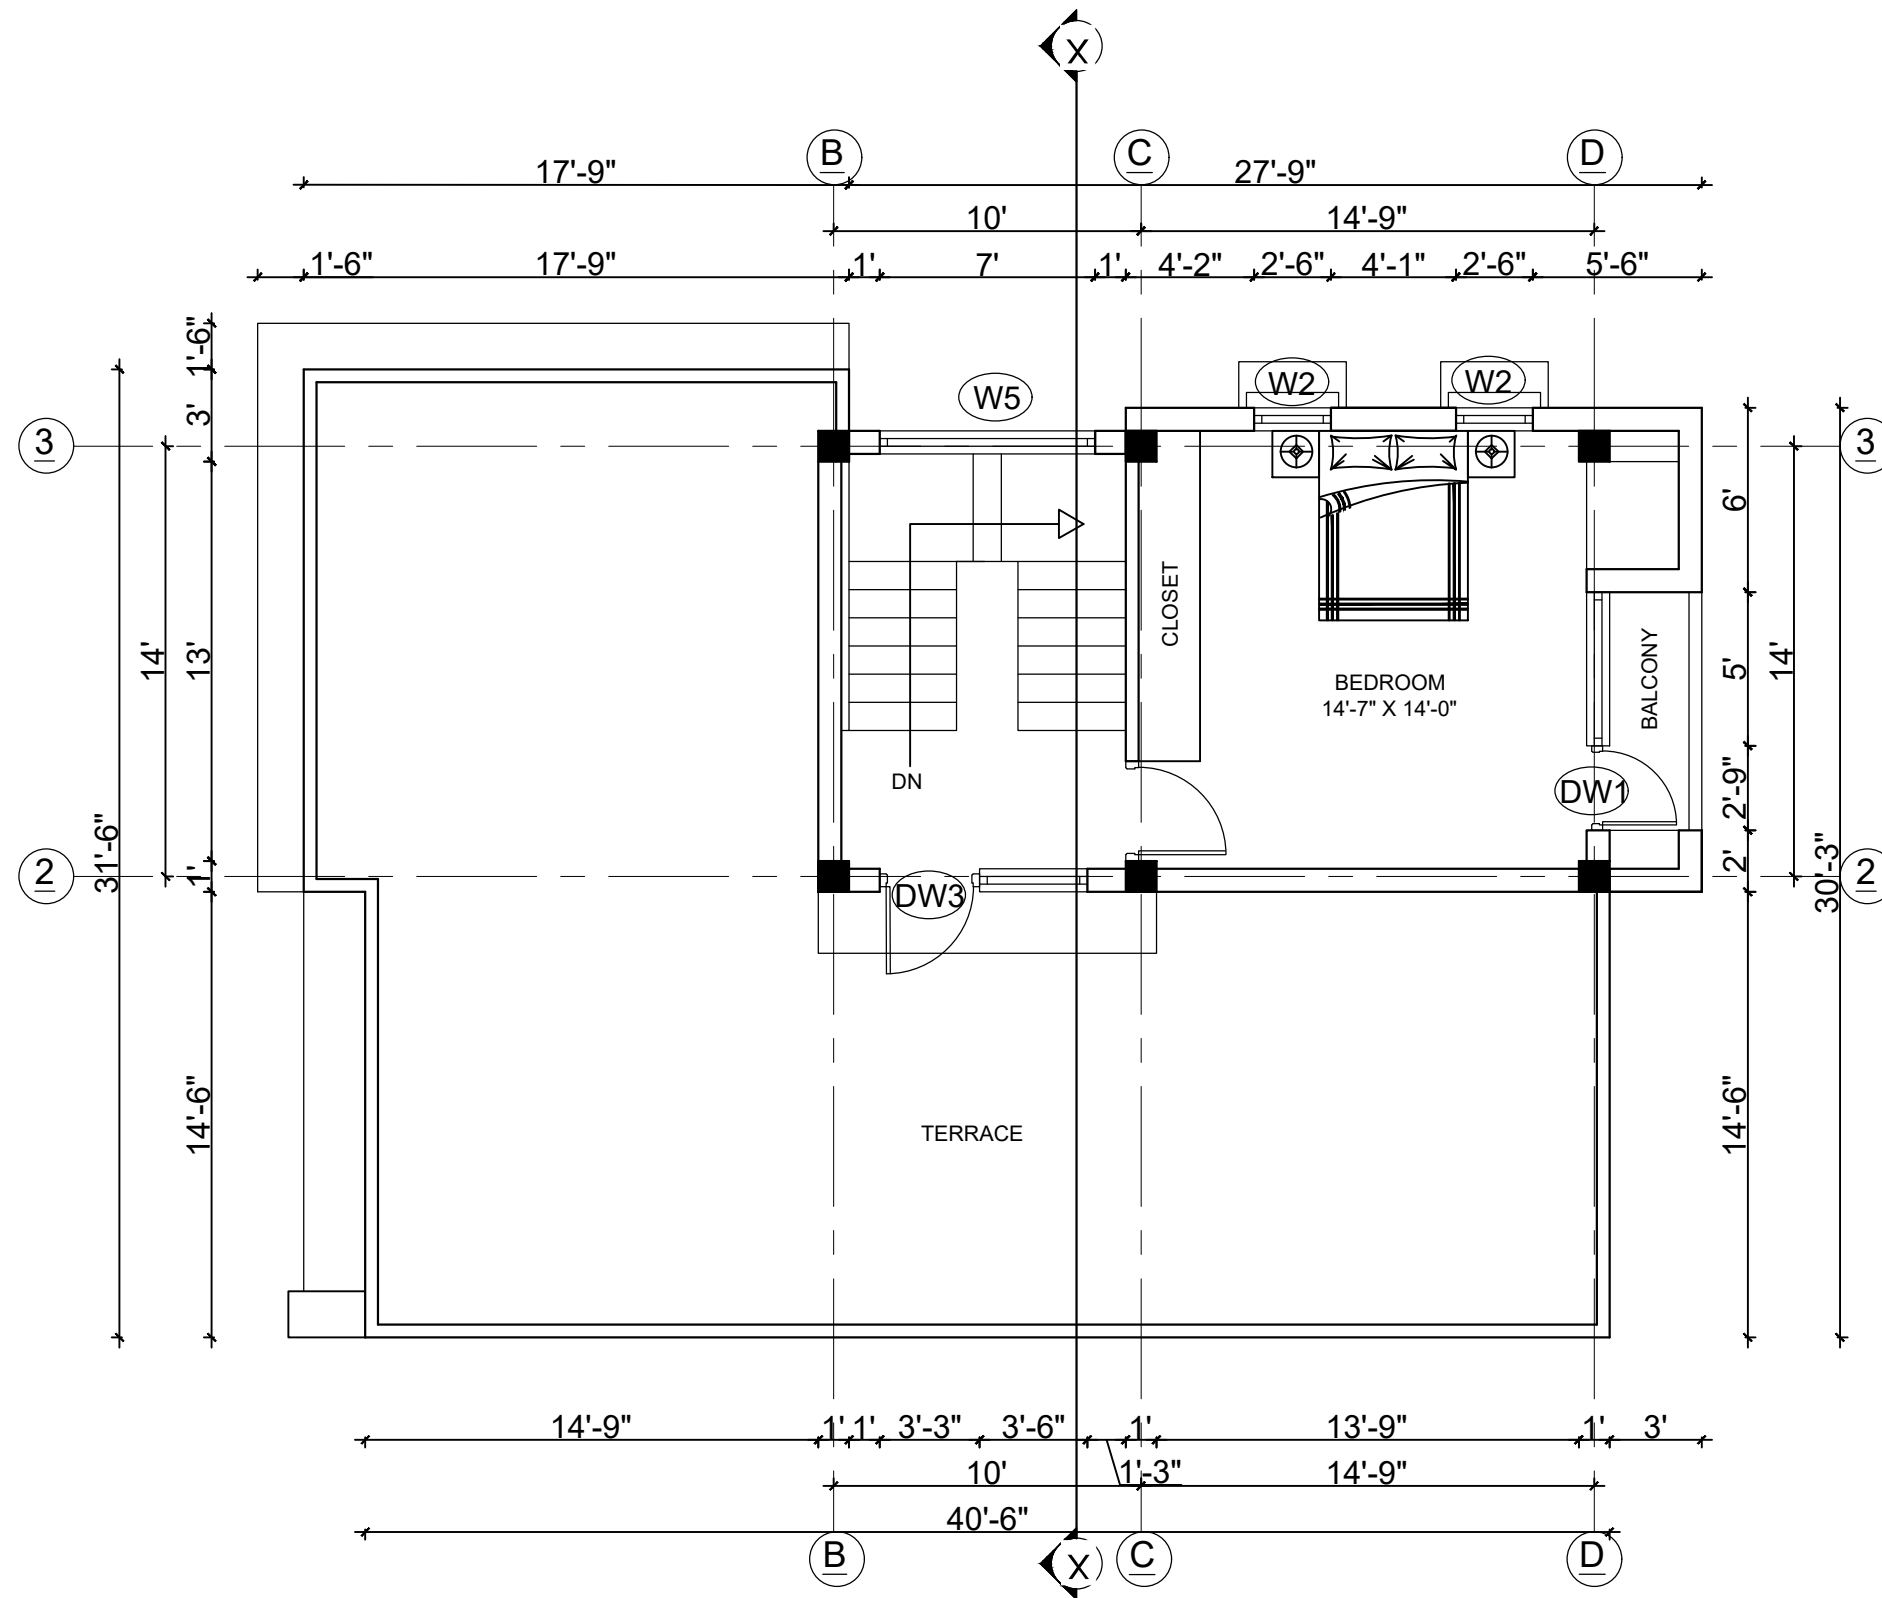

SECOND FLOOR PLAN
FLOOR AREA: 445.31 SQ.FT

URBAN PARK PVT.LTD

KATHMANDU, NEPAL

RESIDENCE DESIGN

ARCHITECTURAL DRAWING

ARCHITECT:

AR.APIL KC

DRAWN BY:

AR.SAMJHANA MAHARJAN

DATE :

March, 2021


SCALE :

1:75

SHEET NO.

AR

03

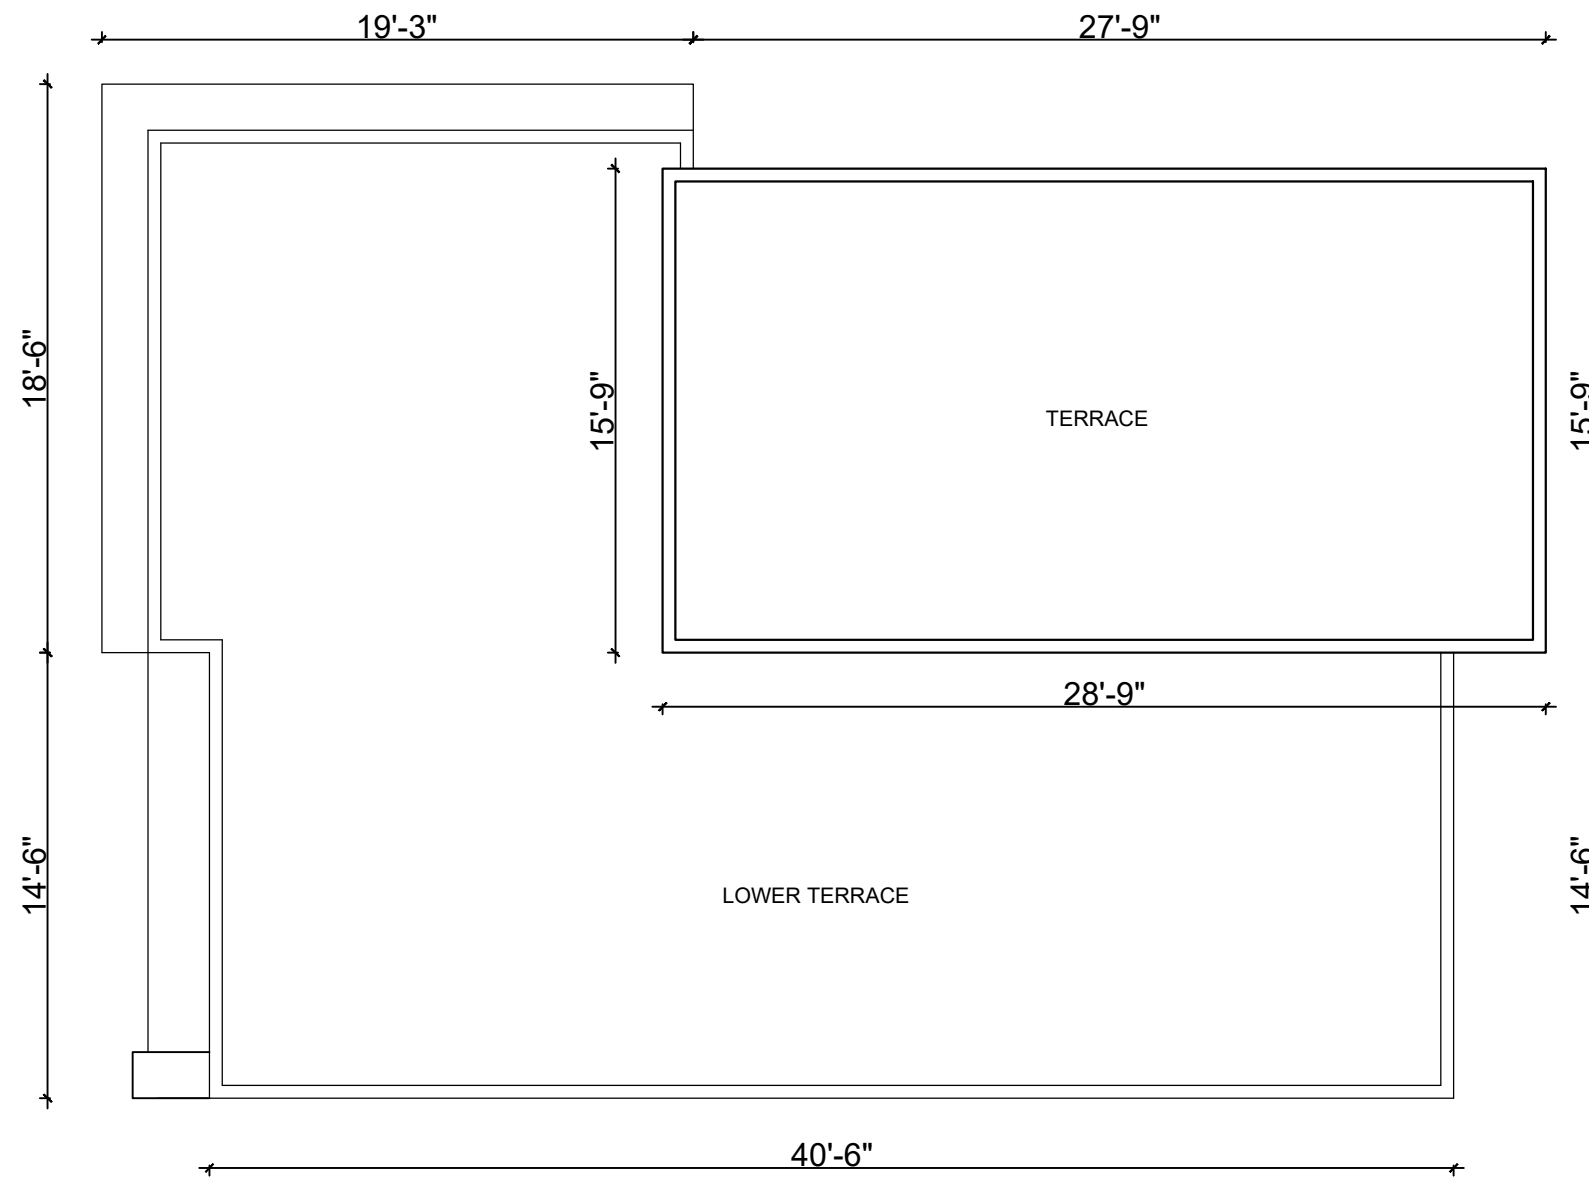

ROOF PLAN

URBAN PARK PVT.LTD

KATHMANDU, NEPAL

RESIDENCE DESIGN

ARCHITECTURAL DRAWING

ARCHITECT:

AR.APIL KC

DRAWN BY:

AR.SAMJHANA MAHARJAN

DATE :

March, 2021


SCALE :

1:75

SHEET NO.

AR

04

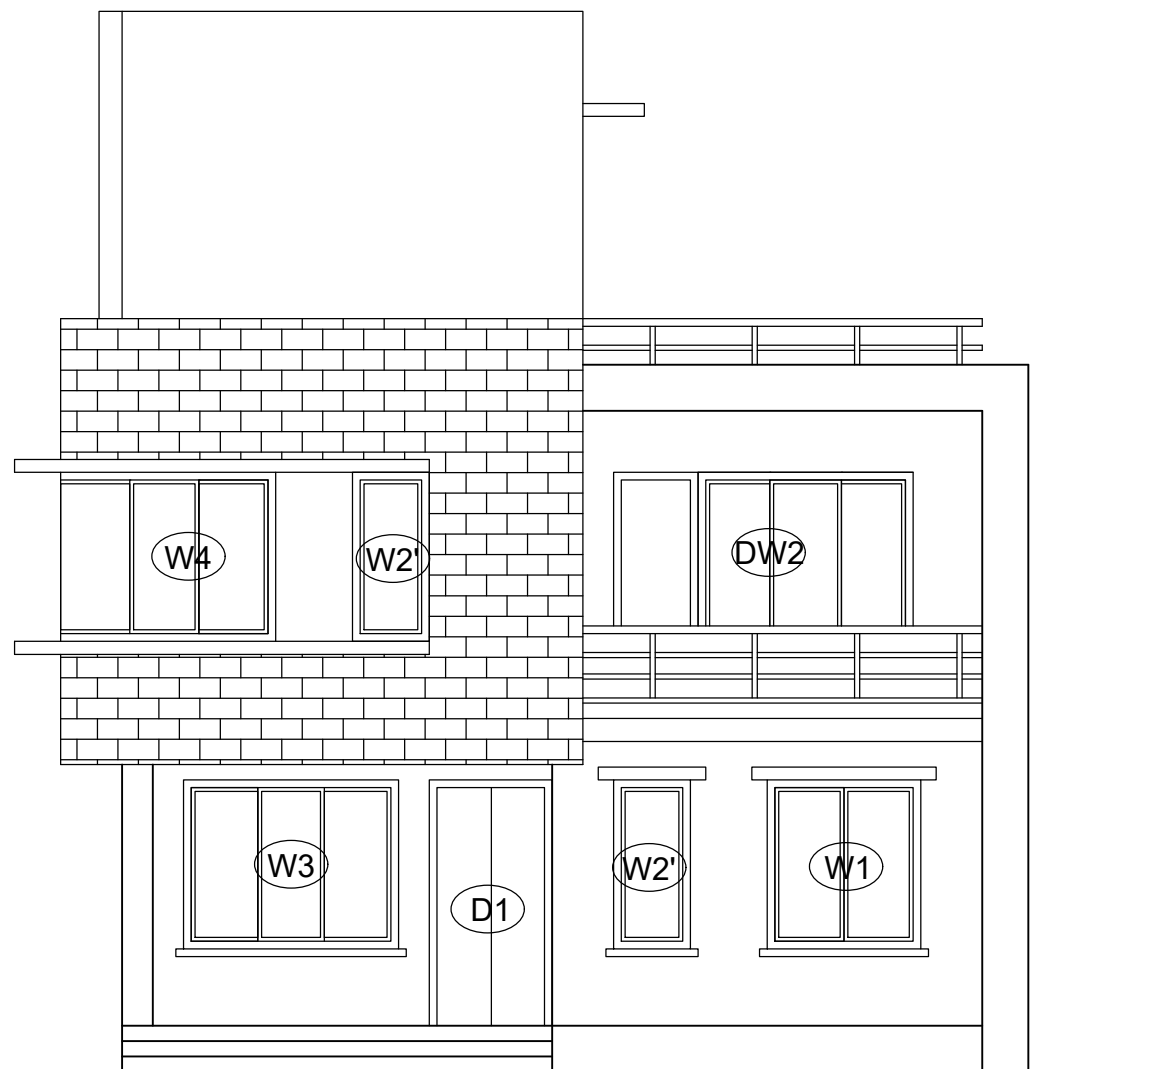

WEST ELEVATION



SOUTH ELEVATION

URBAN PARK PVT.LTD

KATHMANDU, NEPAL

RESIDENCE DESIGN

ARCHITECTURAL DRAWING

ARCHITECT:

AR.APIL KC

DRAWN BY:

AR.SAMJHANA MAHARJAN

DATE :

March, 2021


SCALE :

1:75


SHEET NO.

AR

05

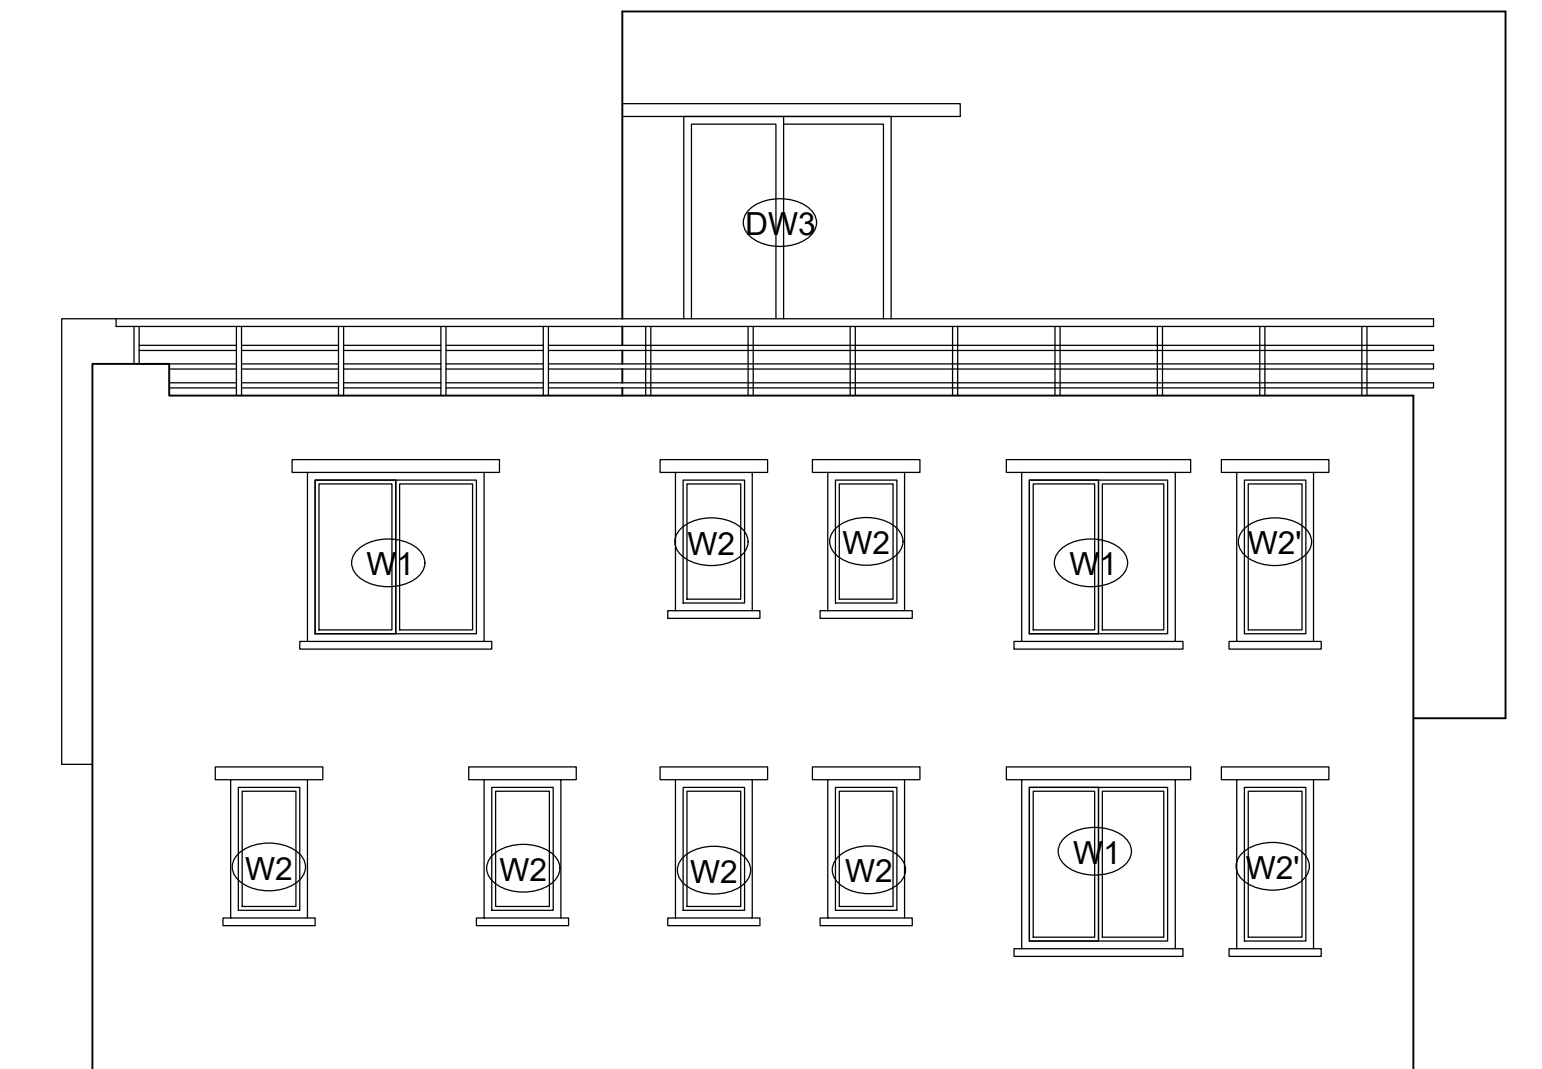

EAST ELEVATION

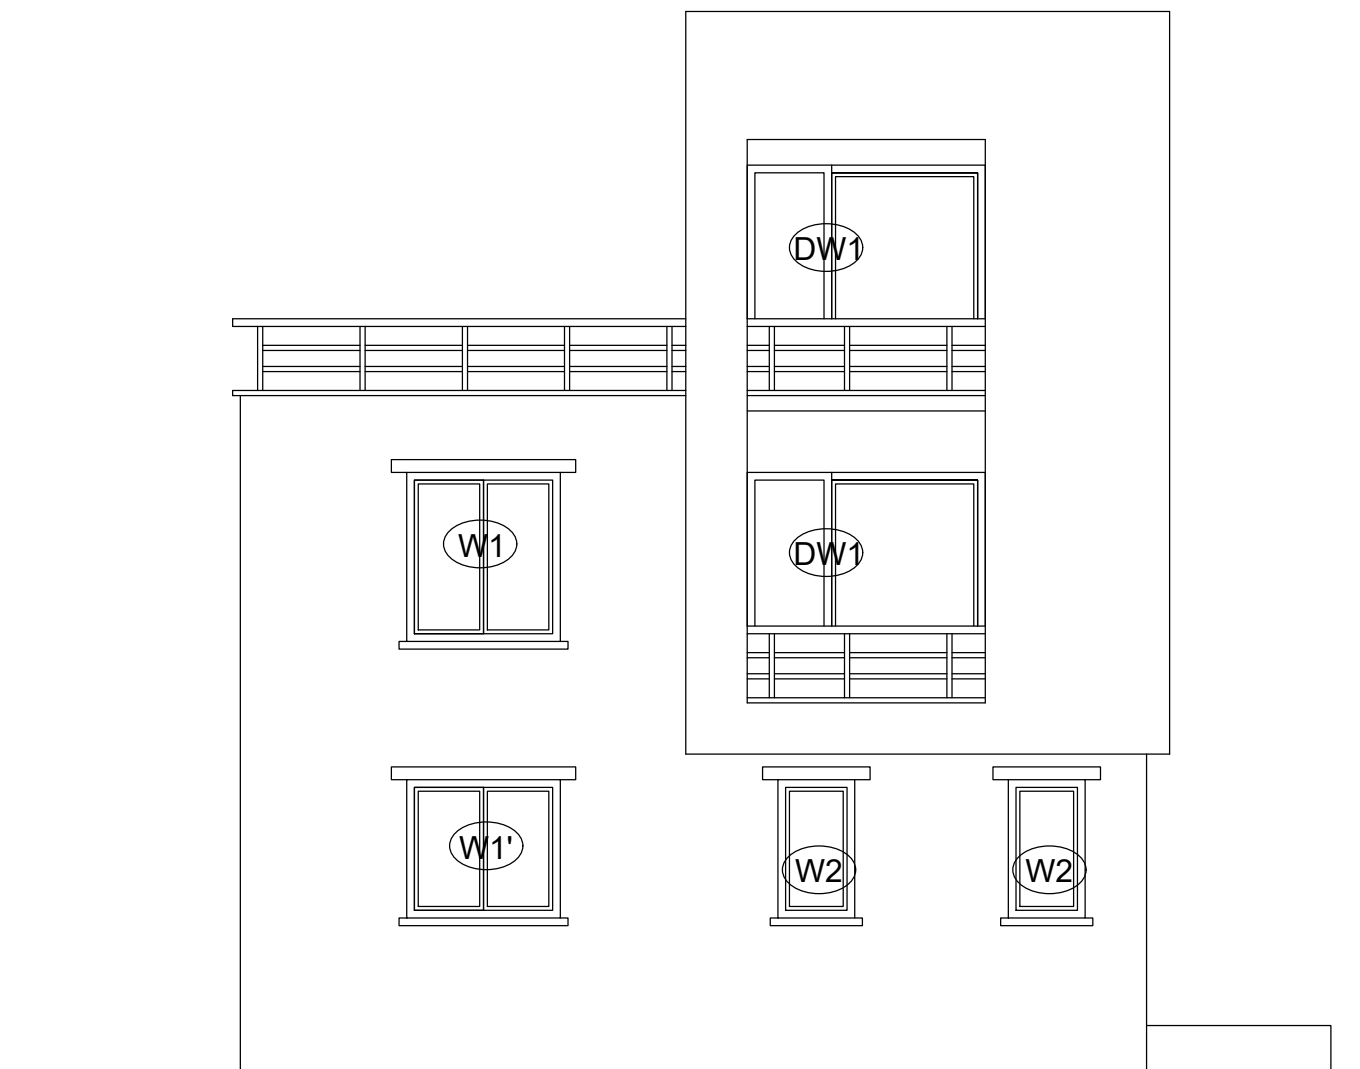

EAST ELEVATION

URBAN PARK PVT.LTD

KATHMANDU, NEPAL

RESIDENCE DESIGN

ARCHITECTURAL DRAWING

ARCHITECT:

AR.APIL KC

DRAWN BY:

AR.SAMJHANA MAHARJAN

DATE :

March, 2021


SCALE :

1:75

SHEET NO.

AR

06

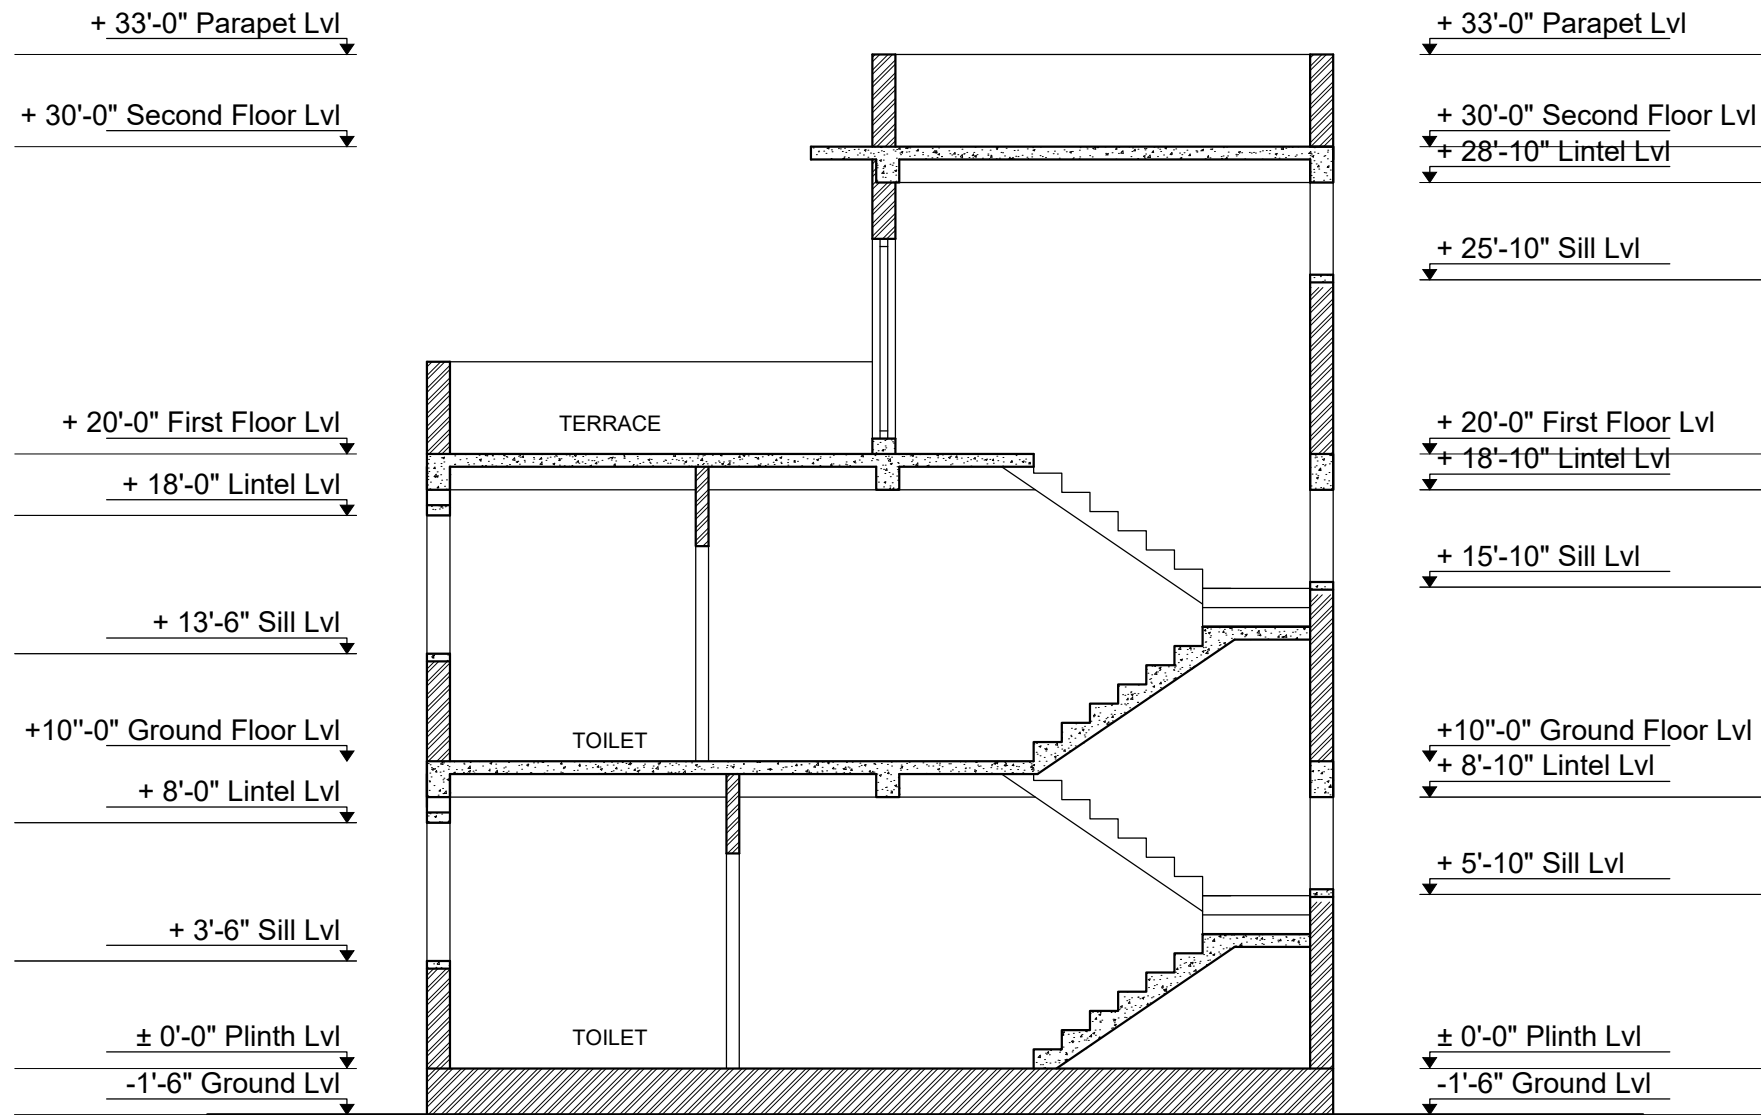

SECTION AT X-X

OPENING SCHEDULE

S.N	DESCRIPTION	SIZE	NO.	SILL
1.	D1	4'-0" X 8'-0"	1	-
2.	D2	3'-3" X 7'-0"	5	-
3.	D3	2'-9" X 7'-0"	4	-
4.	W1	5'-0" X 5'-6"	5	2'-6"
5.	W1'	5'-0" X 4'-6"	1	3'-6"
6.	W2	2'-6" X 4'-6"	12	3'-6"
7.	W2'	2'-6" X 5'-6"	5	2'-6"
8.	W3	7'-0" X 5'-6"	2	2'-6"
9.	W4	7'-0" X 5'-6"	2	2'-6"
10.	W5	7'-0" X 3'-0"	3	STAIRCASE WINDOW
11.	DW1	7'-9" X 7'-6" (7'-9" = 2'-9"(D),5'-0"(W))	2	
12.	DW2	9'-9" X 7'-6" (9'-9" = 2'-9"(D),7'-0"(W))	1	
13.	DW3	6'-9" X 7'-6" (6'-9" = 3'-3"(D),3'-6"(W))	1	0'-6"

URBAN PARK PVT.LTD

KATHMANDU, NEPAL

RESIDENCE DESIGN

ARCHITECTURAL DRAWING

ARCHITECT:

AR.APIL KC

DRAWN BY:

AR.SAMJHANA MAHARJAN

DATE :

March, 2021

SCALE :

1:75

SHEET NO.

AR
07