


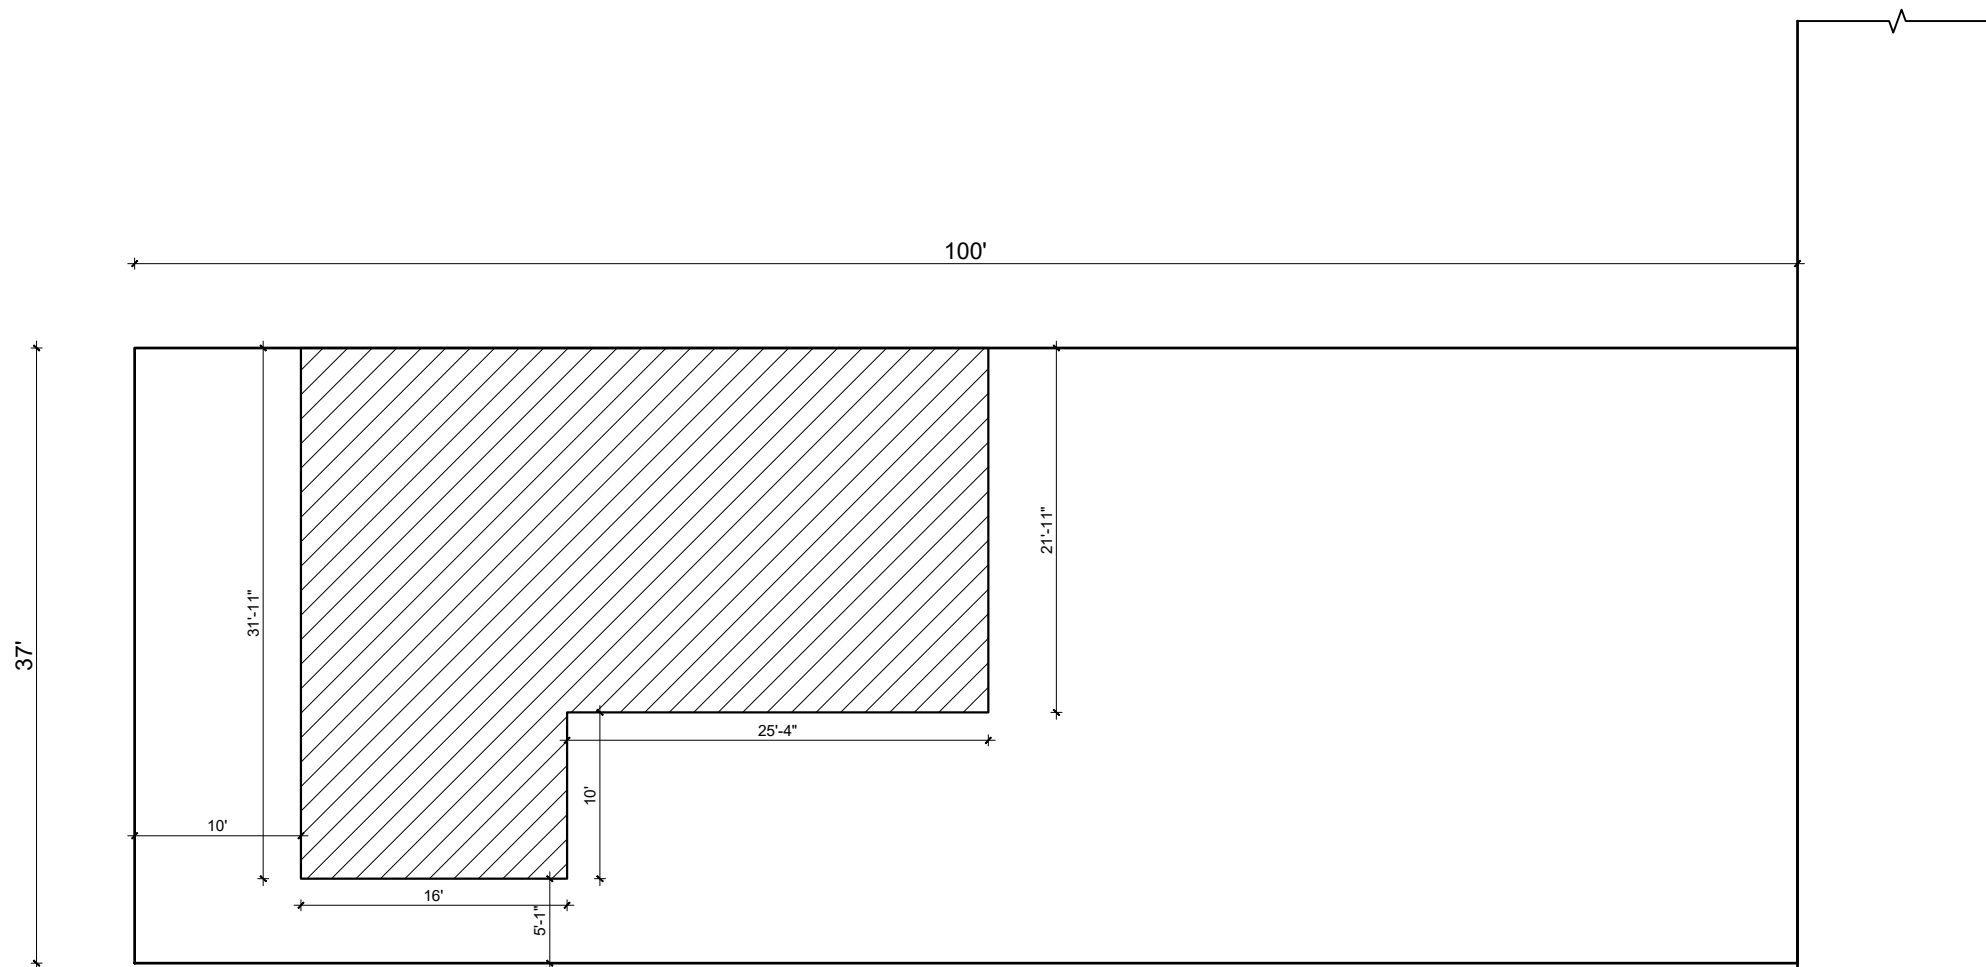

SITE PLAN



URBAN PARK PVT. LTD


BUDDHAGAR, KATHMANDU
urbanparknepal@gmail.com
www.urbanpark.com.np

PROJECT: RESIDENCE DESIGN
BALUWATAR, NEPAL
SHEET: GROUND FLOOR PLAN

ARCHITECT:
AR. APIL K C
AR. GAURAV NEPAL
AR. ANANTA GAUTAM
AR. SAMJHANA MAHARJAN

CIVIL
ENGINEER/
STRUCTURE:
ER. NIRMAL RUWALI

SCALE:

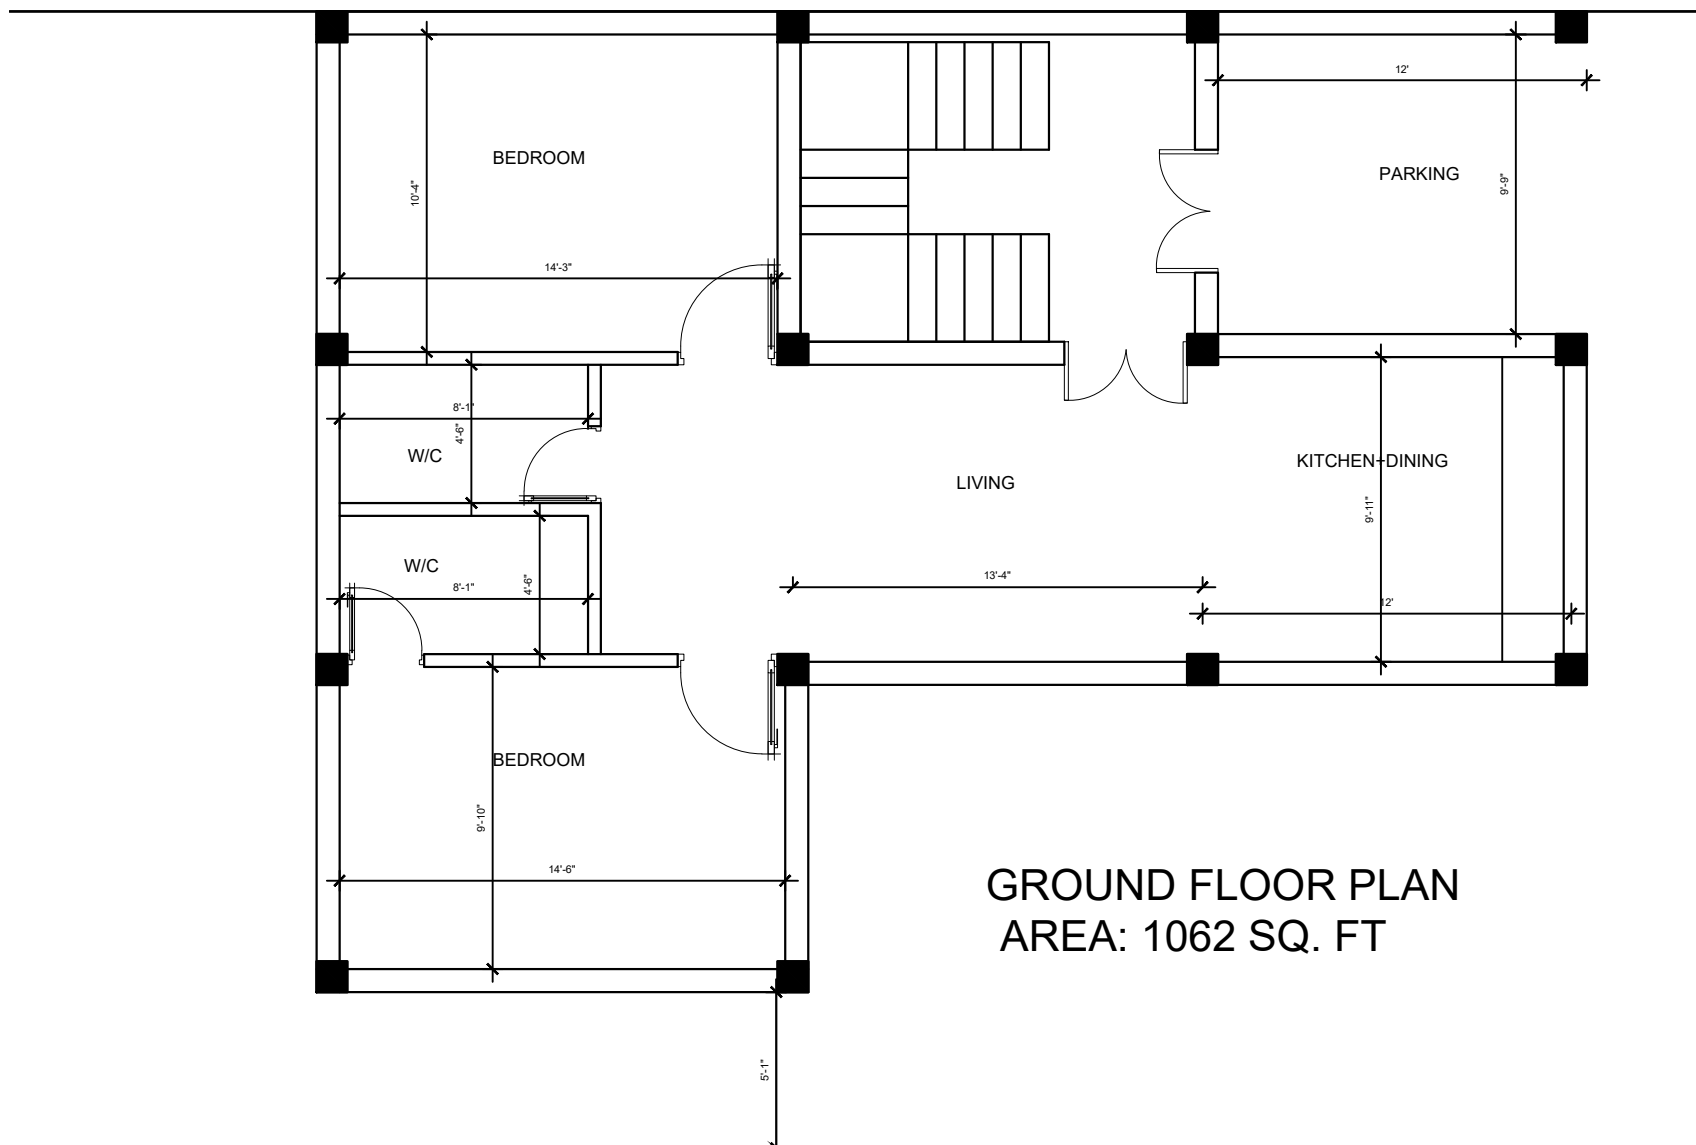

GROUND FLOOR PLAN
AREA: 1062 SQ. FT



URBAN PARK PVT. LTD


BUDDHAGAR, KATHMANDU
urbanparknepal@gmail.com
www.urbanpark.com.np

PROJECT: RESIDENCE DESIGN
BALUWATAR, NEPAL
SHEET: GROUND FLOOR PLAN

ARCHITECT:
AR. APIL K C
AR. GAURAV NEPAL
AR. ANANTA GAUTAM
AR. SAMJHANA MAHARJAN

CIVIL
ENGINEER/
STRUCTURE:
ER. NIRMAL RUWALI

SCALE:

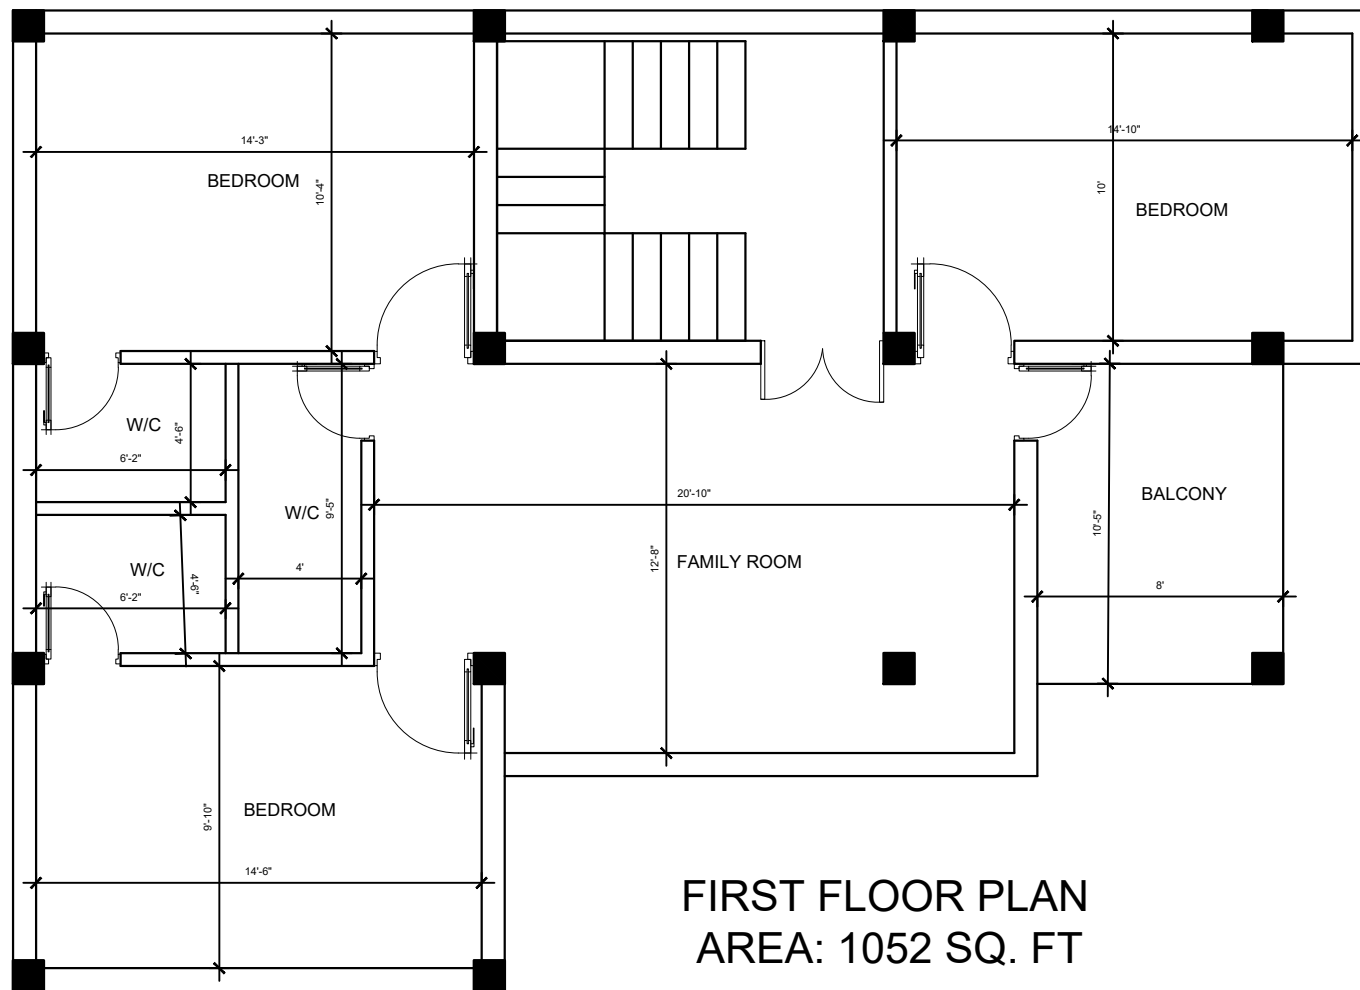

URBAN PARK PVT. LTD

BUDDHAGAR, KATHMANDU
 urbanparknepal@gmail.com
 www.urbanpark.com.np


PROJECT: RESIDENCE DESIGN
 BALUWATAR, NEPAL

SHEET: FIRST FLOOR PLAN

ARCHITECT:
 AR. APIL K C
 AR. GAURAV NEPAL
 AR. ANANTA GAUTAM
 AR. SAMJHANA MAHARJAN

CIVIL
 ENGINEER/
 STRUCTURE:
 ER. NIRMAL RUWALI

SCALE:

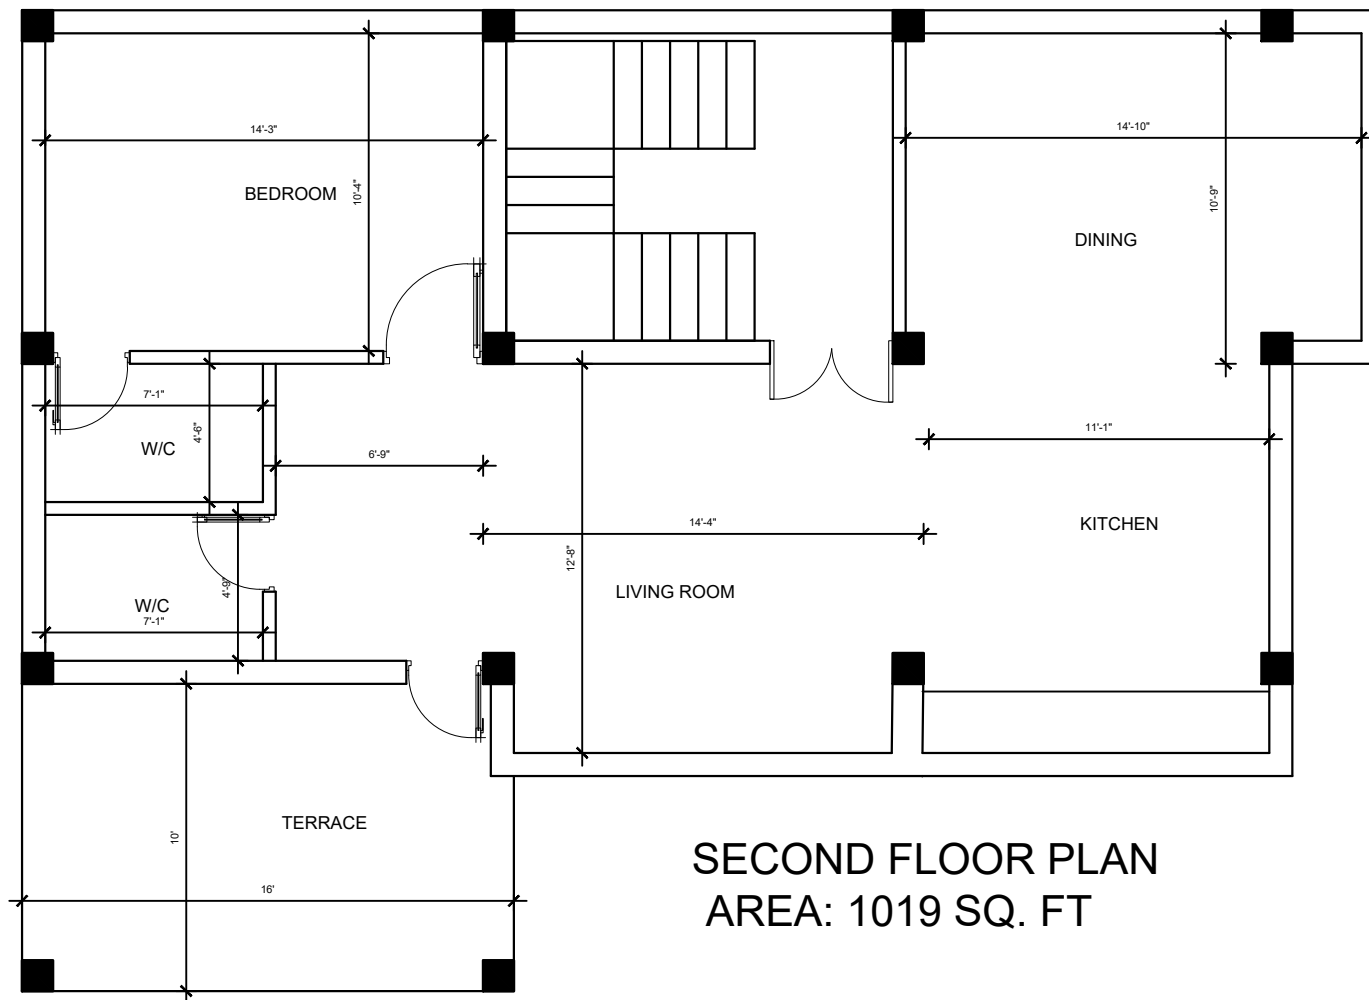

SECOND FLOOR PLAN
AREA: 1019 SQ. FT



URBAN PARK PVT. LTD

BUDDHAGAR, KATHMANDU
 urbanparknepal@gmail.com
 www.urbanpark.com.np

PROJECT: RESIDENCE DESIGN
 BALUWATAR, NEPAL
 SHEET: SANITARY DRAWINGS

ARCHITECT:
 AR. APIL K C
 AR. GAURAV NEPAL
 AR. ANANTA GAUTAM
 AR. SAMJHANA MAHARJAN

CIVIL
 ENGINEER/
 STRUCTURE:
 ER. NIRMAL RUWALI

SCALE: