


ARCHITECTURE DRAWINGS

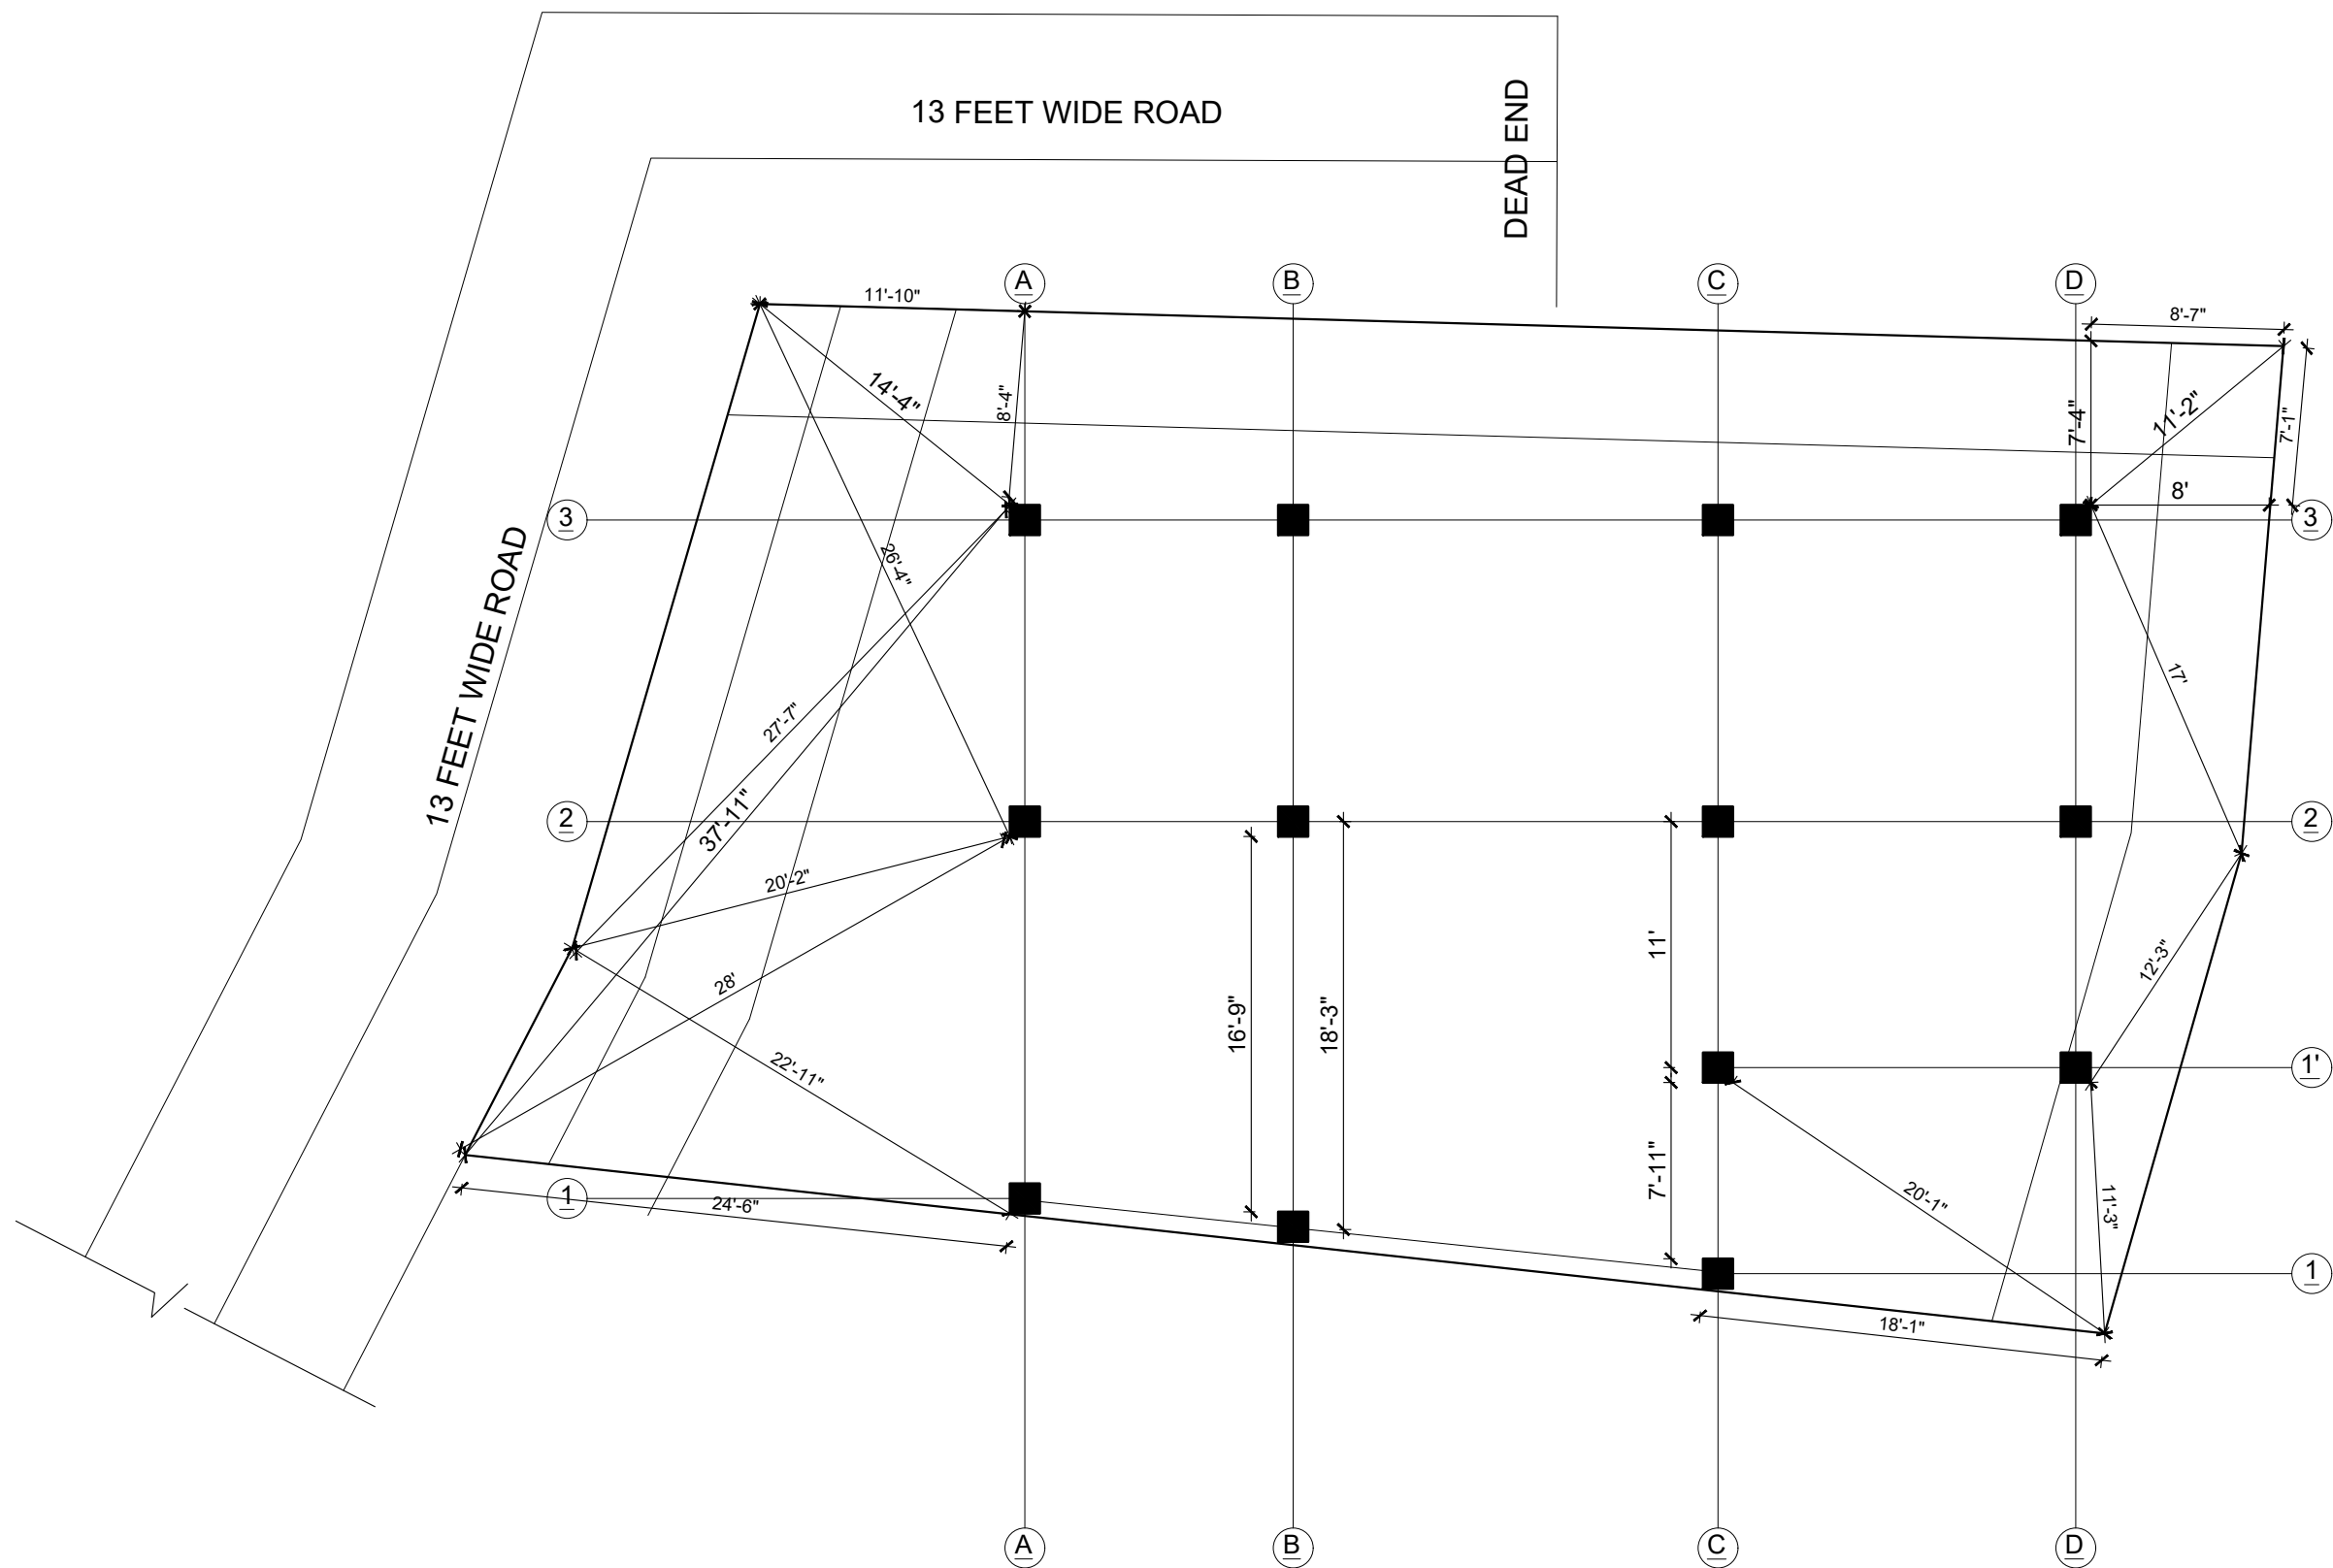

BASEMENT FLOOR PLAN
FLOOR AREA: 1494 SQ.FT

URBAN PARK PVT. LTD

BUDDHAGAR, KATHMANDU
urbanparknepal@gmail.com
www.urbanpark.com.np

RESIDENCE DESIGN

CLIENT: MR. MANDIP SUBEDI

SHEET: BASEMENT FLOOR PAN

ARCHITECT:


AR. APIL K.C.
AR. ANANTA GAUTAM

CIVIL
ENGINEER/
STRUCTURE:


ER. SUJAN ACHARYA


SCALE:

1:100

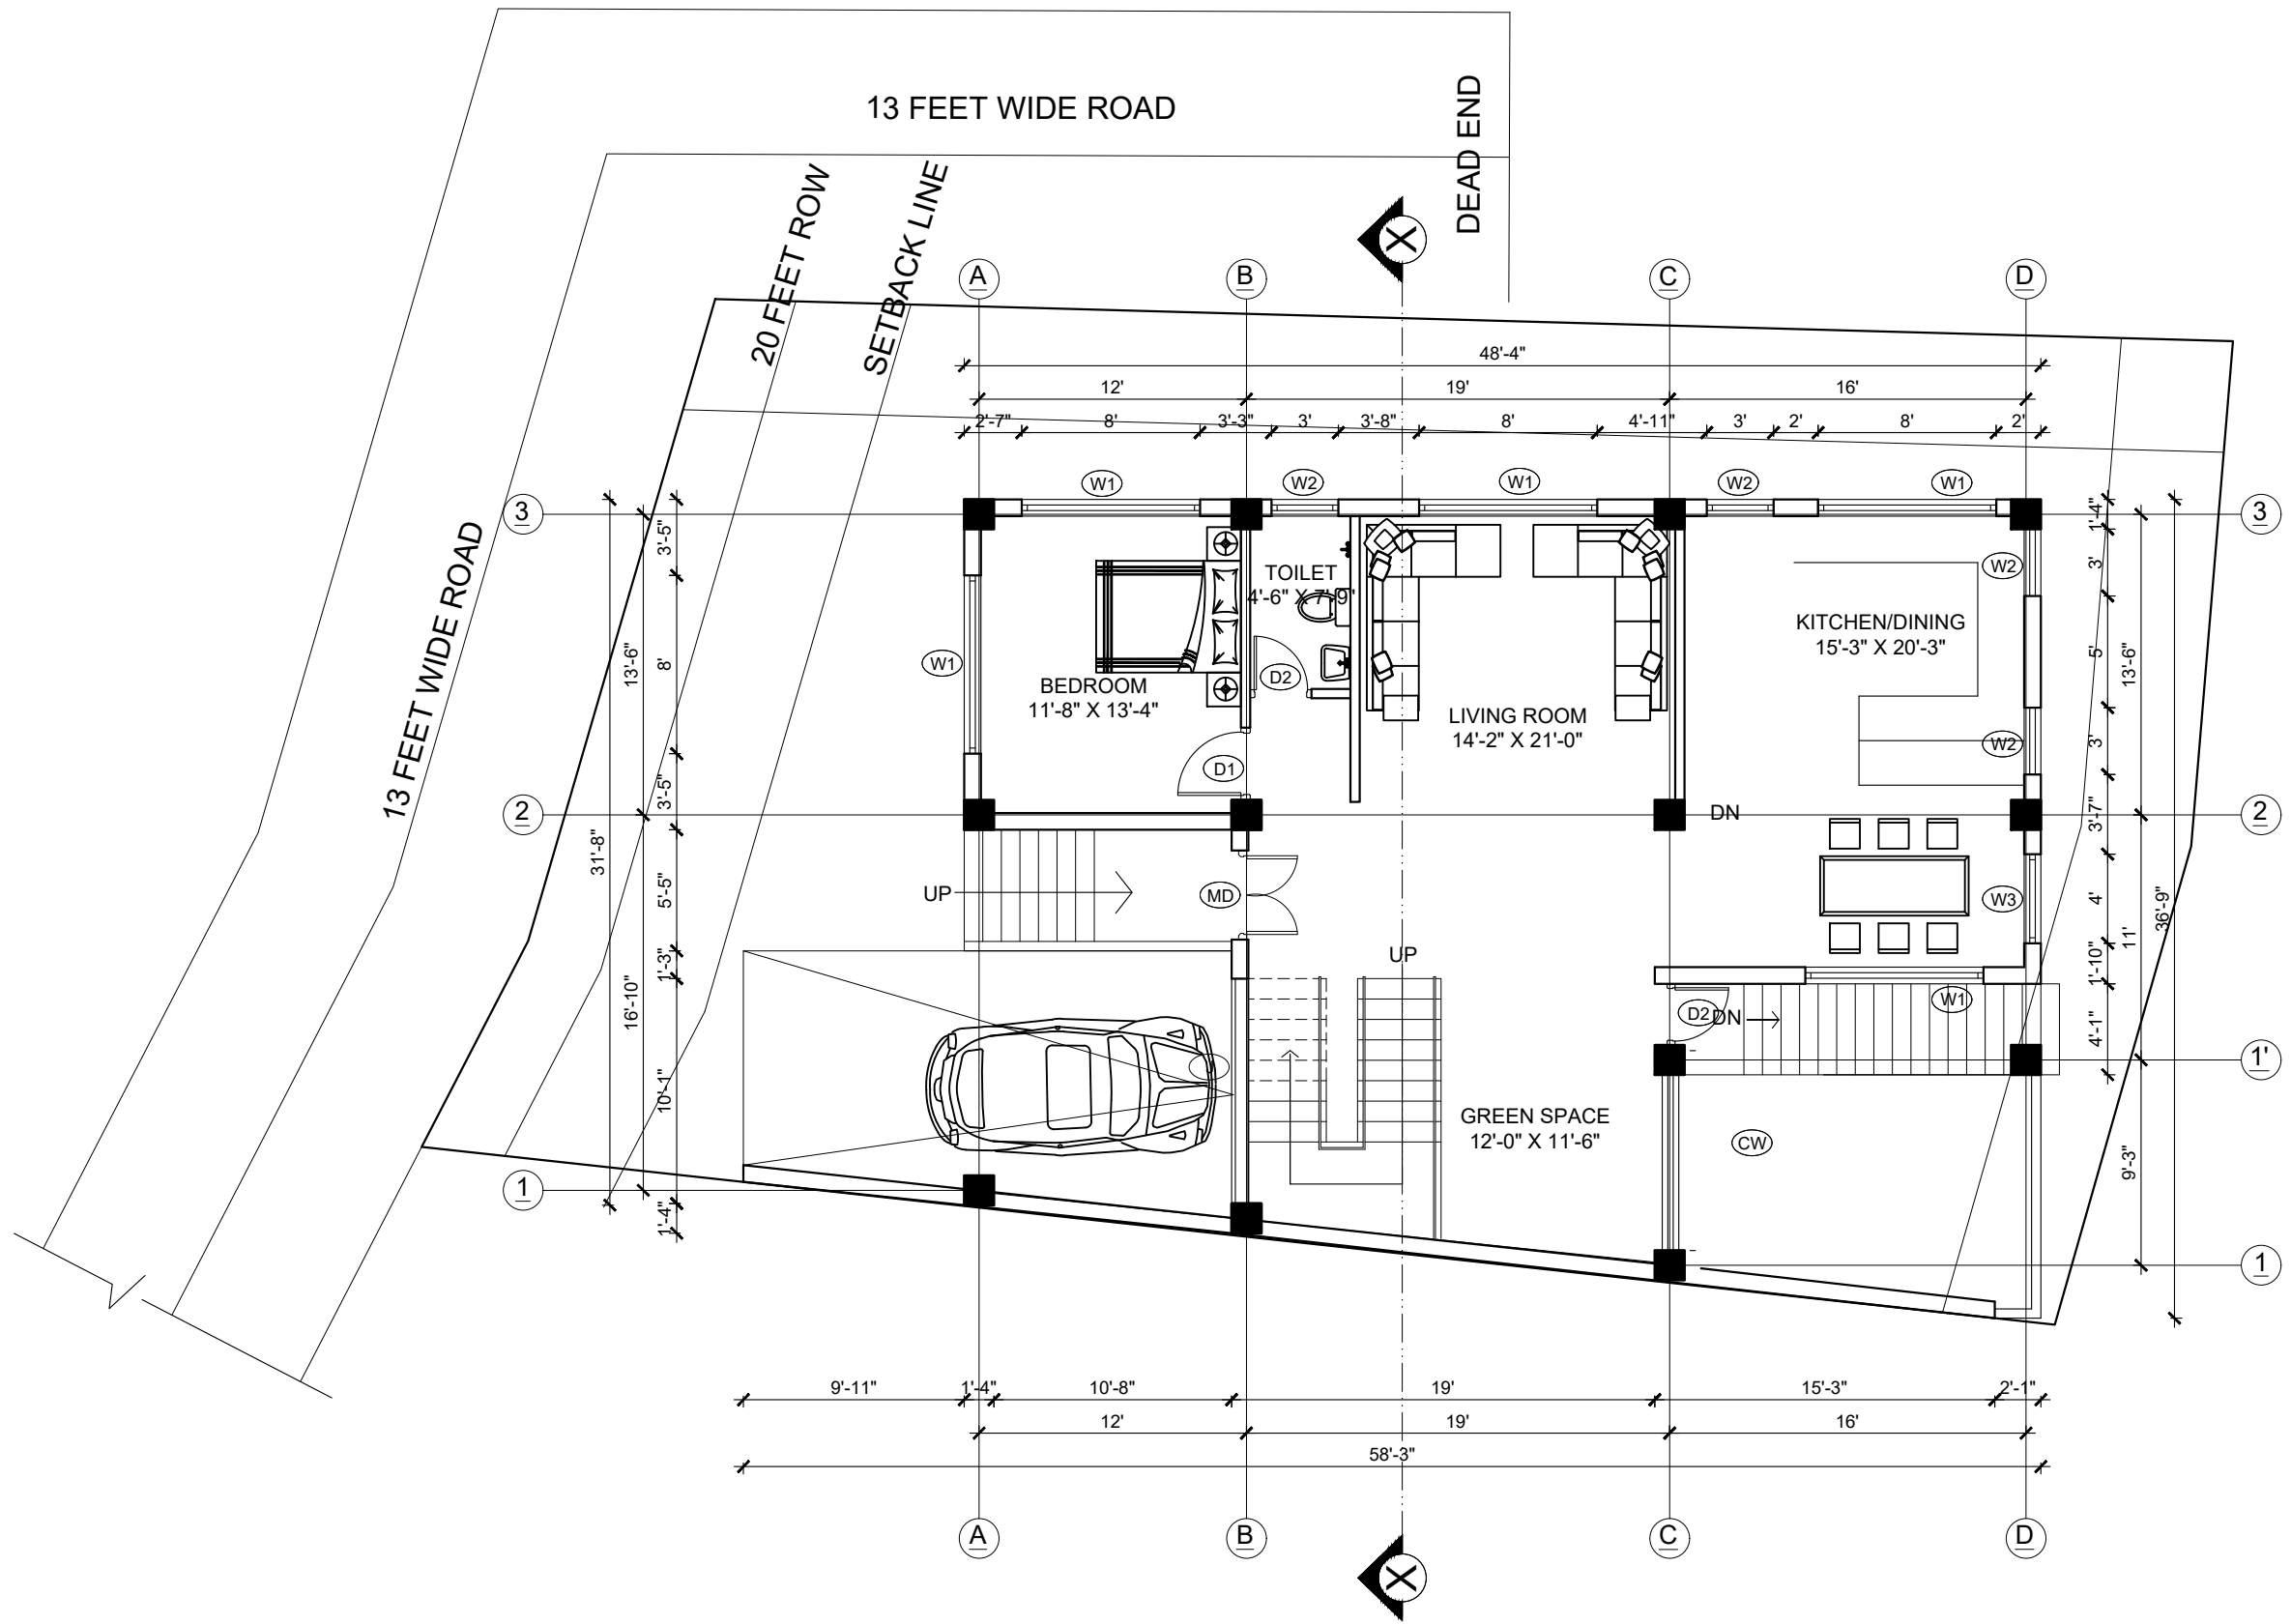


GROUND FLOOR PLAN
FLOOR AREA: 1494 SQ.FT

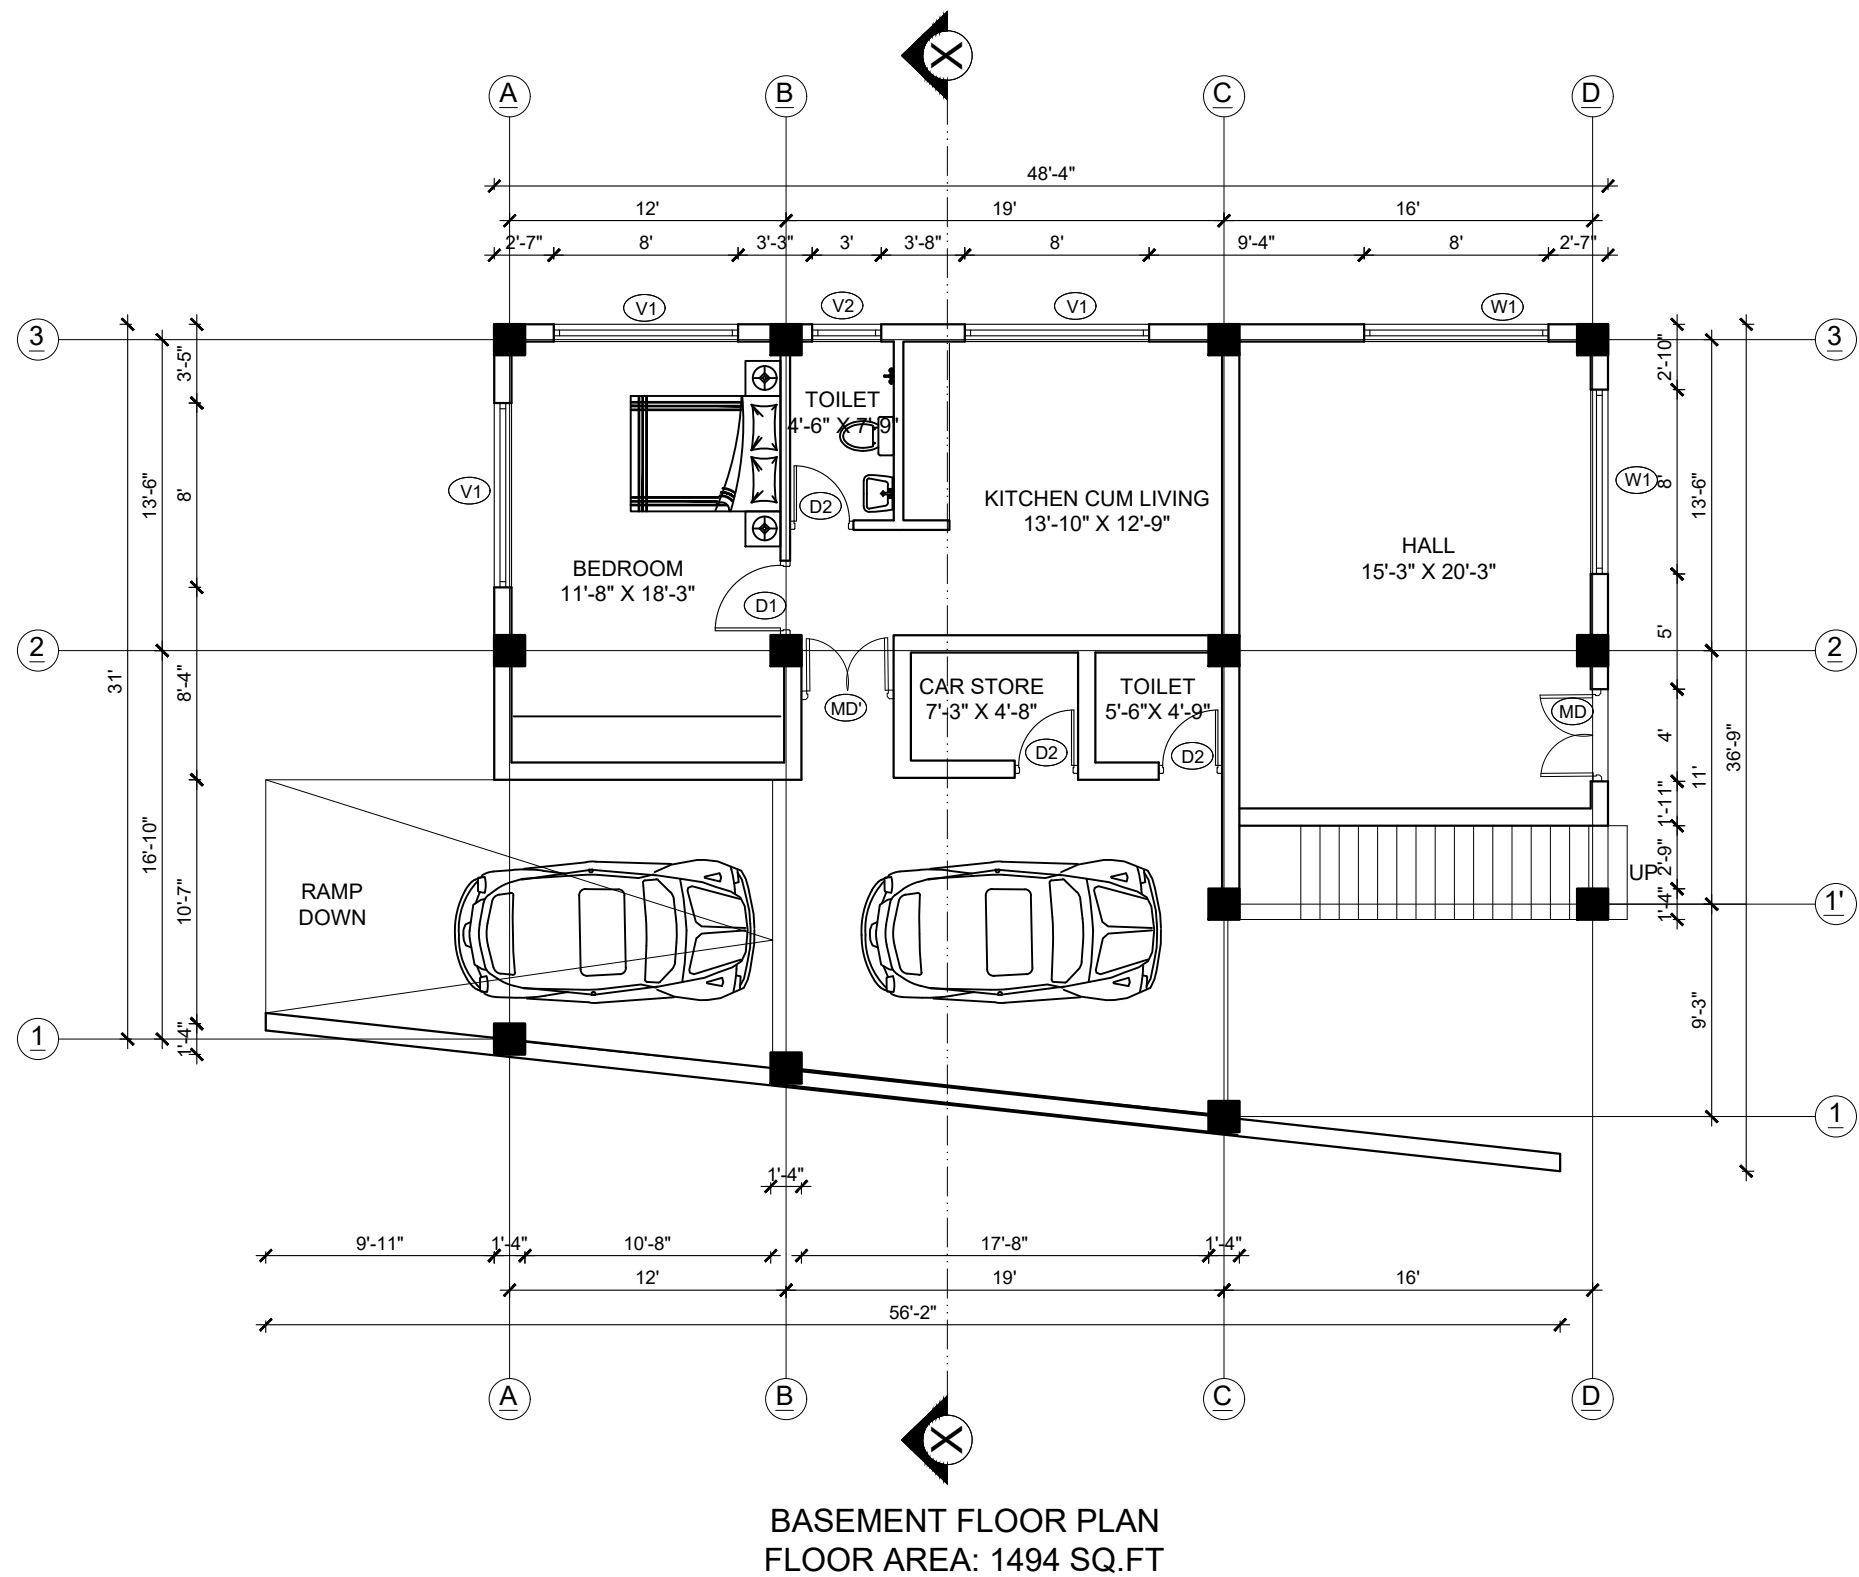


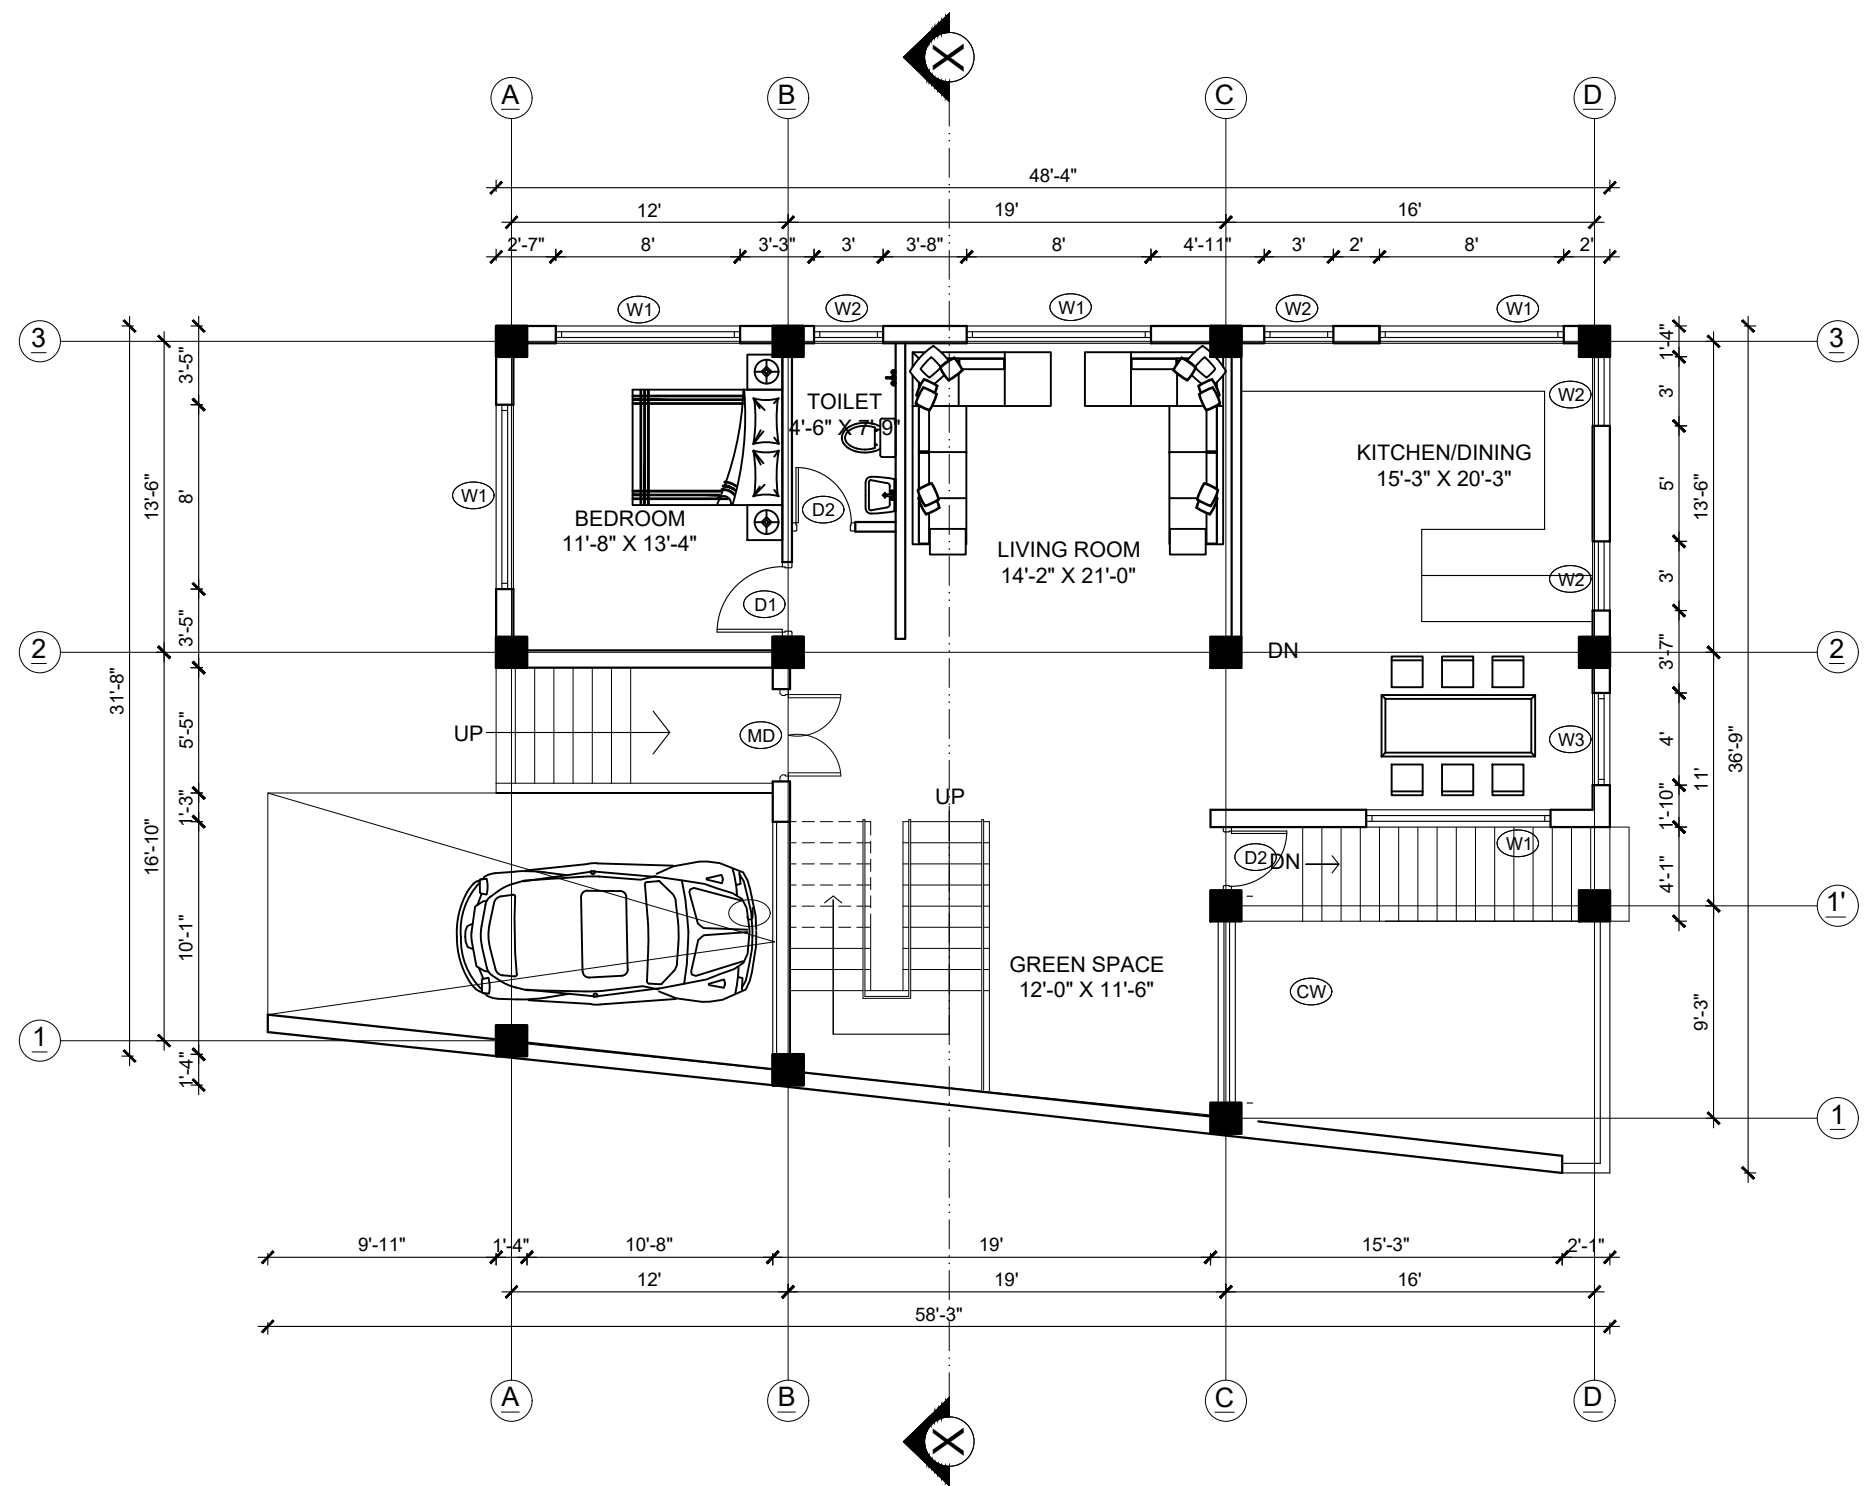


GROUND FLOOR PLAN
FLOOR AREA: 1494 SQ.FT

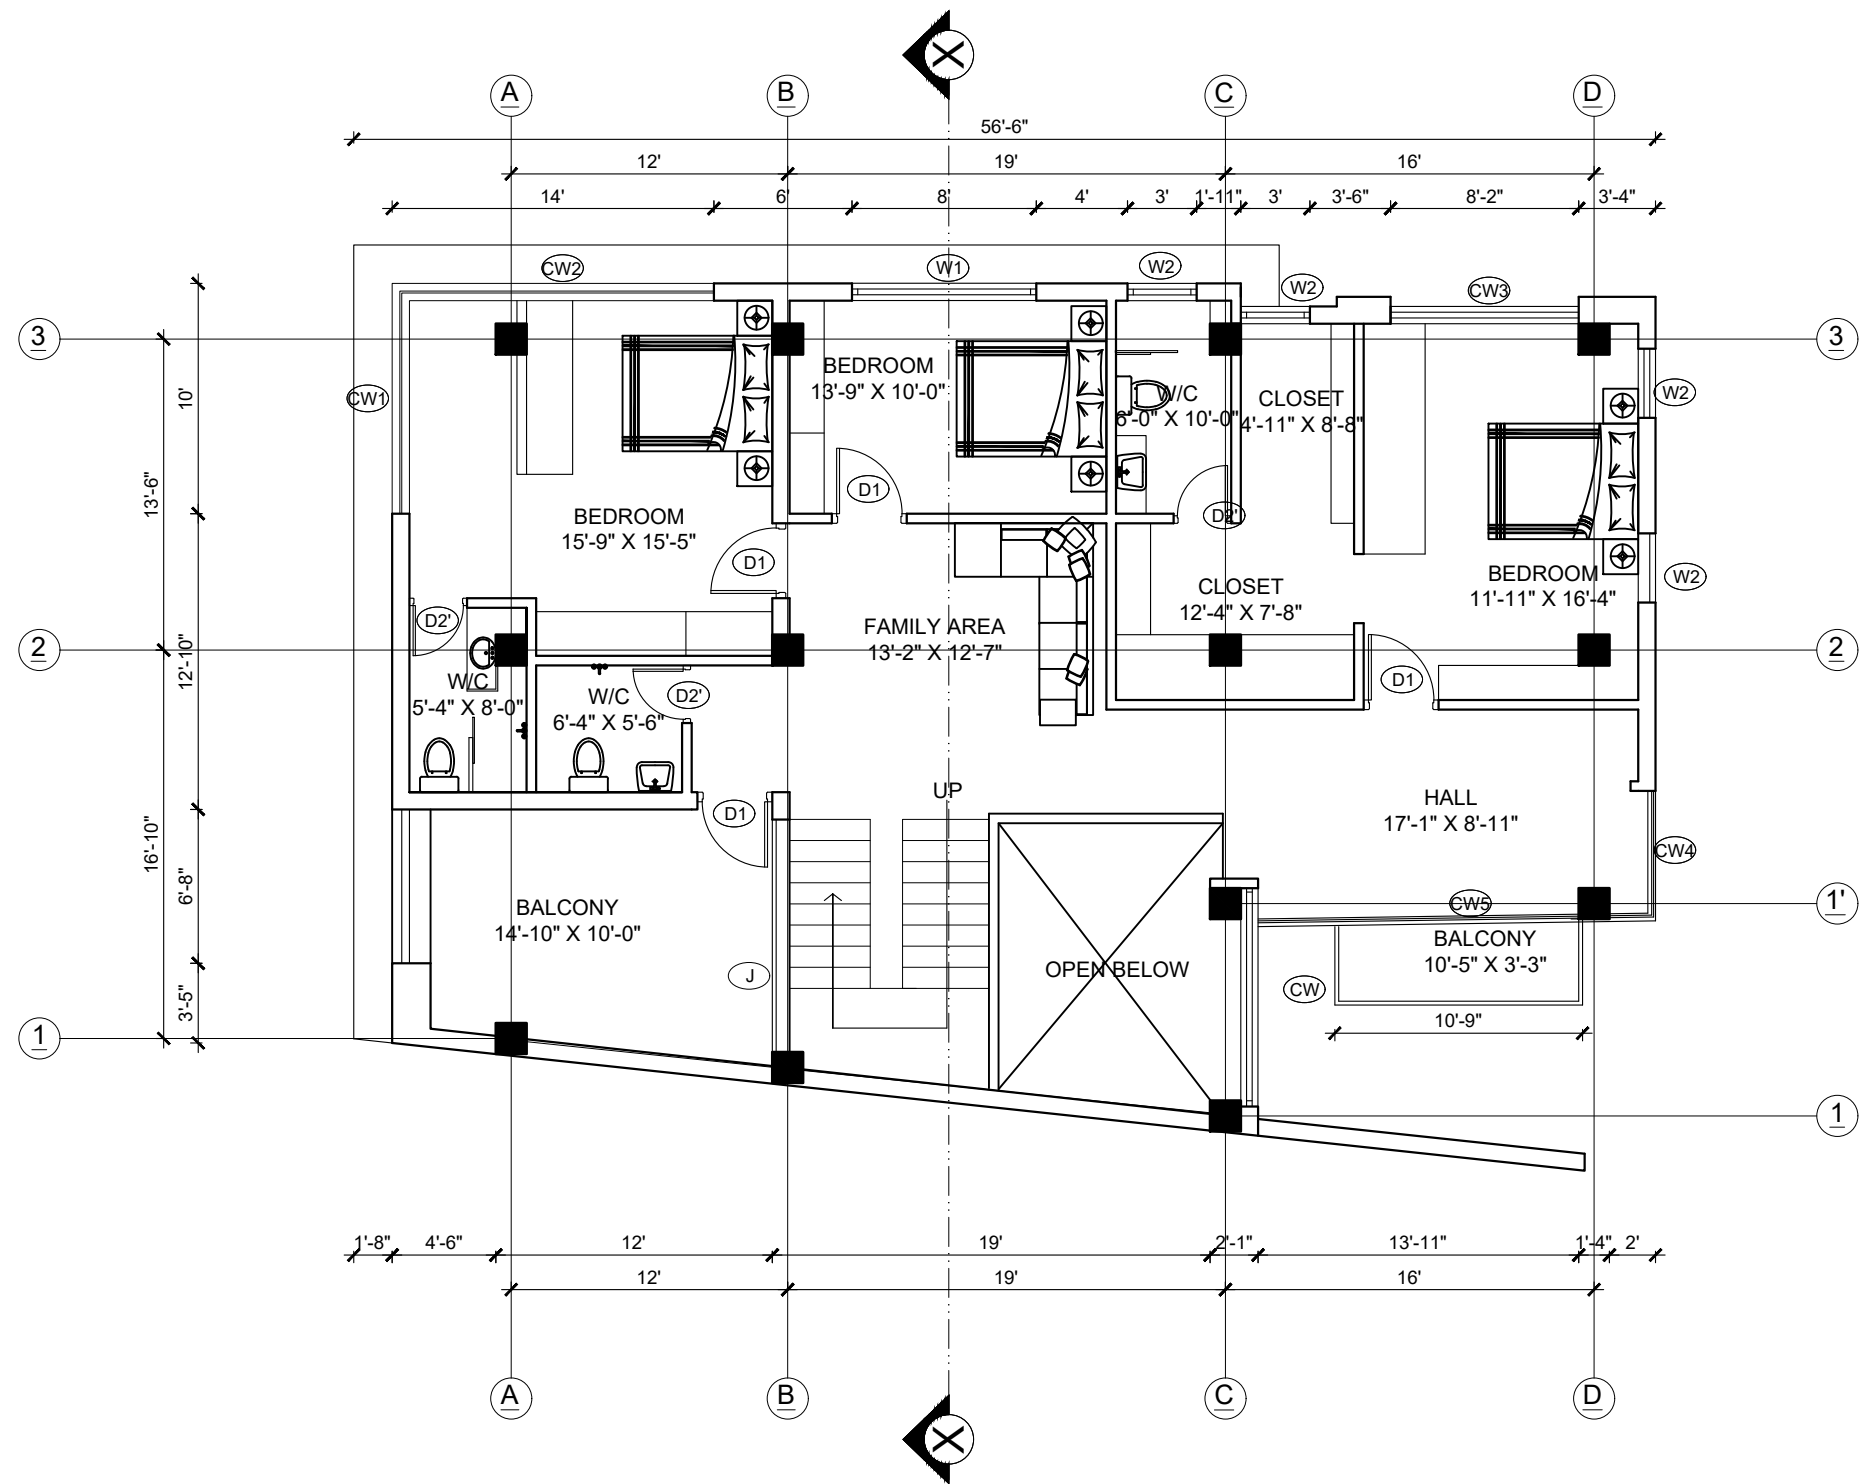


FIRST FLOOR PLAN
FLOOR AREA: 1779 SQ.FT

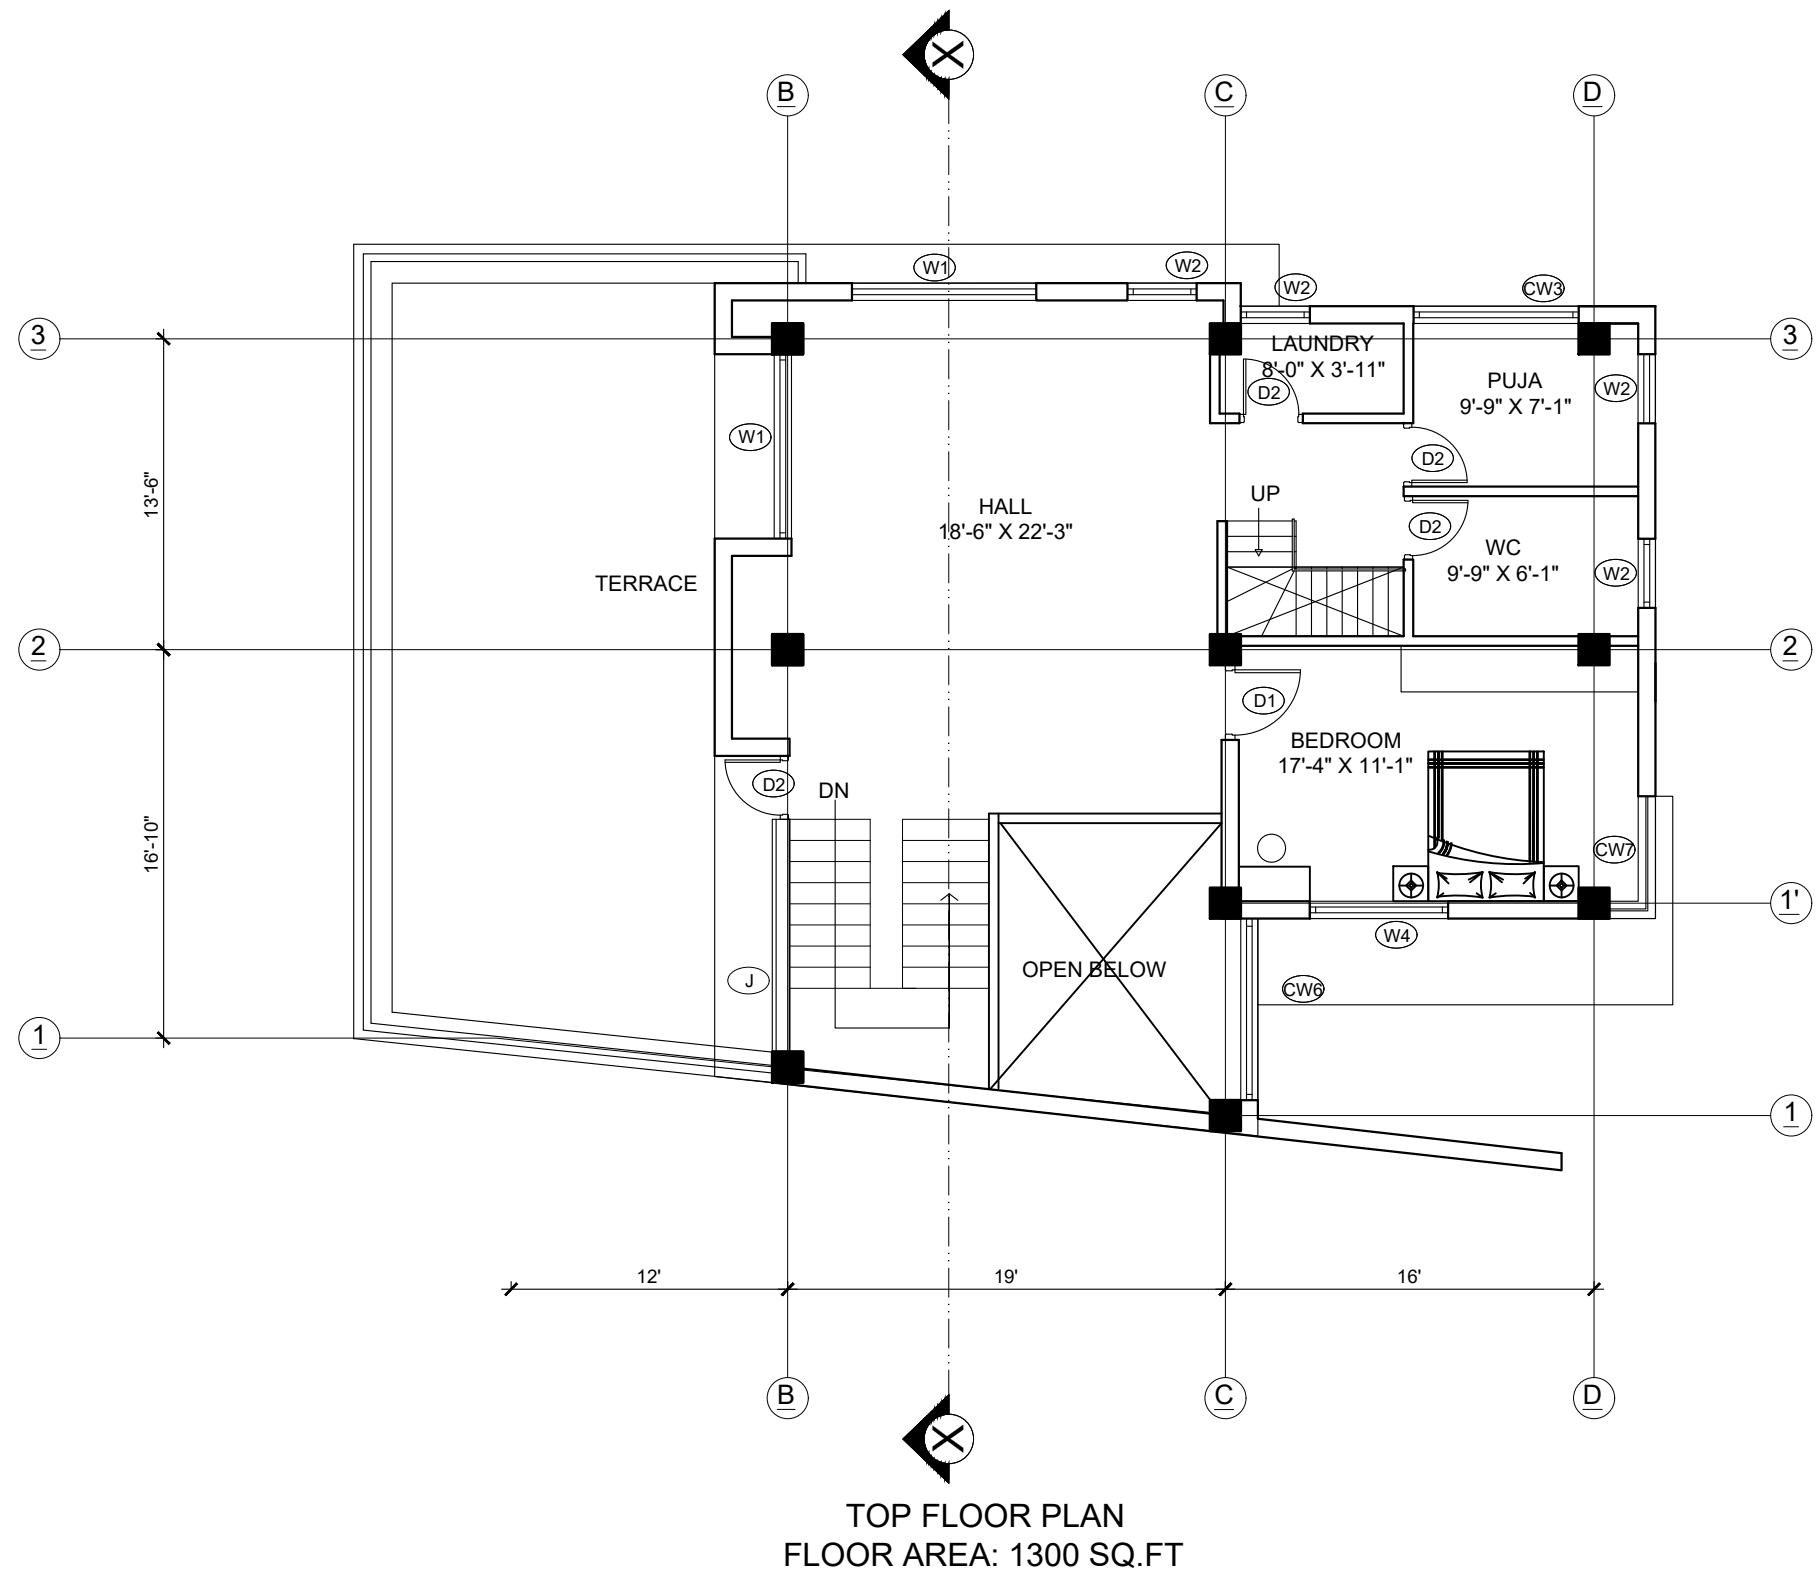

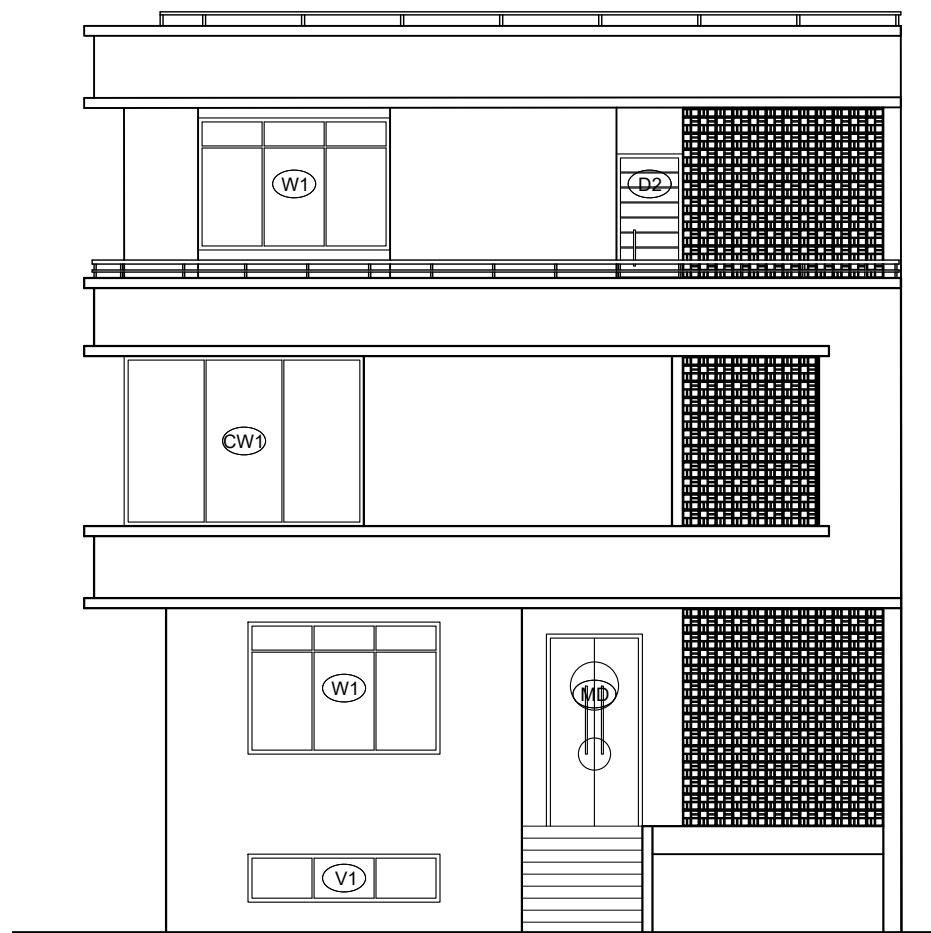


WEST ELEVATION

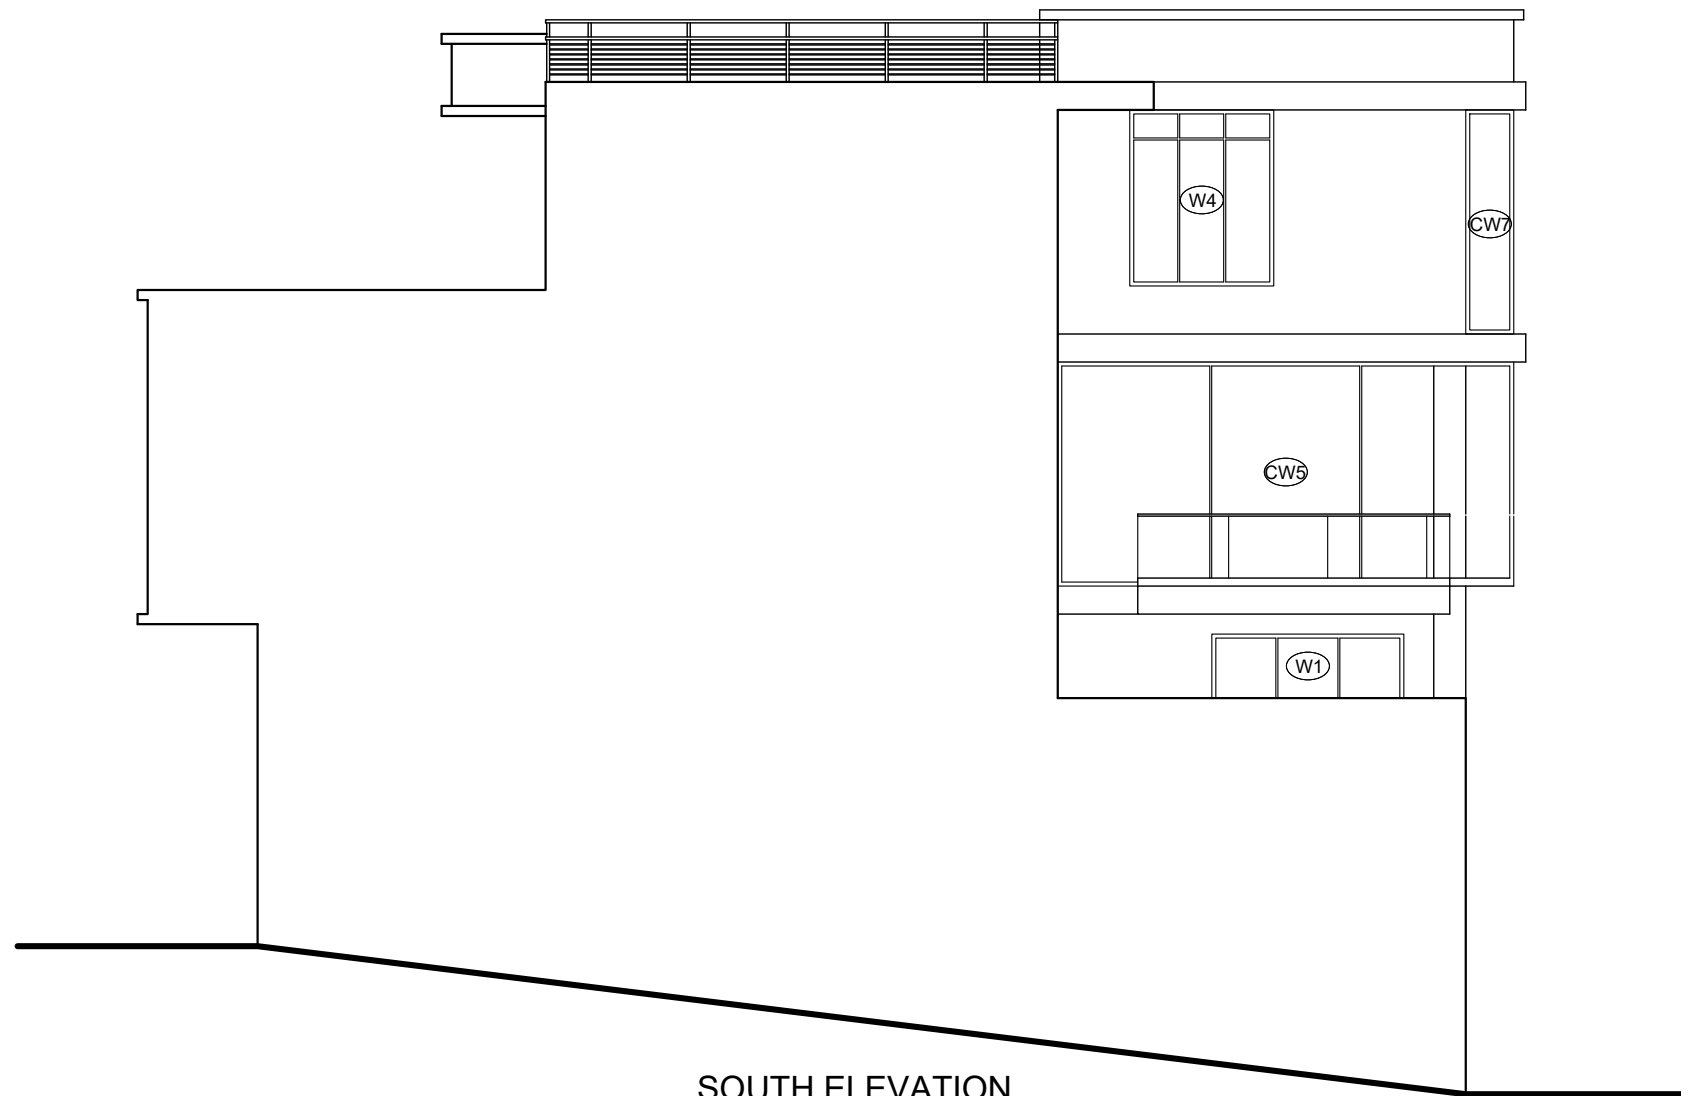


SOUTH ELEVATION



EAST ELEVATION

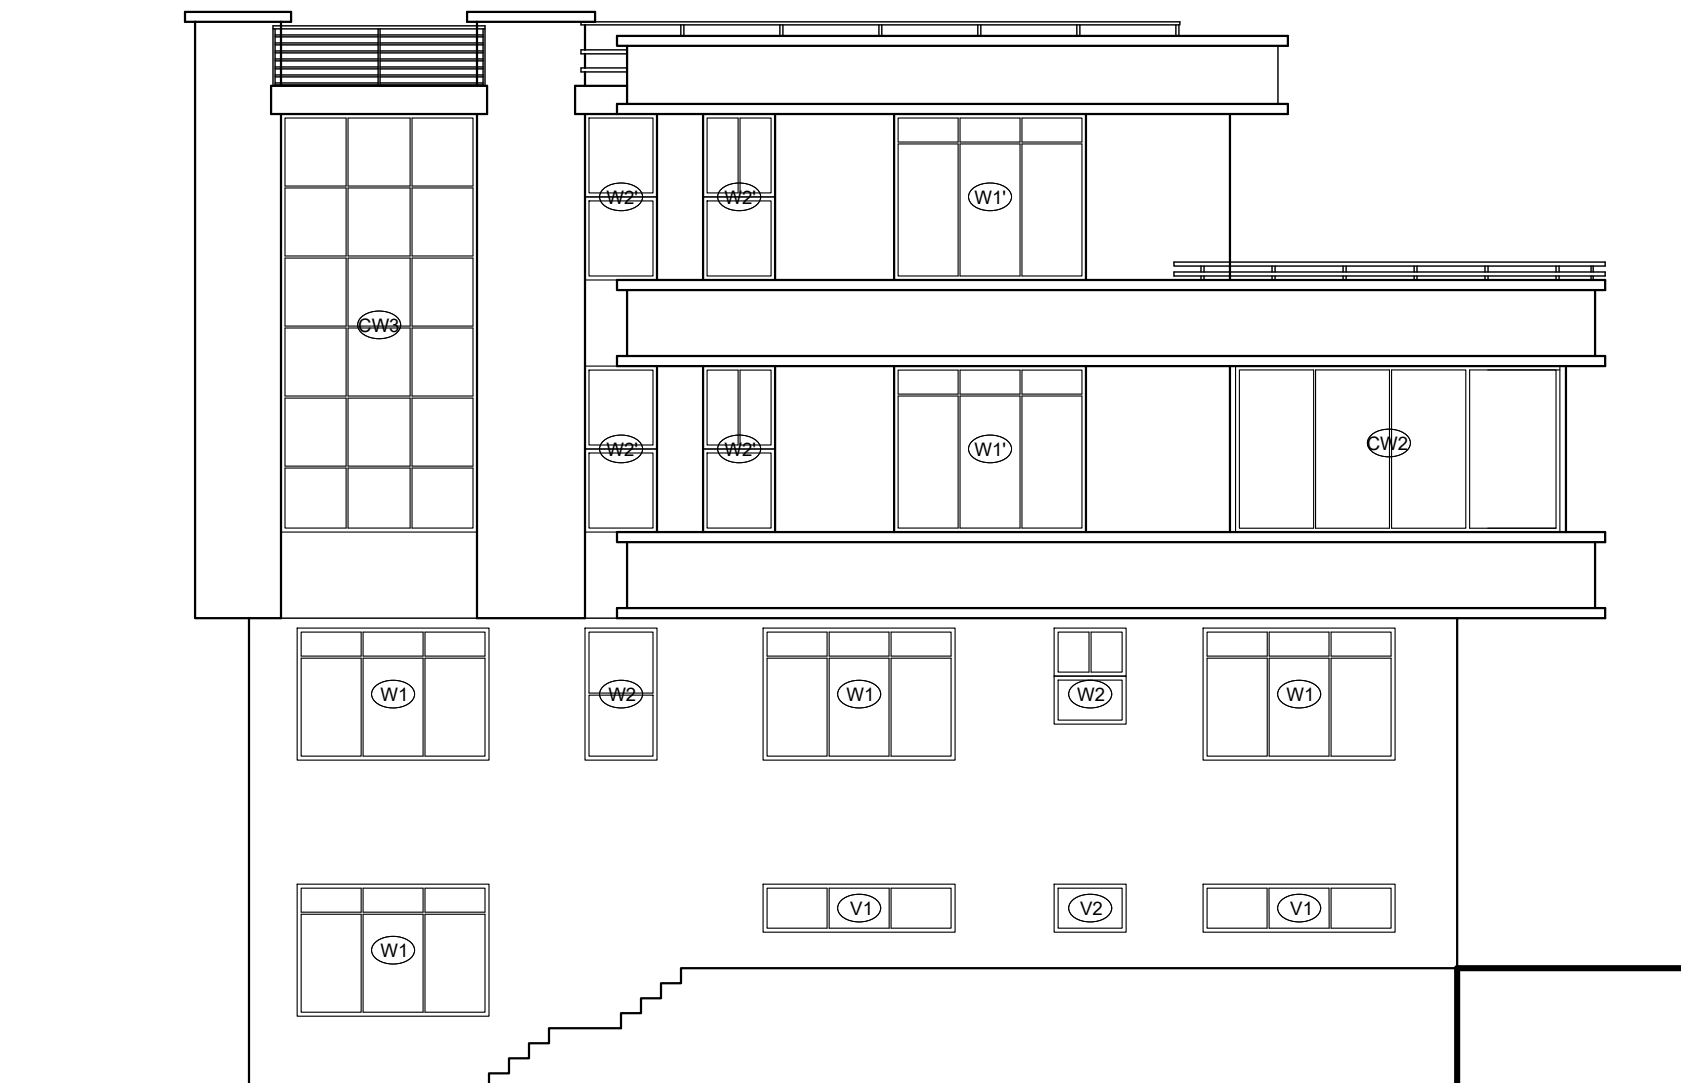


NORTH ELEVATION

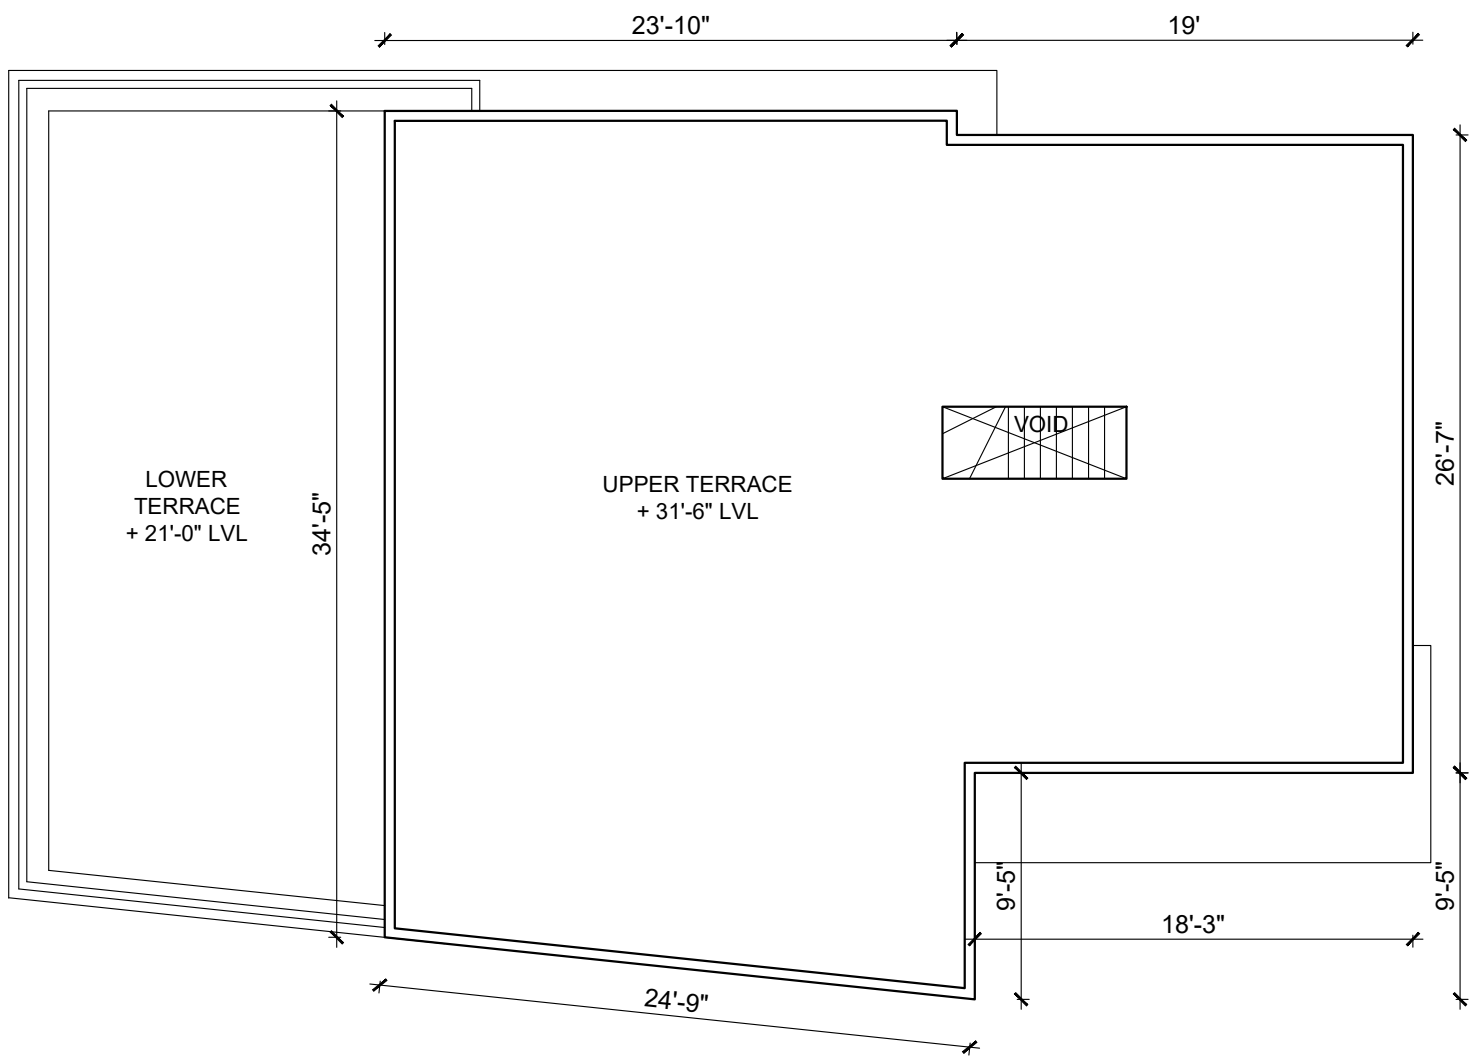

ROOF PLAN

OPENING SCHEDULE

S.N	DESCRIPTION	SIZE	NO.	SILL	LINTEL
1.	MD	4'-0" X 8'-0"	2	-	8'-0"
2.	MD'	4'-0" X 7'-0"	1	-	7'-0"
3.	D1	3'-3" X 7'-0"	7	-	7'-0"
4.	D2	2'-9" X 7'-0"	9	-	7'-0"
5.	D2'	2'-6" X 7'-0"	3	-	7'-0"
6.	W1	8'-0" X 5'-6"	10	3'-0"	8'-6"
7.	W1'	8'-0" X 6'-11"	2	2'-0"	8'-11"
8.	W2	3'-0" X 5'-6"	12	3'-0"	8'-6"
9.	W2'	3'-0" X 6'-11"	4	2'-0"	8'-11"
10.	W3	4'-0" X 5'-6"	1	3'-0"	8'-6"
11.	W4	6'-0" X 7'-4"	1	2'-0"	-
12.	V1	8'-0" X 2'-0"	3	6'-6"	8'-6"
13.	V2	3'-0" X 2'-0"	1	6'-6"	8'-6"
14.	J	10'-1" X 9'-1"	3	-	-
15.	CW	9'-6" X 19'-10"	1	-	-
16.	CW1	9'-8" X 7'-1"	1	2'-0"	-
17.	CW2	13'-8" X 7'-1"	1	2'-0"	-
18.	CW3	8'-2" X 17'-5"	1	2'-0"	-
19.	CW4	5'-6" X 9'-4"	1	-	-
20.	CW5	18'-5" X 9'-4"	1	-	-
21.	CW6	7'-11" X 9'-4"	1	-	-
22.	CW7	5'-0" X 9'-4"	1	-	-

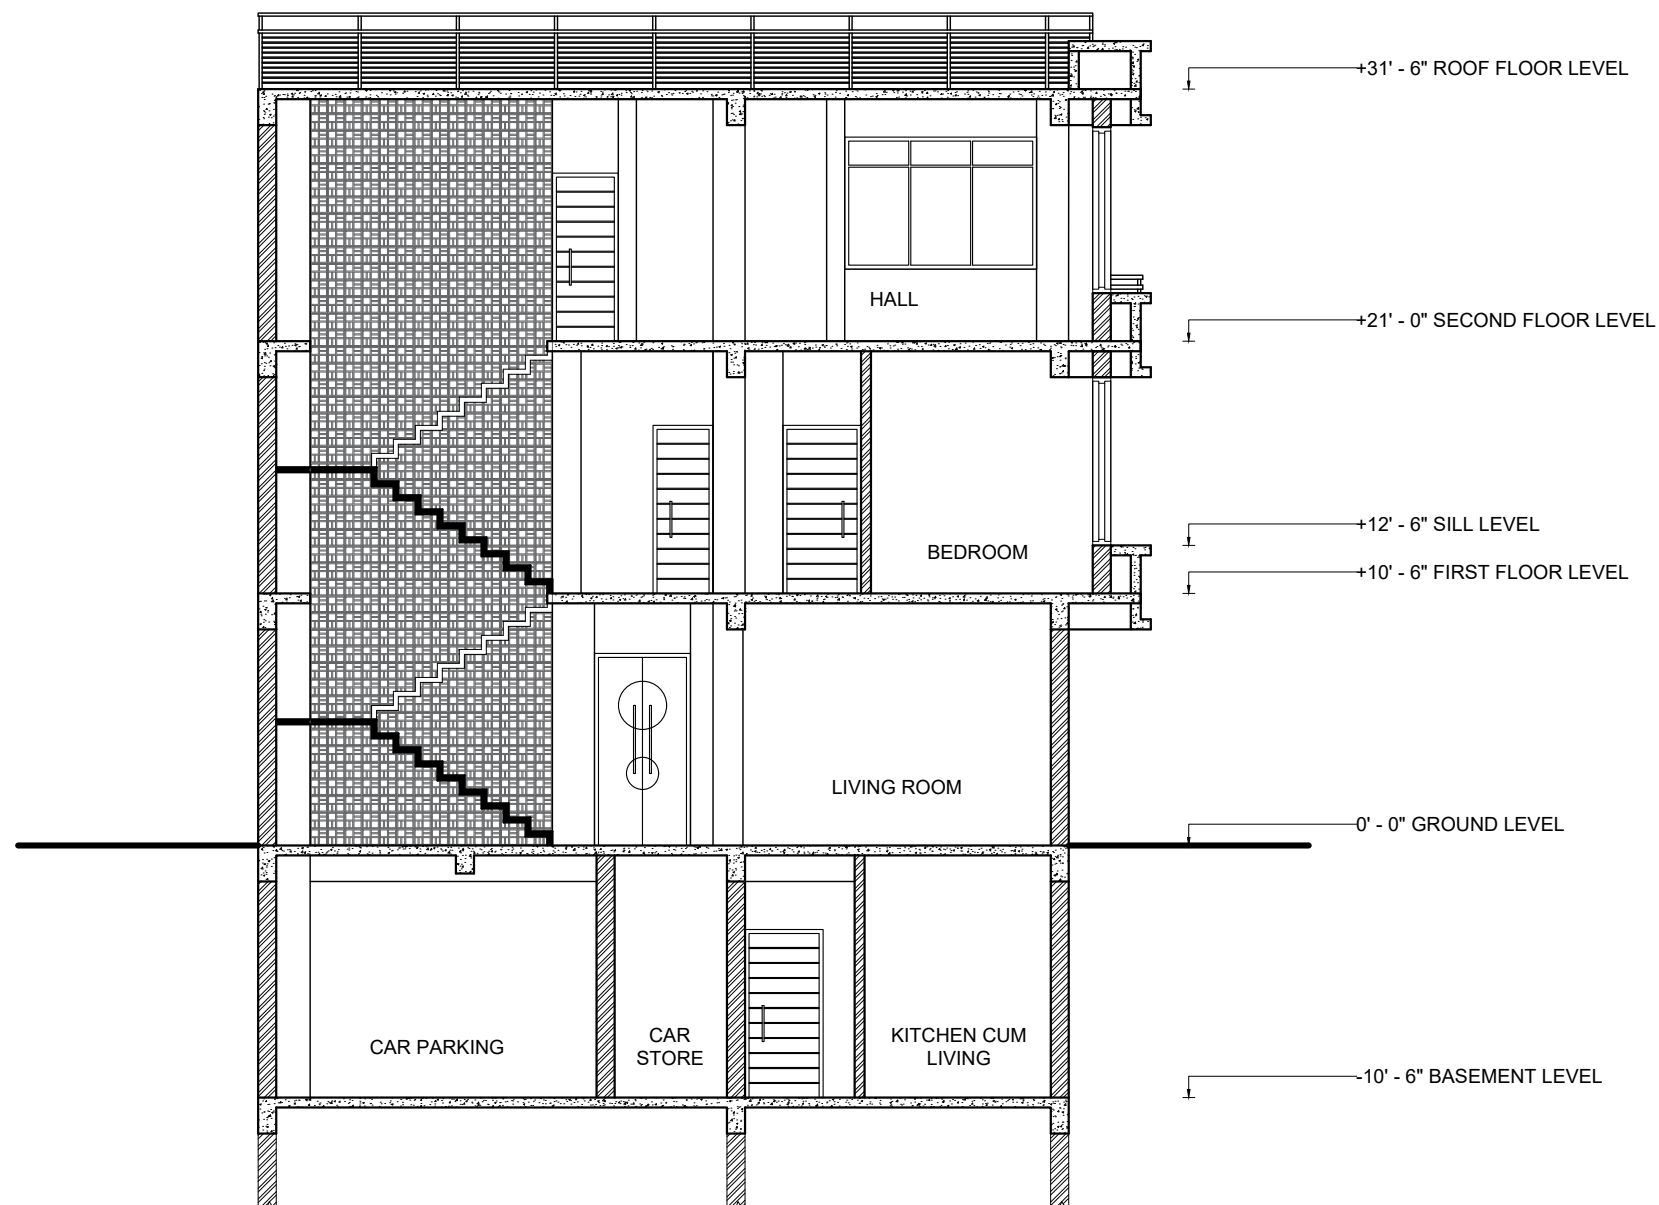

SECTION AT X-X

URBAN PARK PVT. LTD

BUDDHAGAR, KATHMANDU
urbanparknepal@gmail.com
www.urbanpark.com.np

RESIDENCE DESIGN

CLIENT: MR. MANDIP SUBEDI

SHEET: SECTION

ARCHITECT:

AR. APIL K.C.
AR. ANANTA GAUTAM

CIVIL
ENGINEER/
STRUCTURE:

ER. SUJAN ACHARYA

SCALE:

1:100

9