



OPENING SCHEDULE					
S.N	DESCRIPTION	SIZE	NO.	SILL	LINTEL
1.	D1	2'-9" X 7'-0"	10	-	7'-0"
2.	D1'	2'-9" X 5'-3"	1	-	-
3.	D2	3'-6" X 8'-2"	3	-	8'-2"
4.	D3	4'-0" X 8'-2"	1	-	8'-2"
5.	D4	3'-3" X 7'-0"	8	-	7'-0"
6.	SD	6'-0" X 8'-2"	2	-	8'-2"
7.	W1	2'-0" X 5'-8"	14	2'-6"	8'-2"
8.	W2	3'-0" X 4'-0"	9	3'-2"	8'-2"
9.	W3	2'-9" X 5'-8"	3	2'-6"	8'-2"
10.	W4	6'-0" X 5'-8"	6	2'-6"	8'-2"
11.	W5	8'-0" X 5'-8"	3	2'-6"	8'-2"

AREA TRIANGULATION


S.N	DESCRIPTION	AREA (SQ.FT.)
1.	A	717
2.	B	812
3.	C	375
TOTAL		1904 SQ.FT.

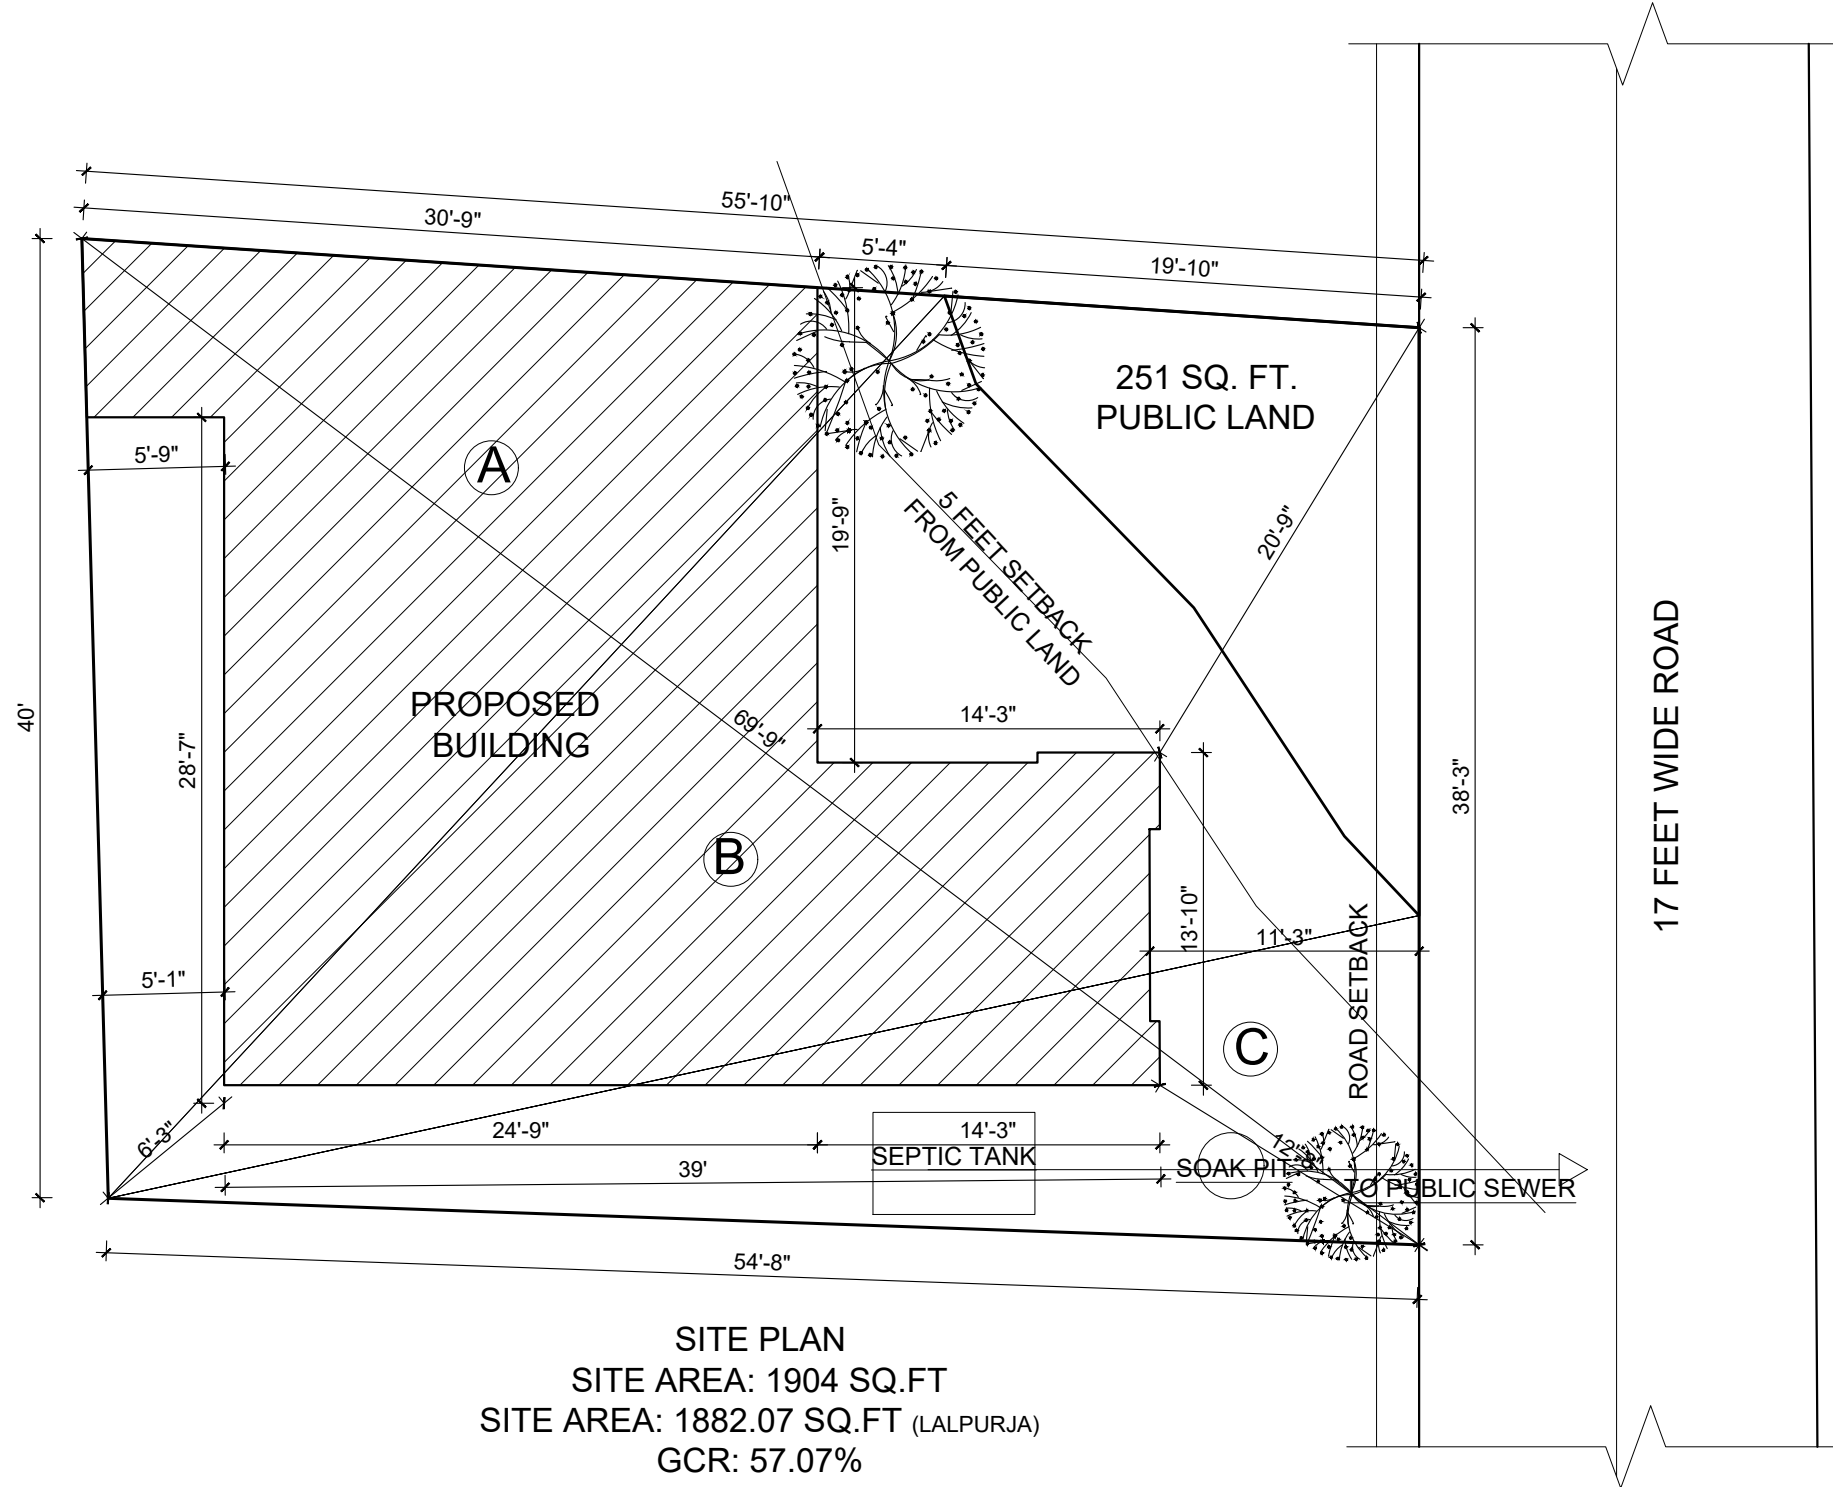


SITE PLAN
SITE AREA: 1904 SQ.FT
SITE AREA: 1882.07 SQ.FT (LALPURJA)
GCR: 57.07%
FAR: 1.59

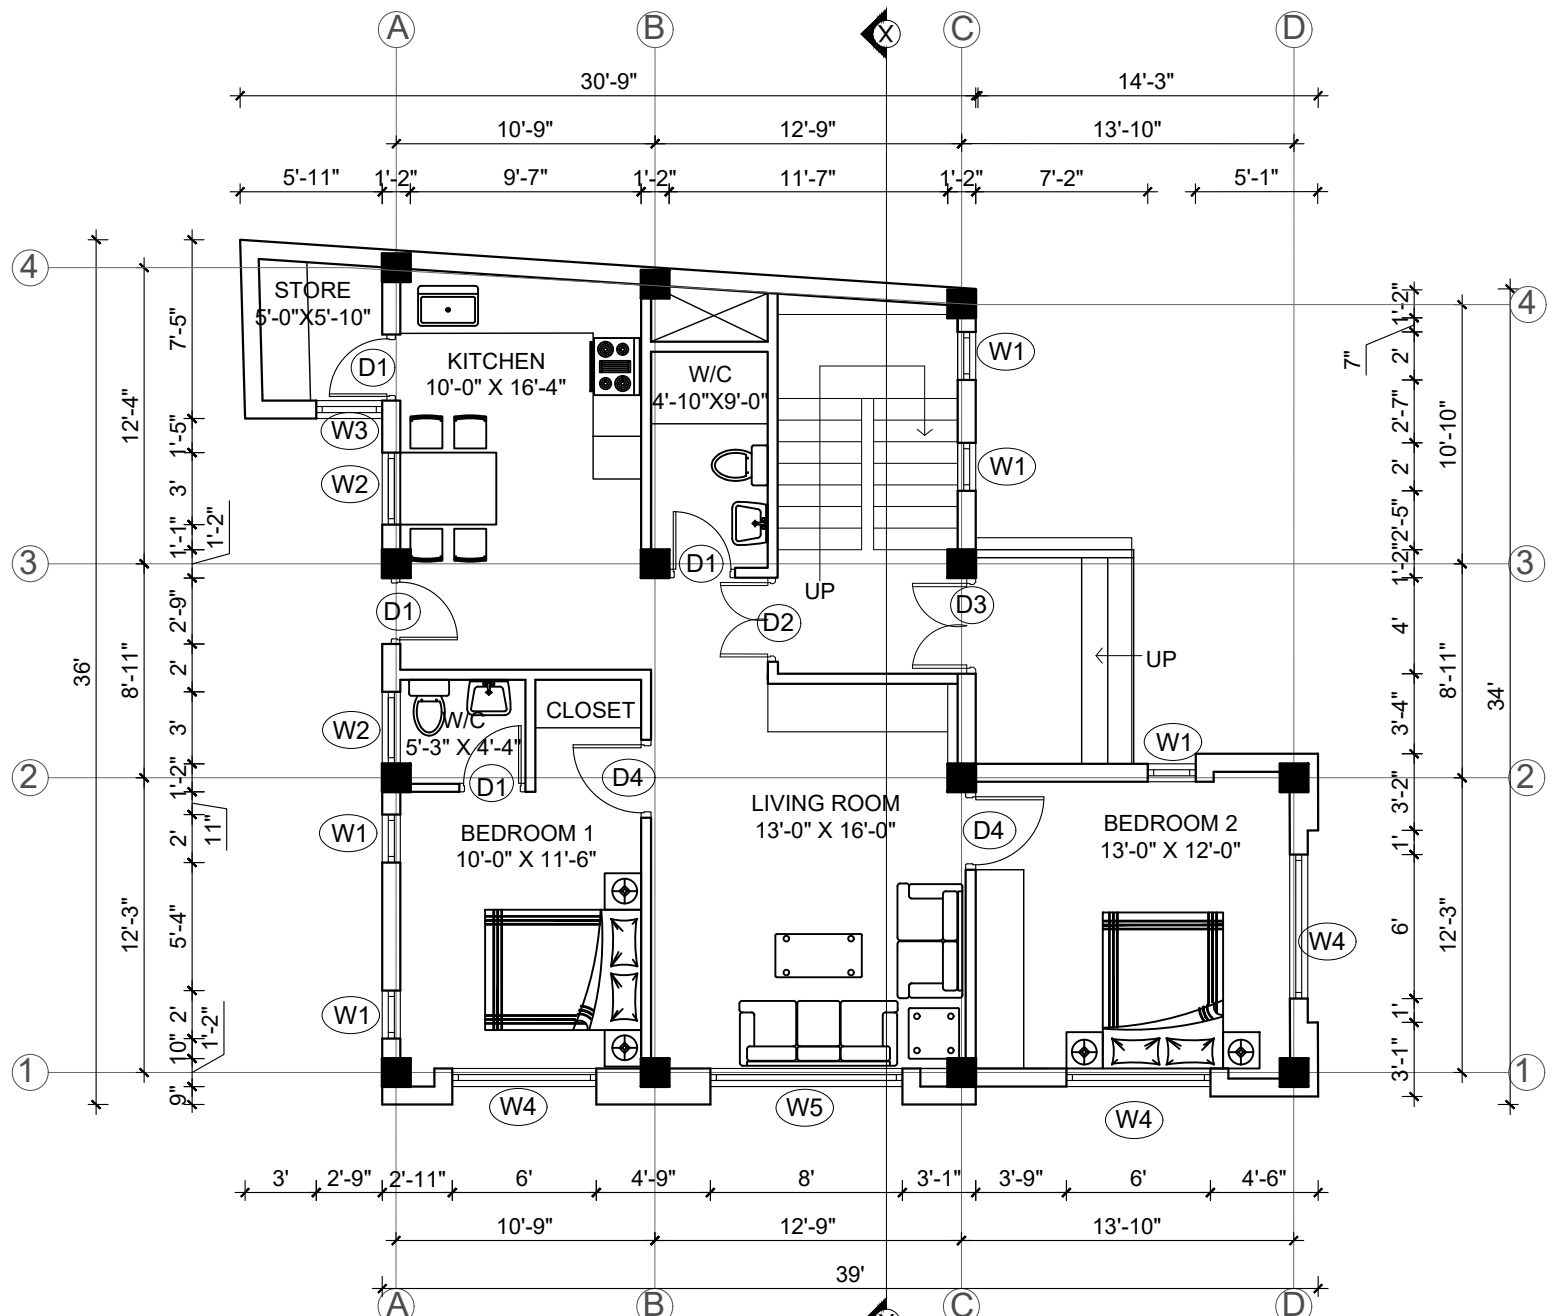


GROUND FLOOR PLAN
FLOOR AREA: 1085.42 SQ.FT

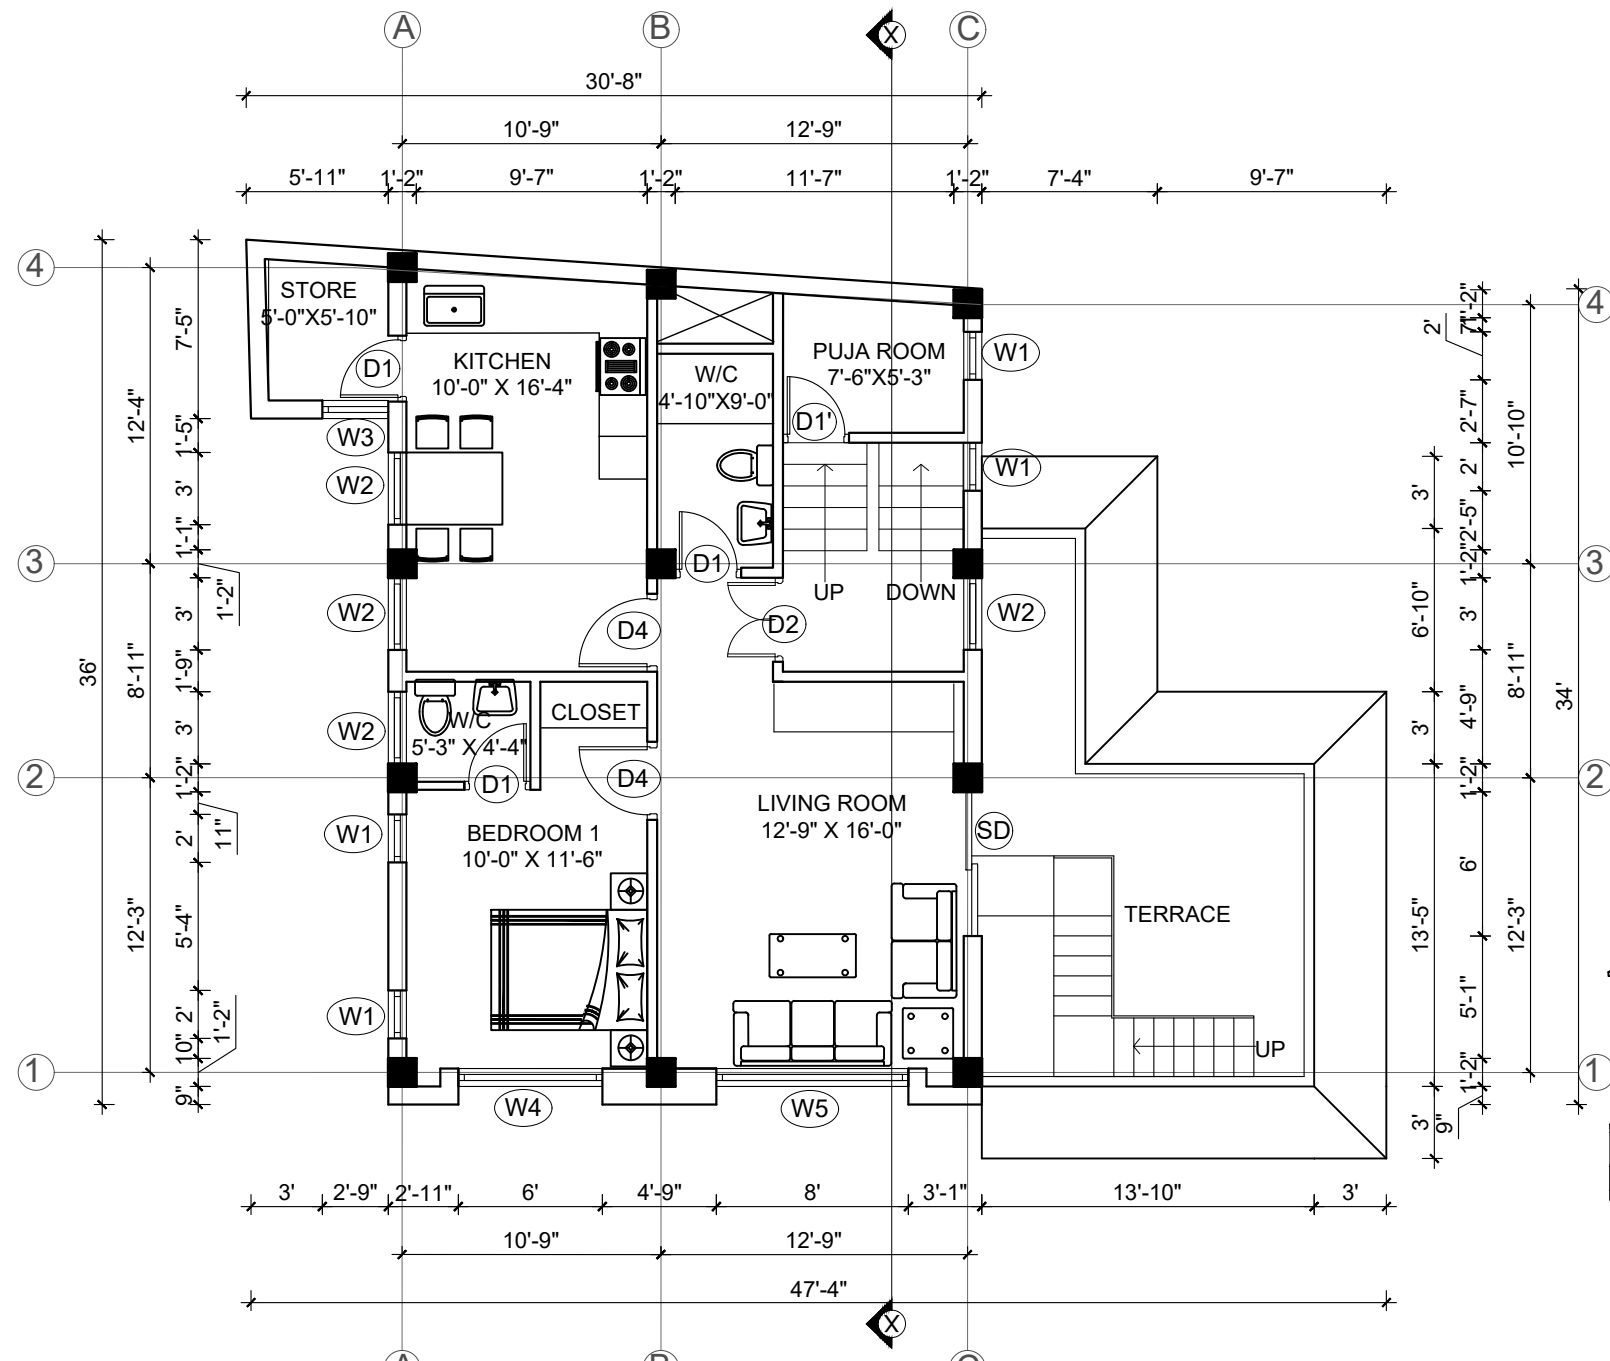


TOP FLOOR PLAN
FLOOR AREA: 884.14 SQ.FT

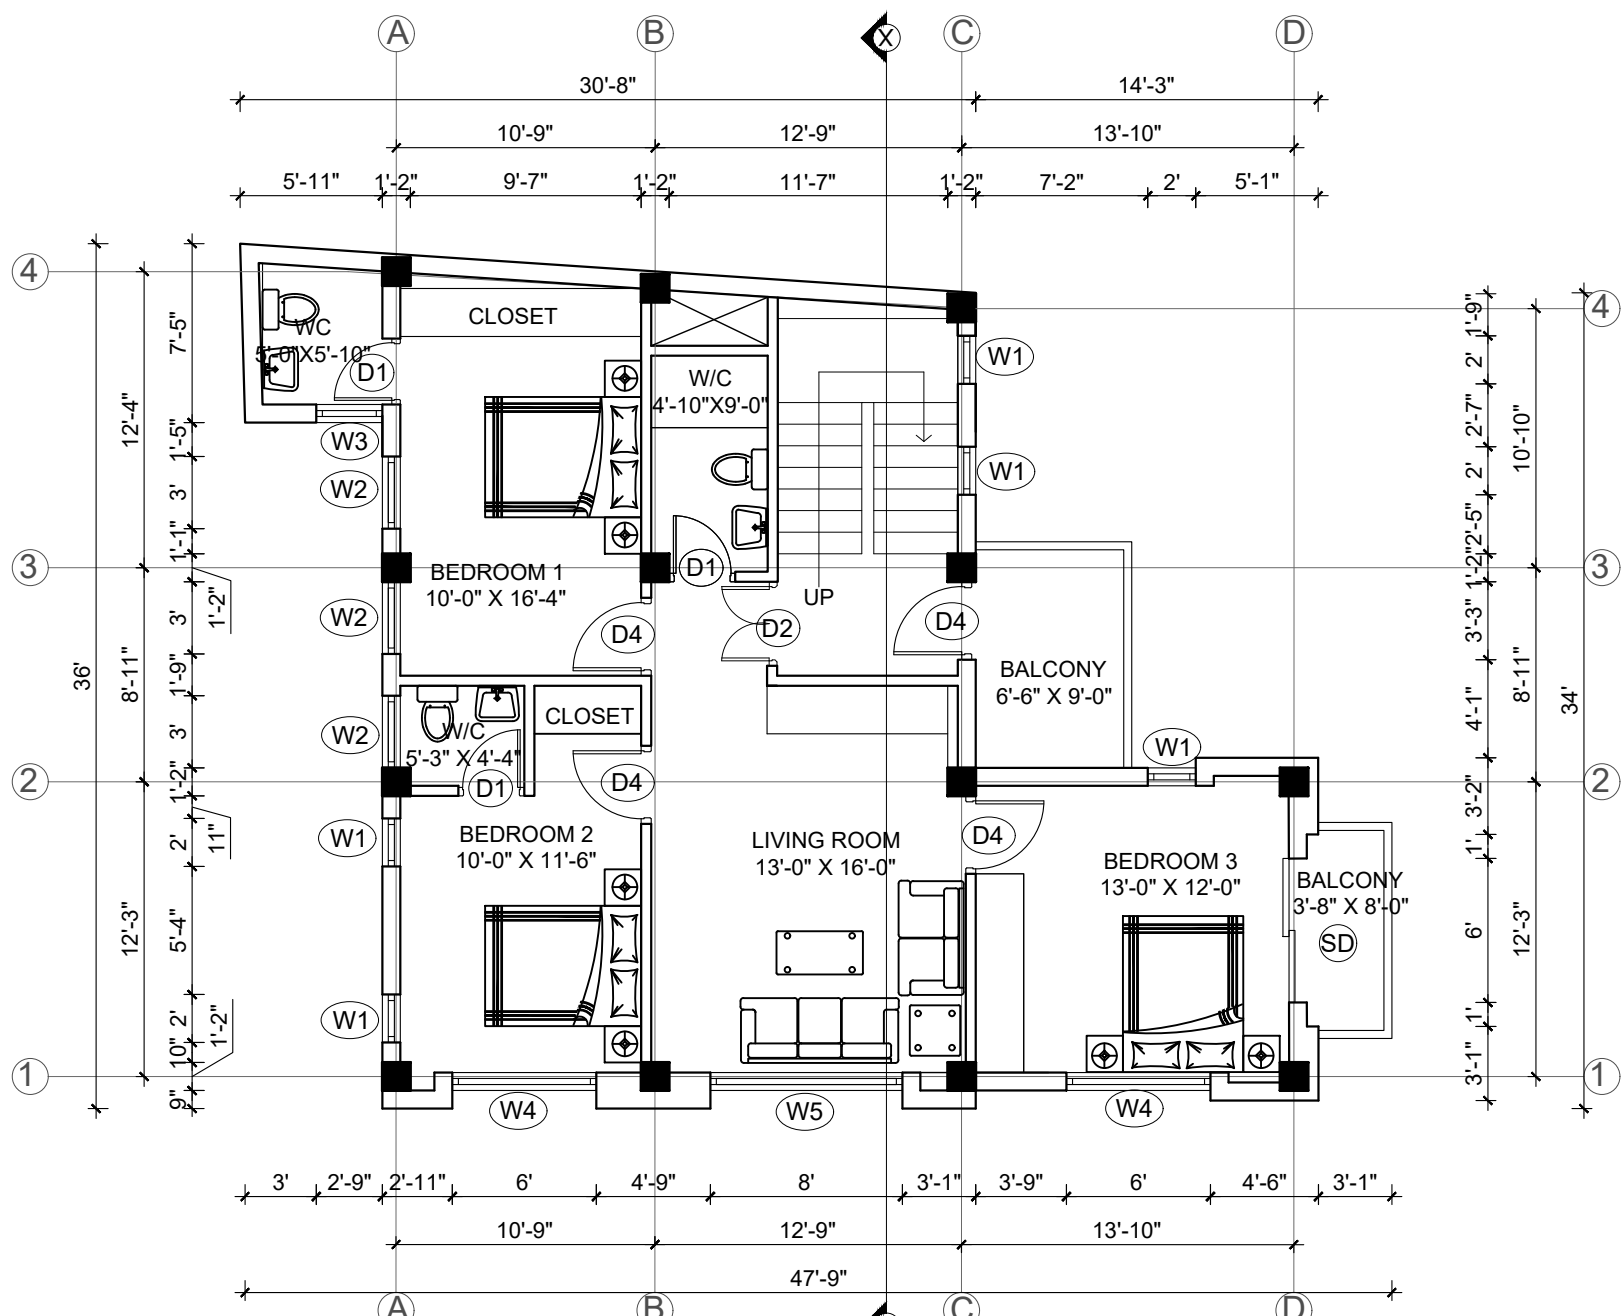


FIRST FLOOR PLAN
FLOOR AREA: 1085.42 SQ.FT

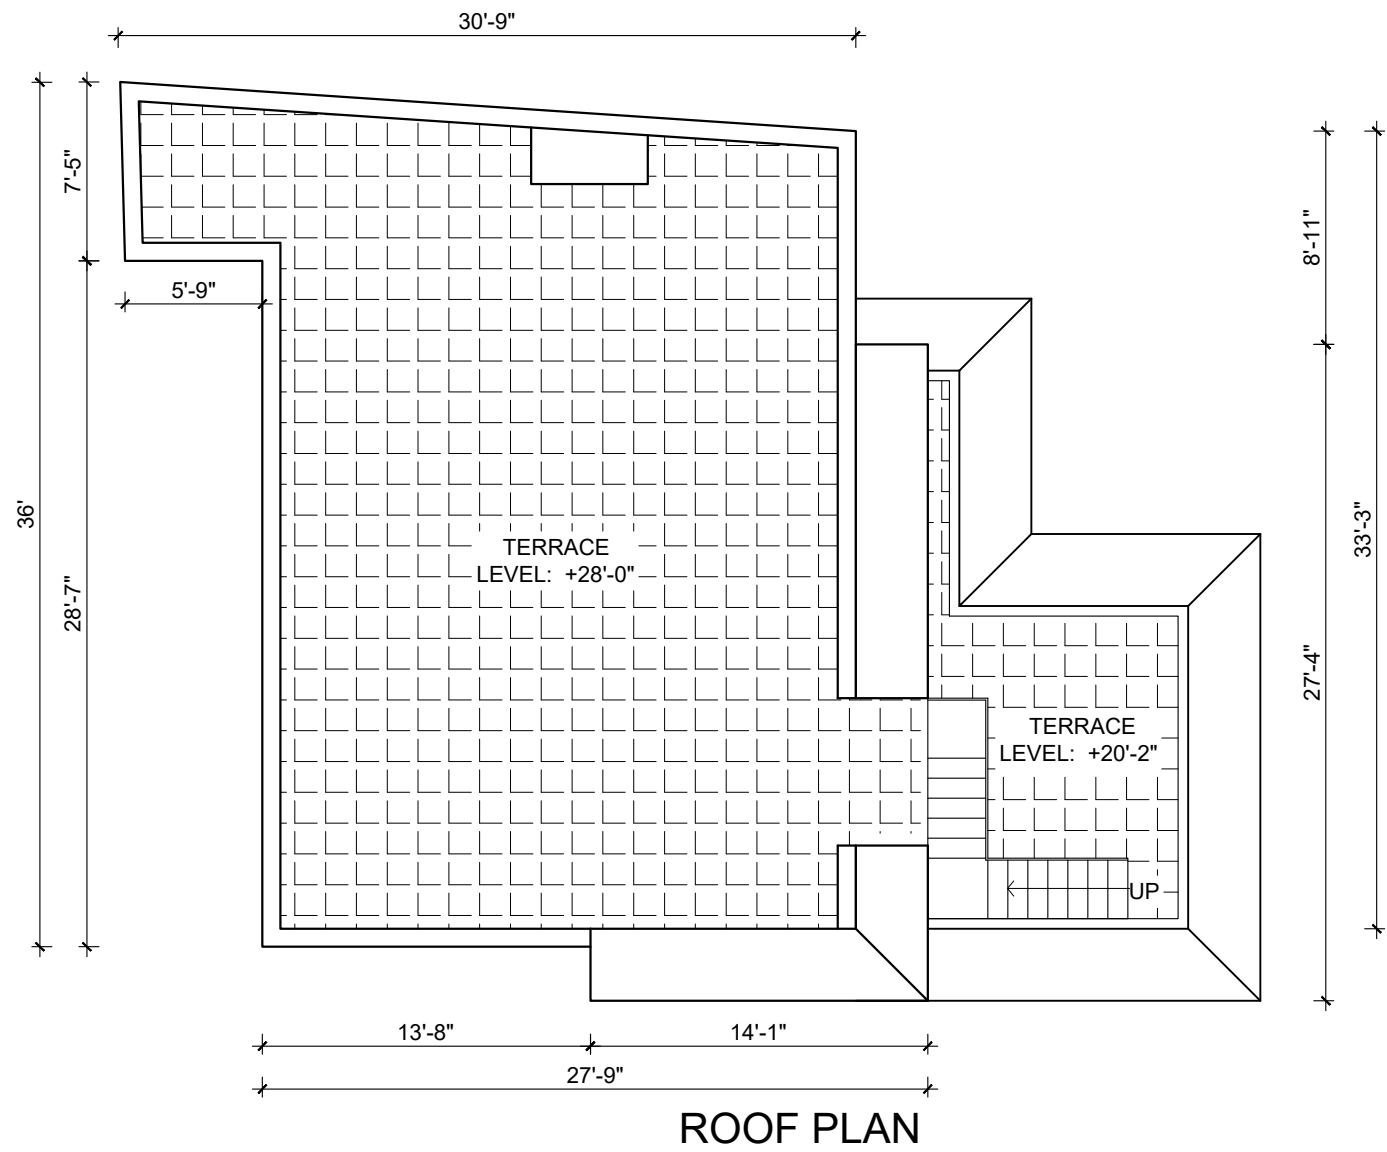


ROOF PLAN

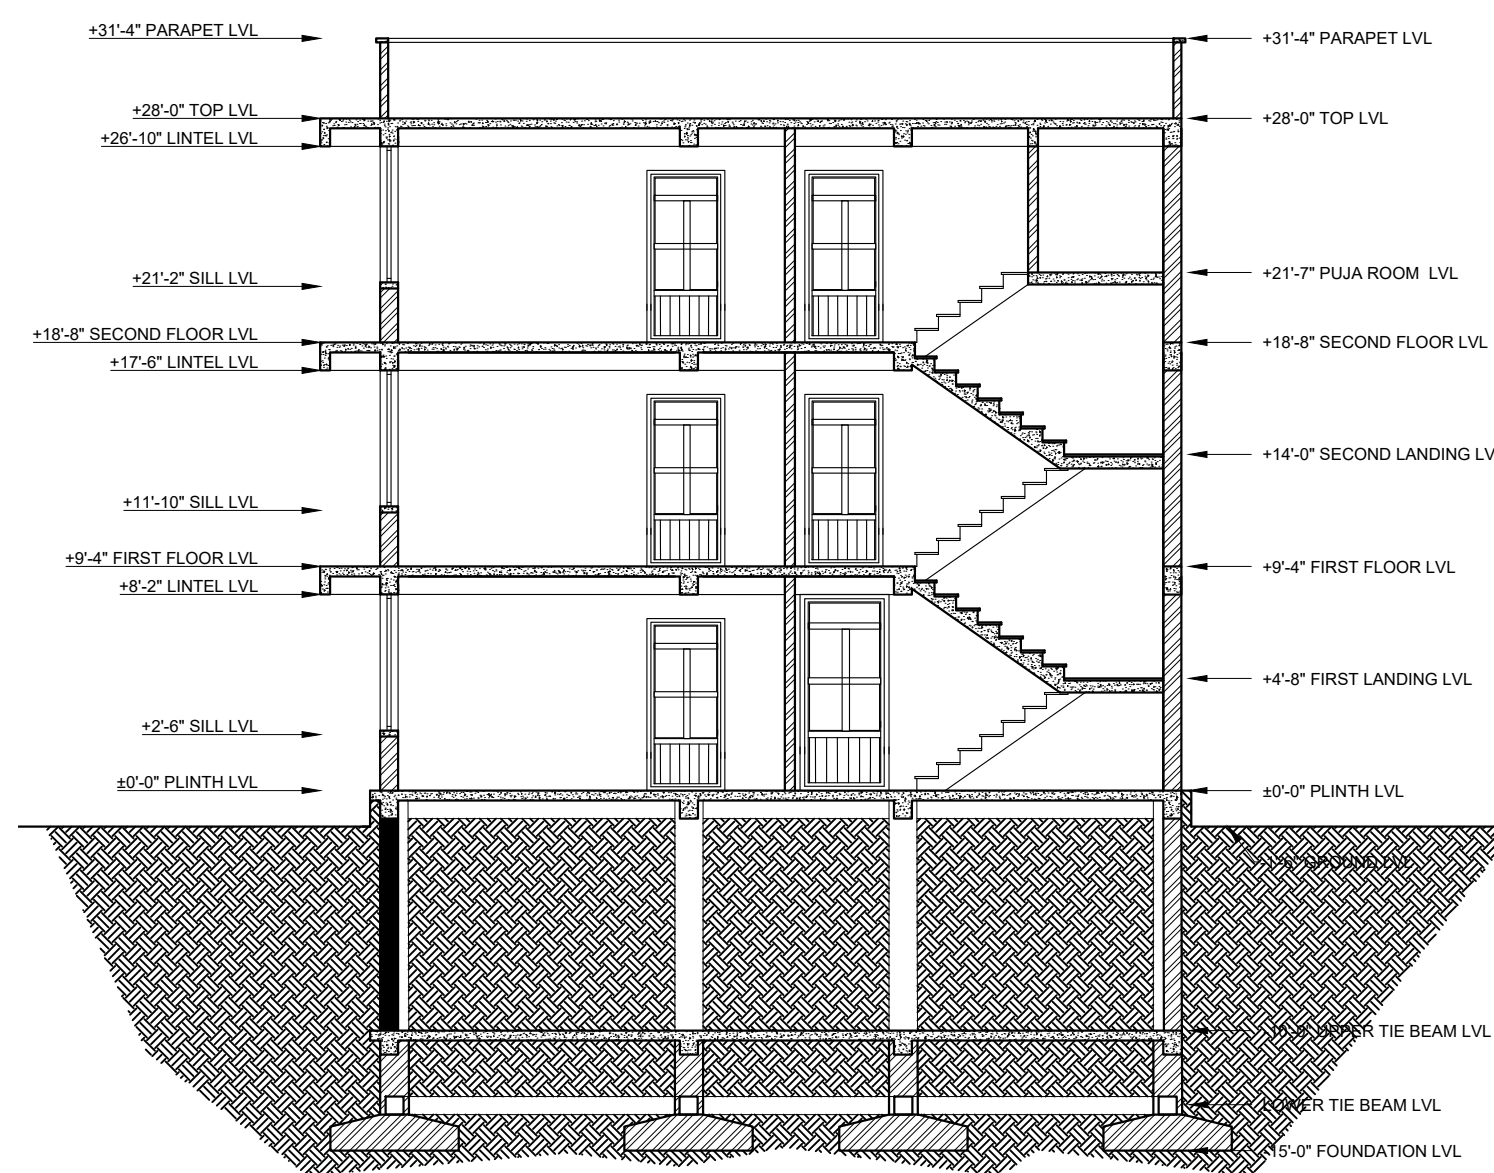

SECTION AT X-X

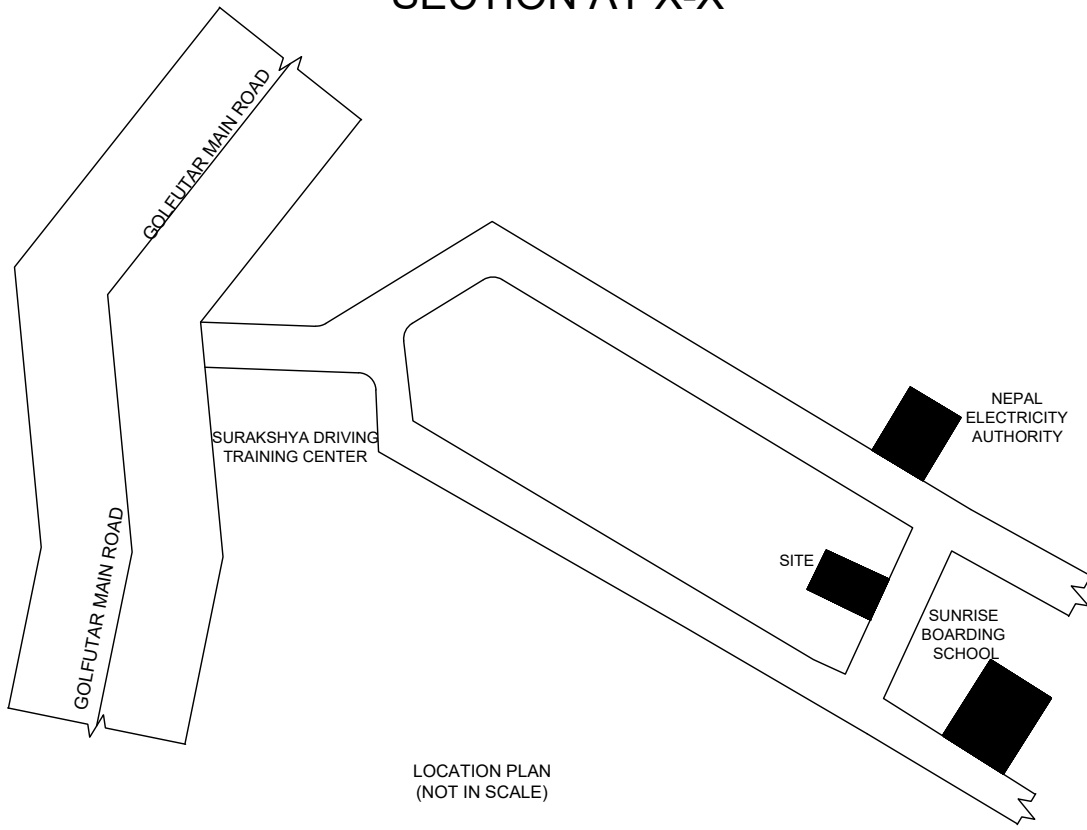

LOCATION PLAN
(NOT IN SCALE)

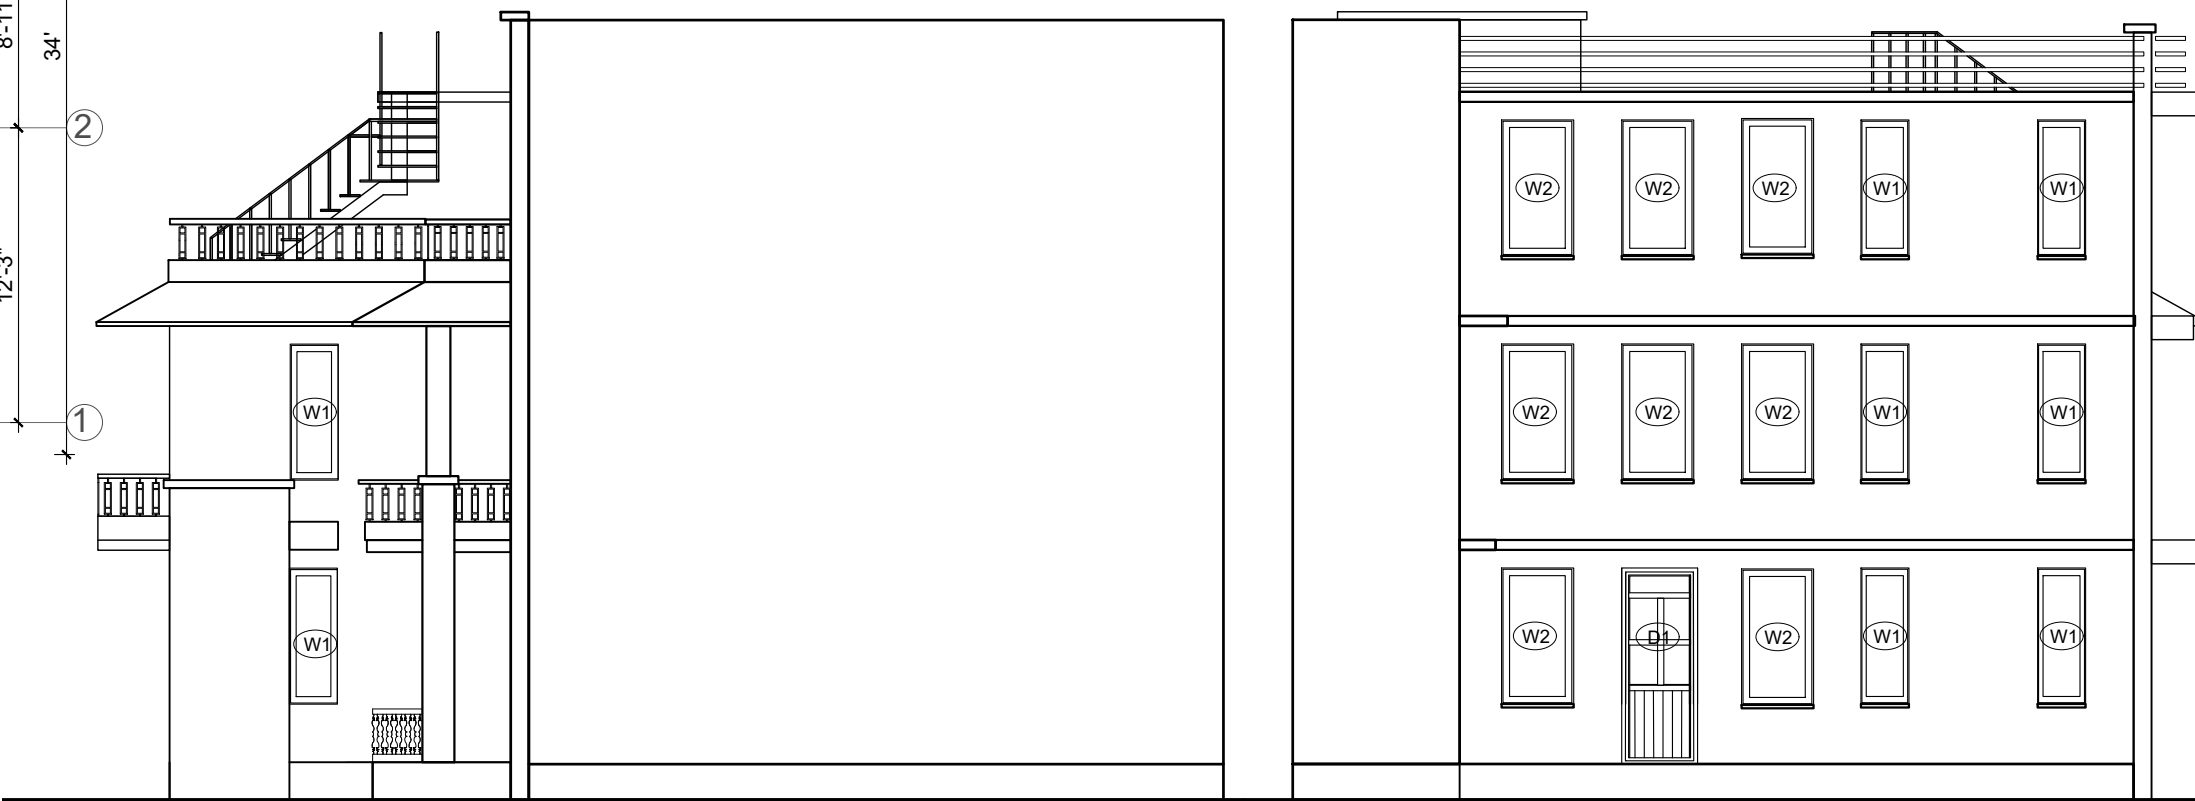


NORTH ELEVATION

WEST ELEVATION



SOUTH ELEVATION

EAST ELEVATION

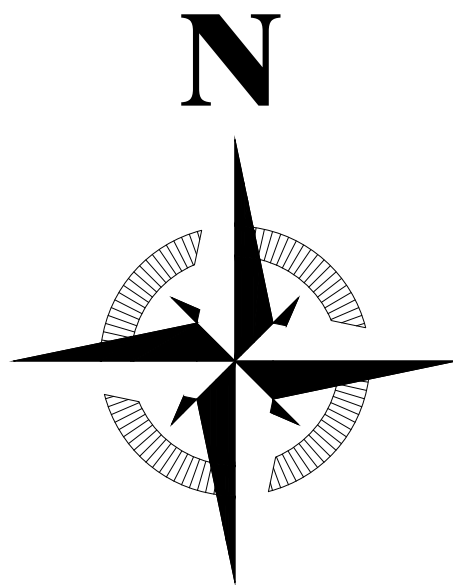

REVISIONS

REV.	DESCRIPTION	DATE
A		






URBAN PARK PVT. LTD.
KATHMANDU, NEPAL
urbanparknepal@gmail.com

OWNER: Mr. DHAN KUMARI KHATRI	
SIGNATURE:	
BUILDING TYPE: RESIDENTIAL	LOCATION: BUDHANILKANTHA, WARD NO. 3
PLOT NO: 125	AREA: 176.96 SQ.M. (0-5-2-1.05) 174.85 SQ.M. (0-5-2-0) ACCORDING TO LALPURJA
DETAILS: ARCHITECTURAL DRAWINGS	
ARCHITECT: AR. APIL K. C.	
DATE: SEP 2021	SCALE: 1"=8'-0" (1:96)
SIGNATURE :	
NEC REGISTRATION NO. 1070 "A"	
REMARKS:	

1. DO NOT SCALE FROM THE DRAWINGS
2. STRUCTURAL DRAWINGS SHALL BE READ IN CONJUNCTION WITH RELEVANT ARCHITECTURAL DRAWINGS AND IN ANY CONFLICT REFER ARCHITECTURAL DRAWINGS FOR DIMENSIONS.
3. UNLESS SPECIFIED OTHERWISE, ALL LEVELS SHOWN IN STRUCTURAL DRAWINGS ARE STRUCTURAL LEVELS ONLY.
4. DO NOT SCALE FOLLOW WRITTEN DIMENSION ONLY
5. ALL DIMENSION & LEVEL ARE IN FEET-INCHES UNLESS NOTED OTHERWISE. ALL DIMENSION TO BE VERIFIED ON SITE & APPROVED BY THE ENGINEER
6. GRADE OF CONCRETE MIX SHALL BE M-25 FOR COLUMN, M-20 FOR FOOTING, BEAMS, SLABS ETC. UNLESS NOTED OTHERWISE CONFORMING TO IS:456-2000.
7. REINFORCEMENT SHALL BE HIGH YIELD STRENGTH DEFORMED BARS OF GRADE Fe:500 CONFORMING TO IS: 1786-1985.
8. CLEAR COVER TO BARS
 - a. FOR CONCRETE MEMBERS IN CONTACT WITH SOIL = 50mm
 - b. FOR LONGITUDINAL (VERTICAL) BARS IN COLUMN = 40mm
 - c. FOR MAIN BARS IN BEAMS = 25mm
 - d. FOR OUTER BARS IN SLAB = 20mm
9. BARS IN COLUMNS SHALL BE SPLICED ONLY AT MID HEIGHT OF COLUMN.
10. BARS SPLICING IN BEAM SHALL BE AVOIDED IN THE SPAN WHERE INTERMEDIATE BEAM IS CONNECTED AND SHALL BE ONLY AS SHOWN ON DWG.
11. DEVELOPMENT / LAP LENGTH (L_d) FOR BARS.














BAR DIA-(mm)	8	10	12	16	20	25	28	32
FOR M20 Ld	1'-9"	2'-3"	2'-8"	3'-6"	4'-5"	5'-7"	6'-2"	7'-0"
FOR M25 Ld	1'-7"	2'-0"	2'-4"	3'-1"	3'-10"	4'-10"	5'-5"	6'-2"

18. ANY DISCREPANCY NOTED BETWEEN DETAILS IN THE DRAWINGS/SPECIFICATIONS, THE MATTER SHALL BE BROUGHT TO THE NOTICE OF CONCERNED ENGINEER PRIOR TO CONSTRUCTION AND GOT RECONCILED BEFORE EXECUTION.

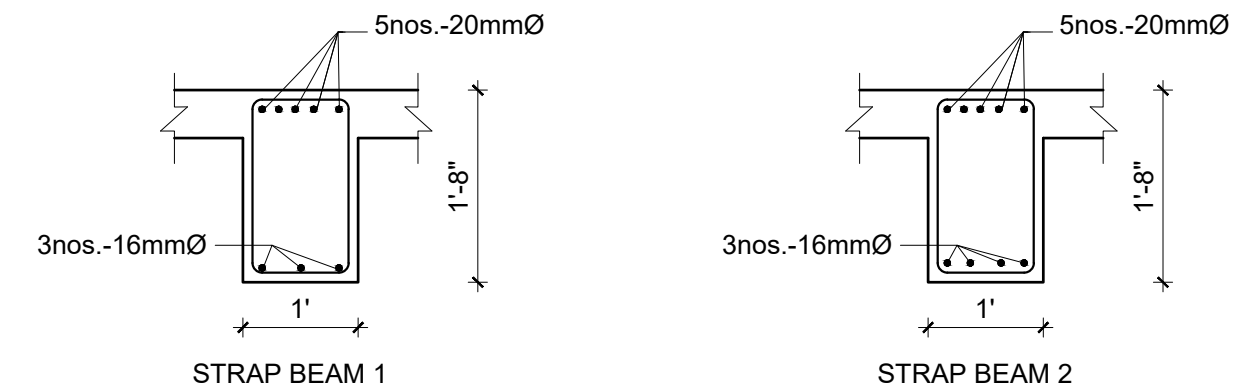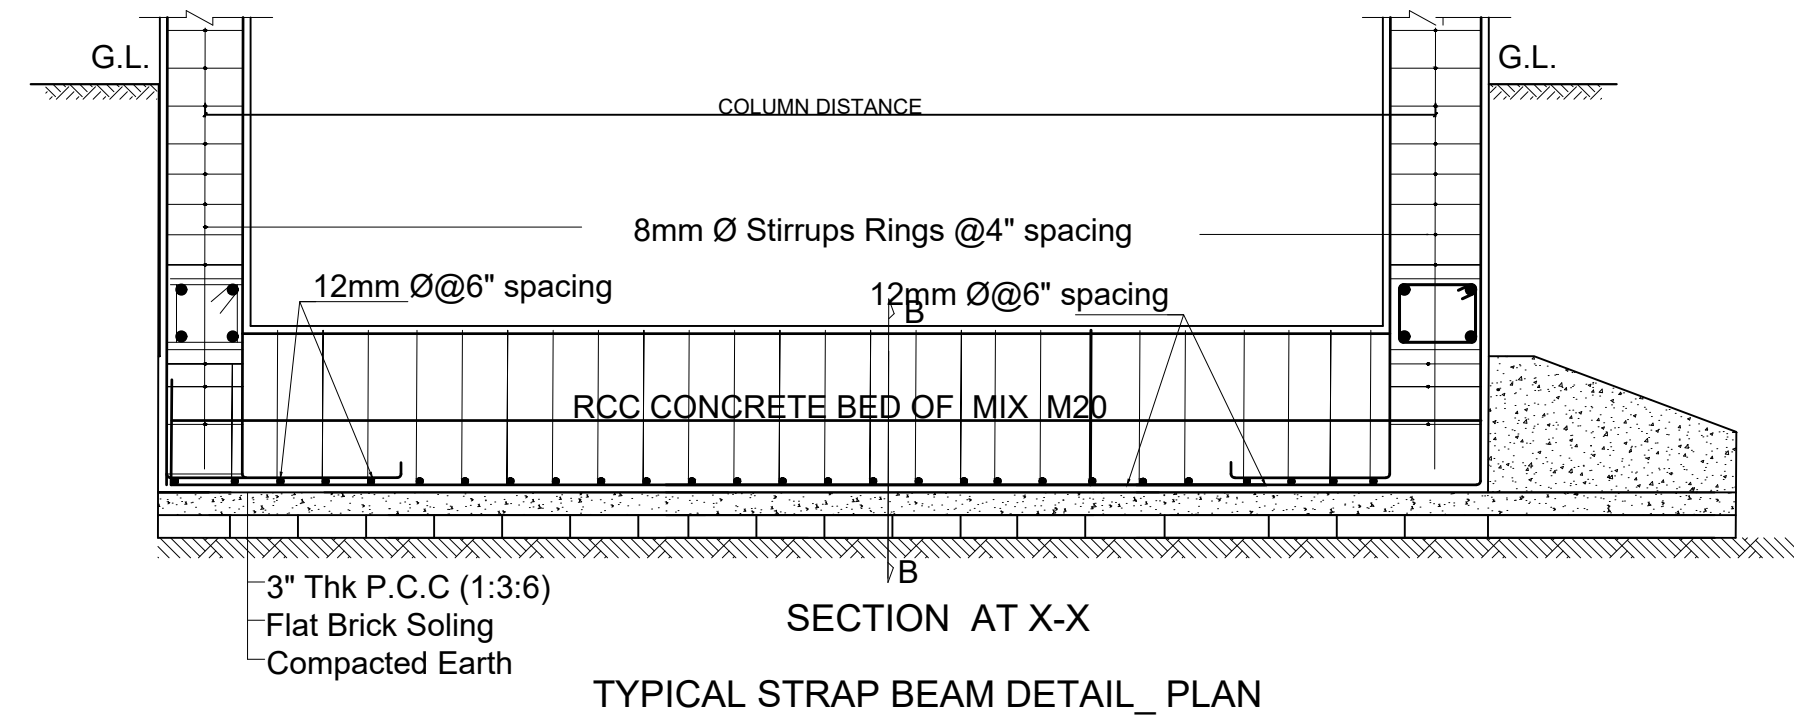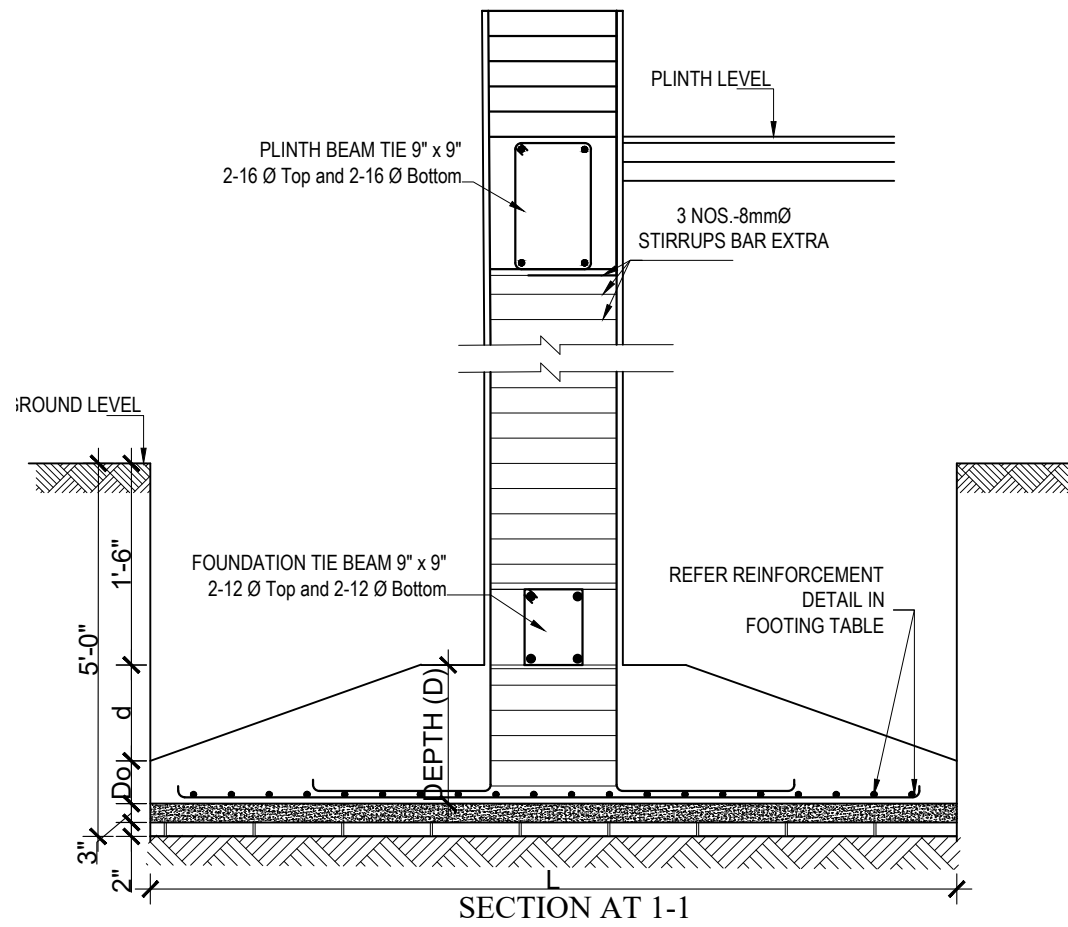

S. No.	Footing	Footing Size			Reinforcement		Remarks
		Size		thickness[mm]	along X-direction	along Y-direction	
		Length	Breadth				
1.	F1	5'-0"	5'-0"	18"	12mmØ@6" C/C	12mmØ@6" C/C	Isolated Footing
2.	F2	5'-6"	5'-6"	18"	12mmØ@6" C/C	12mmØ@6" C/C	Isolated Footing
3.	F3	6'-2"	6'-2"	18"	12mmØ@6" C/C	12mmØ@6" C/C	Isolated Footing

S. No.	GRID	Footing Size				Strap Beam Width	Strap Beam Depth	Rebar Detail
		Length L1	Breadth(m) B1	Length(m) L2	Breadth(m) B2			
1.	GRID A (4-3)	5'-0"	5'-6"	6'-6"	5'-6"	12"	20"	5-20mm reinforcement@top and 3-16mm reinforcement@bottom
2.	GRID B (4-3)	5'-0"	6'-8"	7'-8"	6'-8"	12"	22"	5-20mm reinforcement@top and 4-16mm reinforcement@bottom
3.	GRID C (4-3)	5'-0"	6'-8"	7'-8"	6'-8"	12"	22"	5-20mm reinforcement@top and 4-16mm reinforcement@bottom

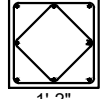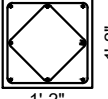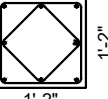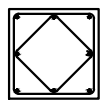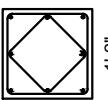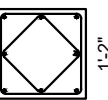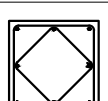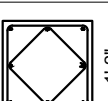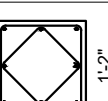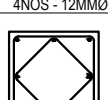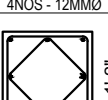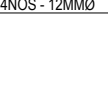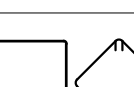COLUMN REINFORCEMENT DETAILS					
S. NO.	DESCRIPTION	COLUMN C1 (14' x 14')	COLUMN C2 (14' x 14')	COLUMN C3 (14' x 14')	STIRRUPS
1	-10'-0" LIV.	 4NGS - 10MM 4NGS - 12MM	 4NGS - 10MM 4NGS - 10MM	 4NGS - 10MM 4NGS - 12MM	 8@10mmx1 & 150mmx1
2	GROUND FLOOR	 4NGS - 10MM 4NGS - 12MM	 4NGS - 10MM 4NGS - 12MM	 4NGS - 10MM 4NGS - 12MM	 8@10mmx1 & 150mmx1
1	FIRST FLOOR	 4NGS - 10MM 4NGS - 12MM	 4NGS - 10MM 4NGS - 12MM	 4NGS - 10MM 4NGS - 12MM	 8@10mmx1 & 150mmx1
1	TOP FLOOR	 4NGS - 10MM 4NGS - 12MM	 4NGS - 10MM 4NGS - 12MM	 4NGS - 10MM 4NGS - 12MM	 8@10mmx1 & 150mmx1


REV.	DESCRIPTION	DATE
A		




URBAN PARK PVT. LTD.
KATHMANDU, NEPAL
urbanparknepal@gmail.com

NEC REGISTRATION NO.
1070 "A"


REMARKS:

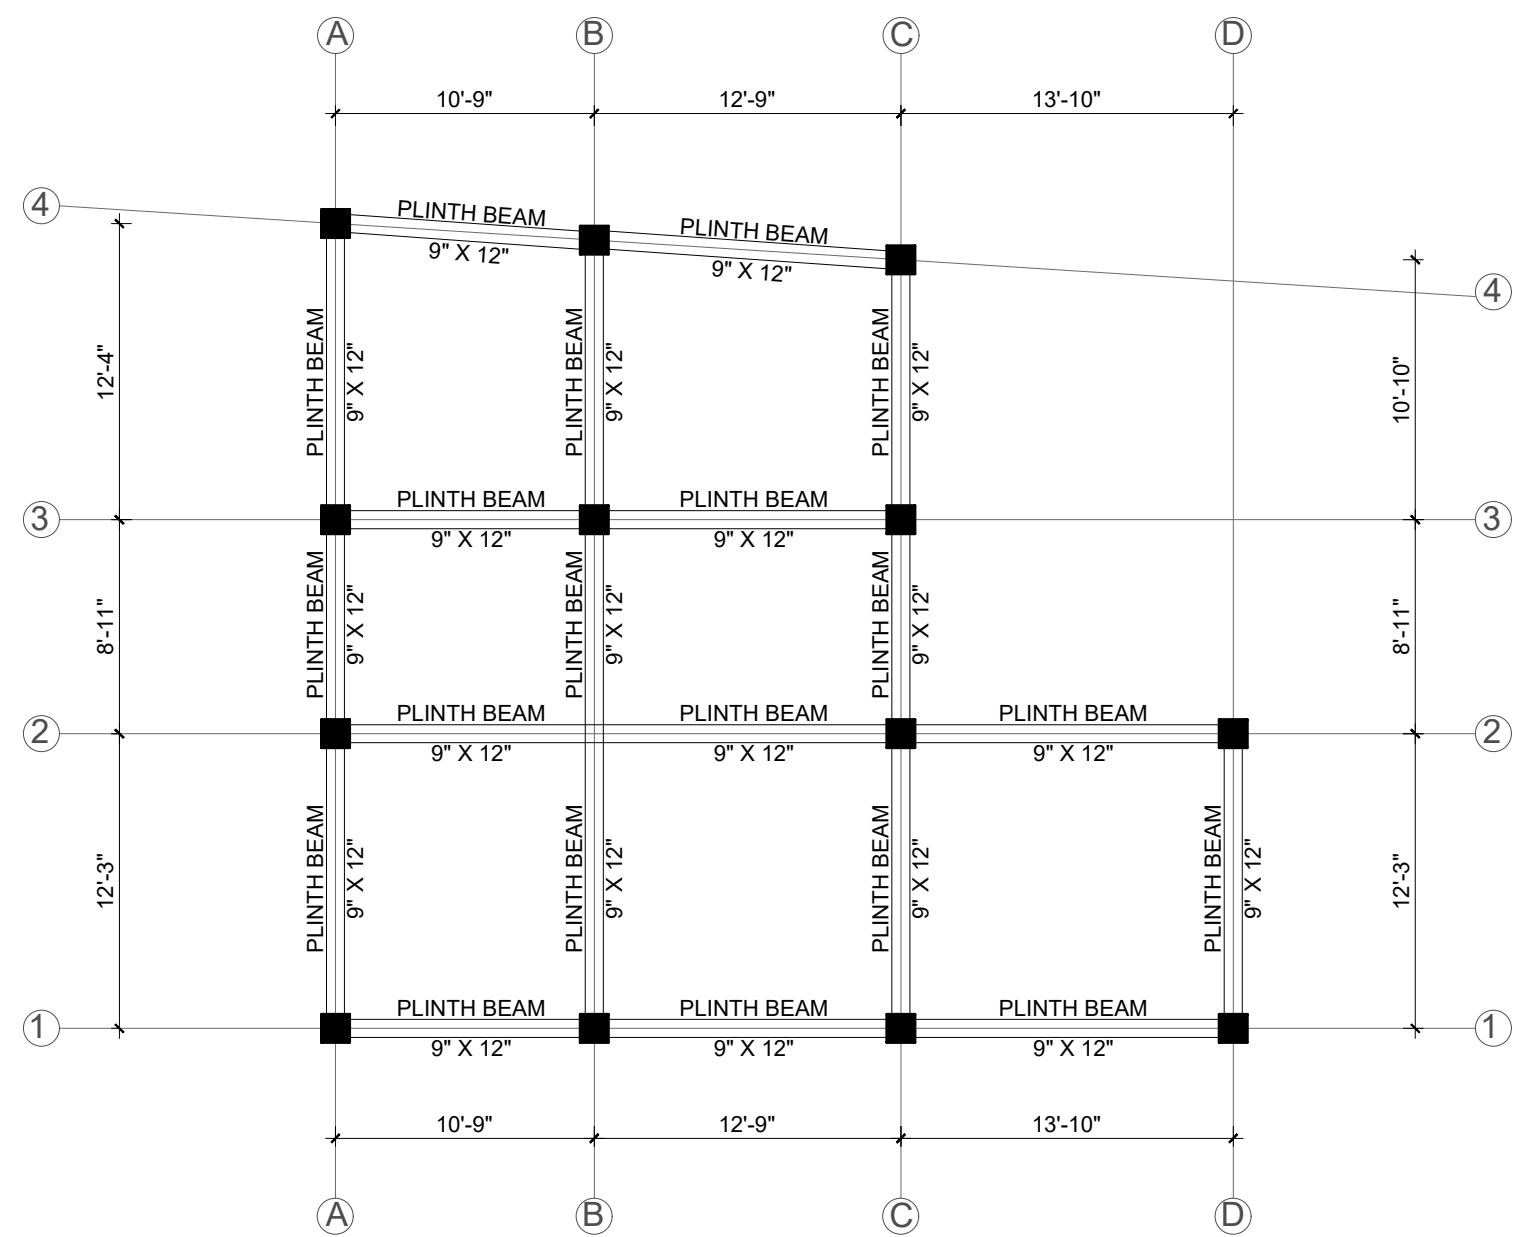


BEAM LAYOUT PLAN (UPPER TIE BEAM AT -10'-0" LVL)

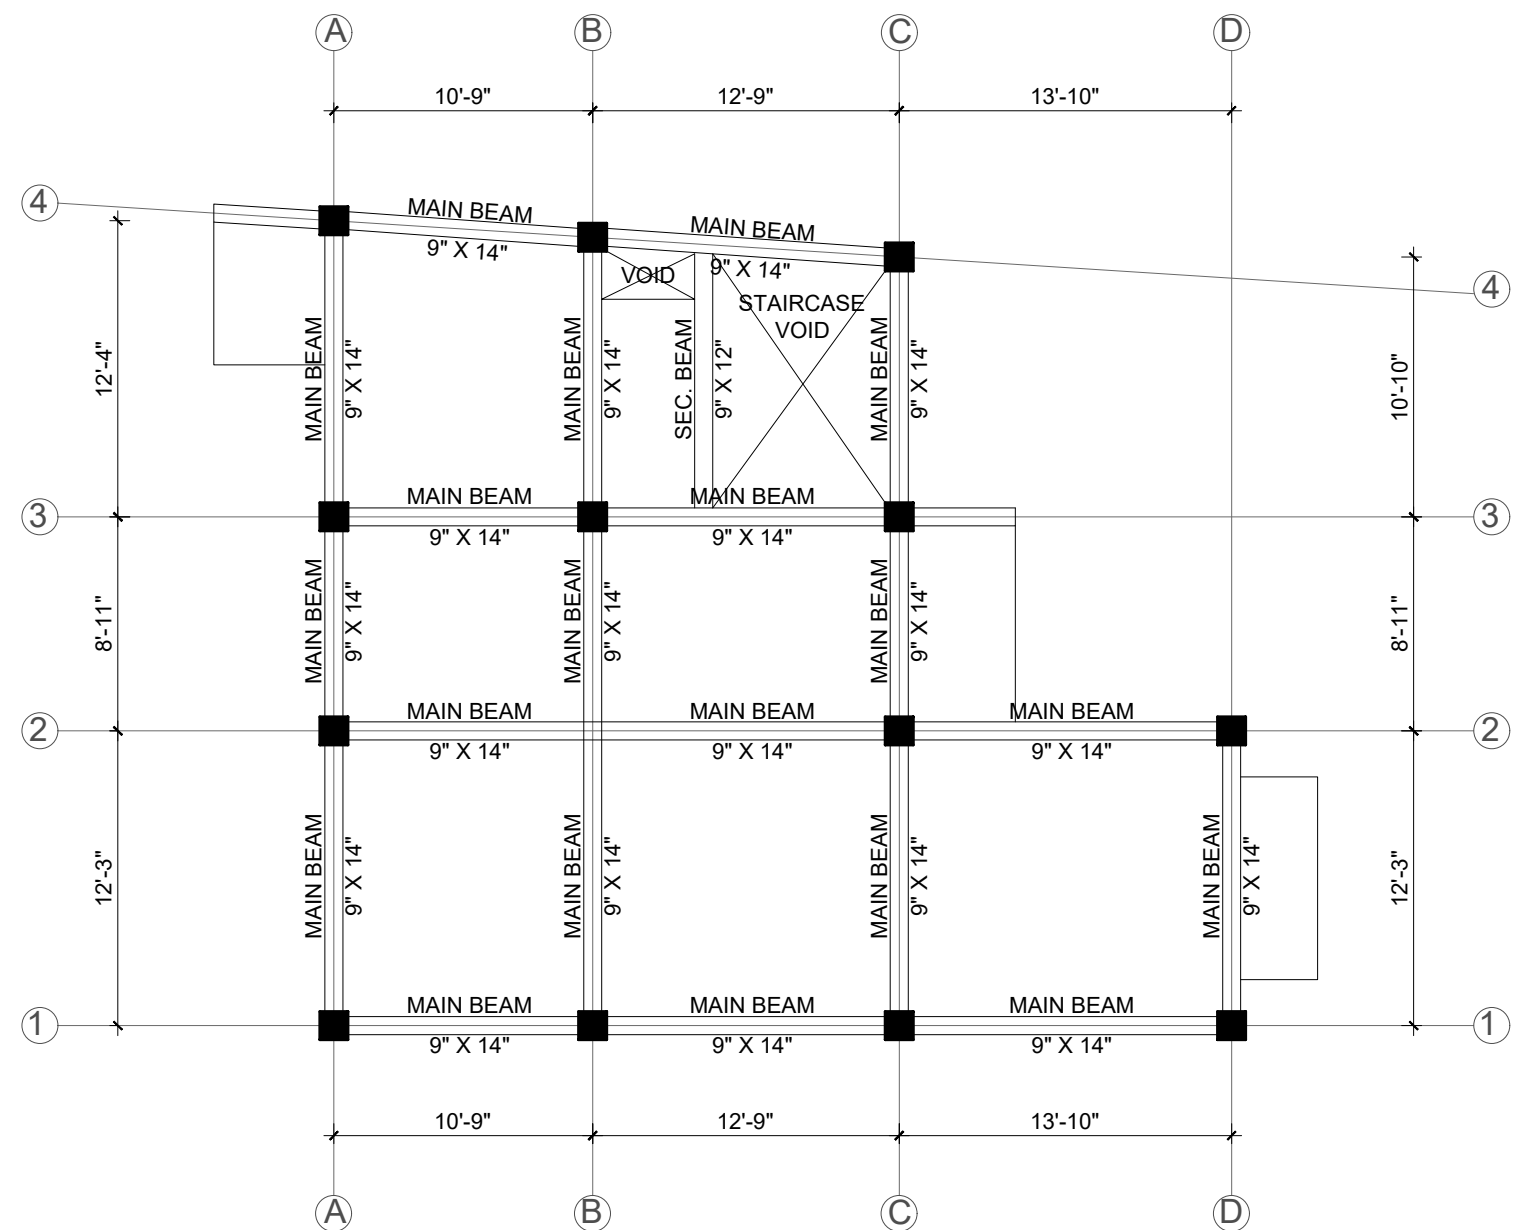


BEAM LAYOUT PLAN (GROUND, FIRST AND SECOND FLOOR)

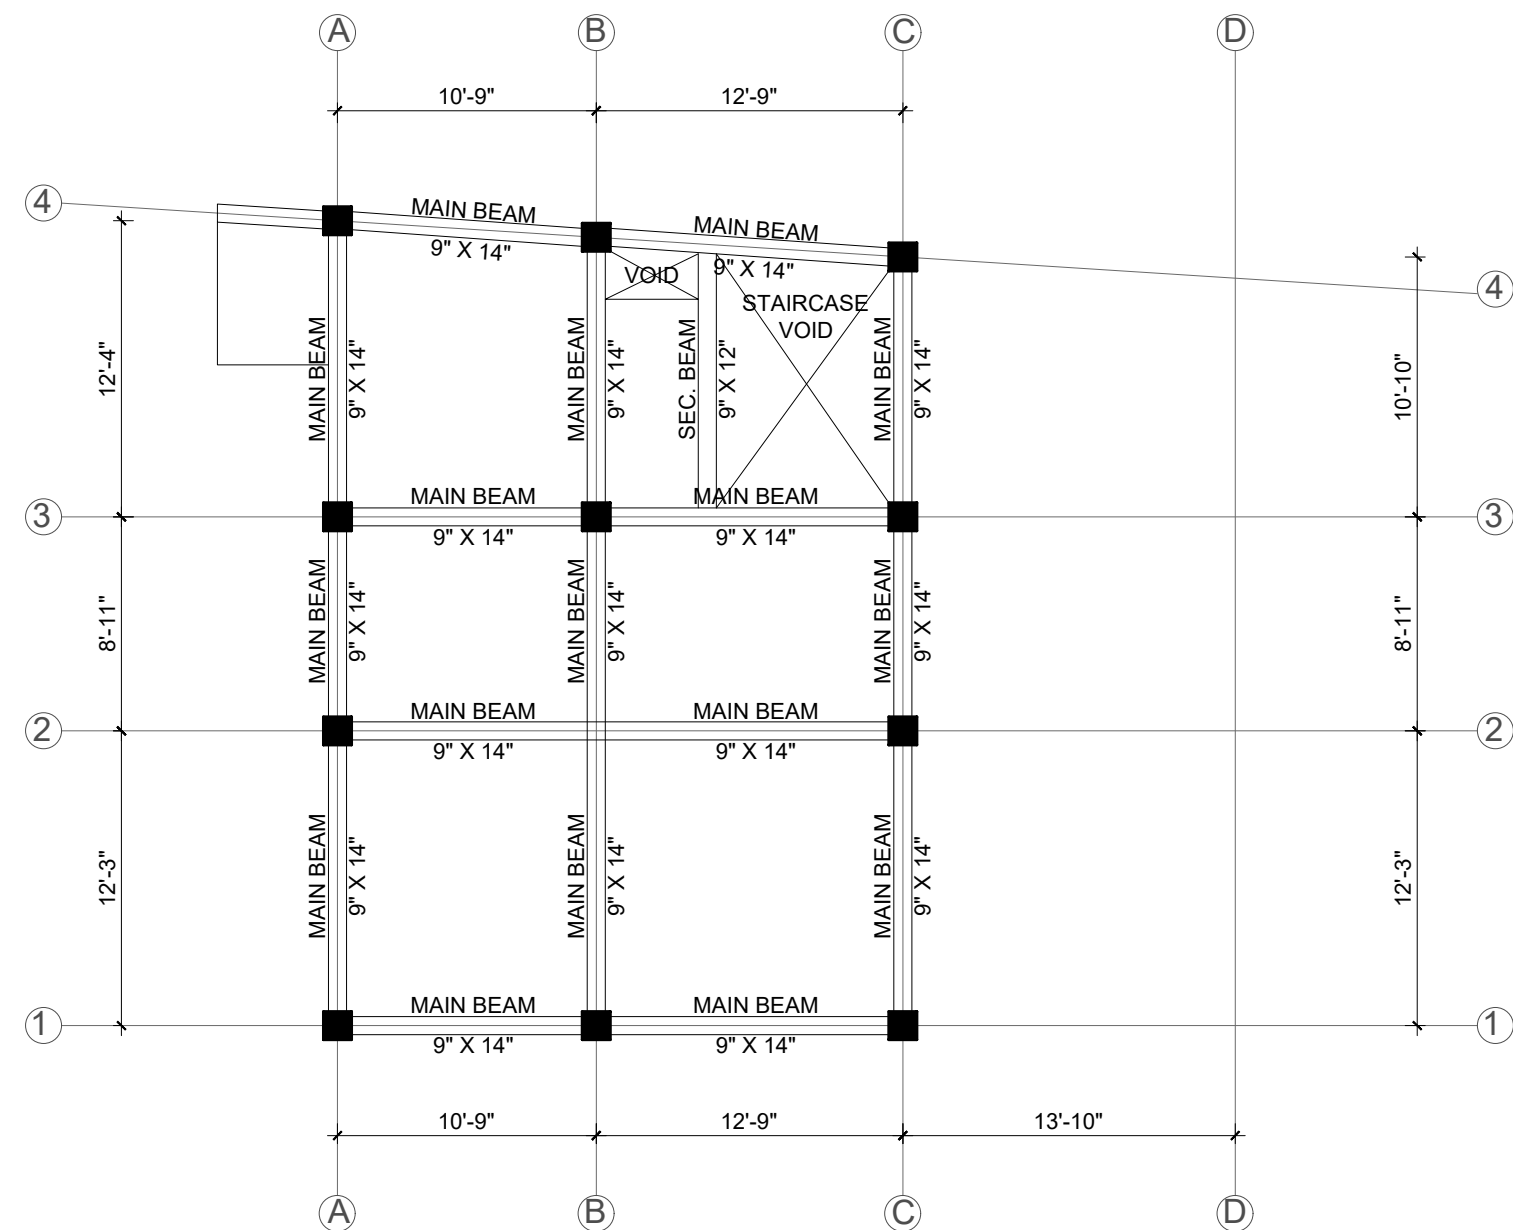


BEAM LAYOUT PLAN (TOP FLOOR)

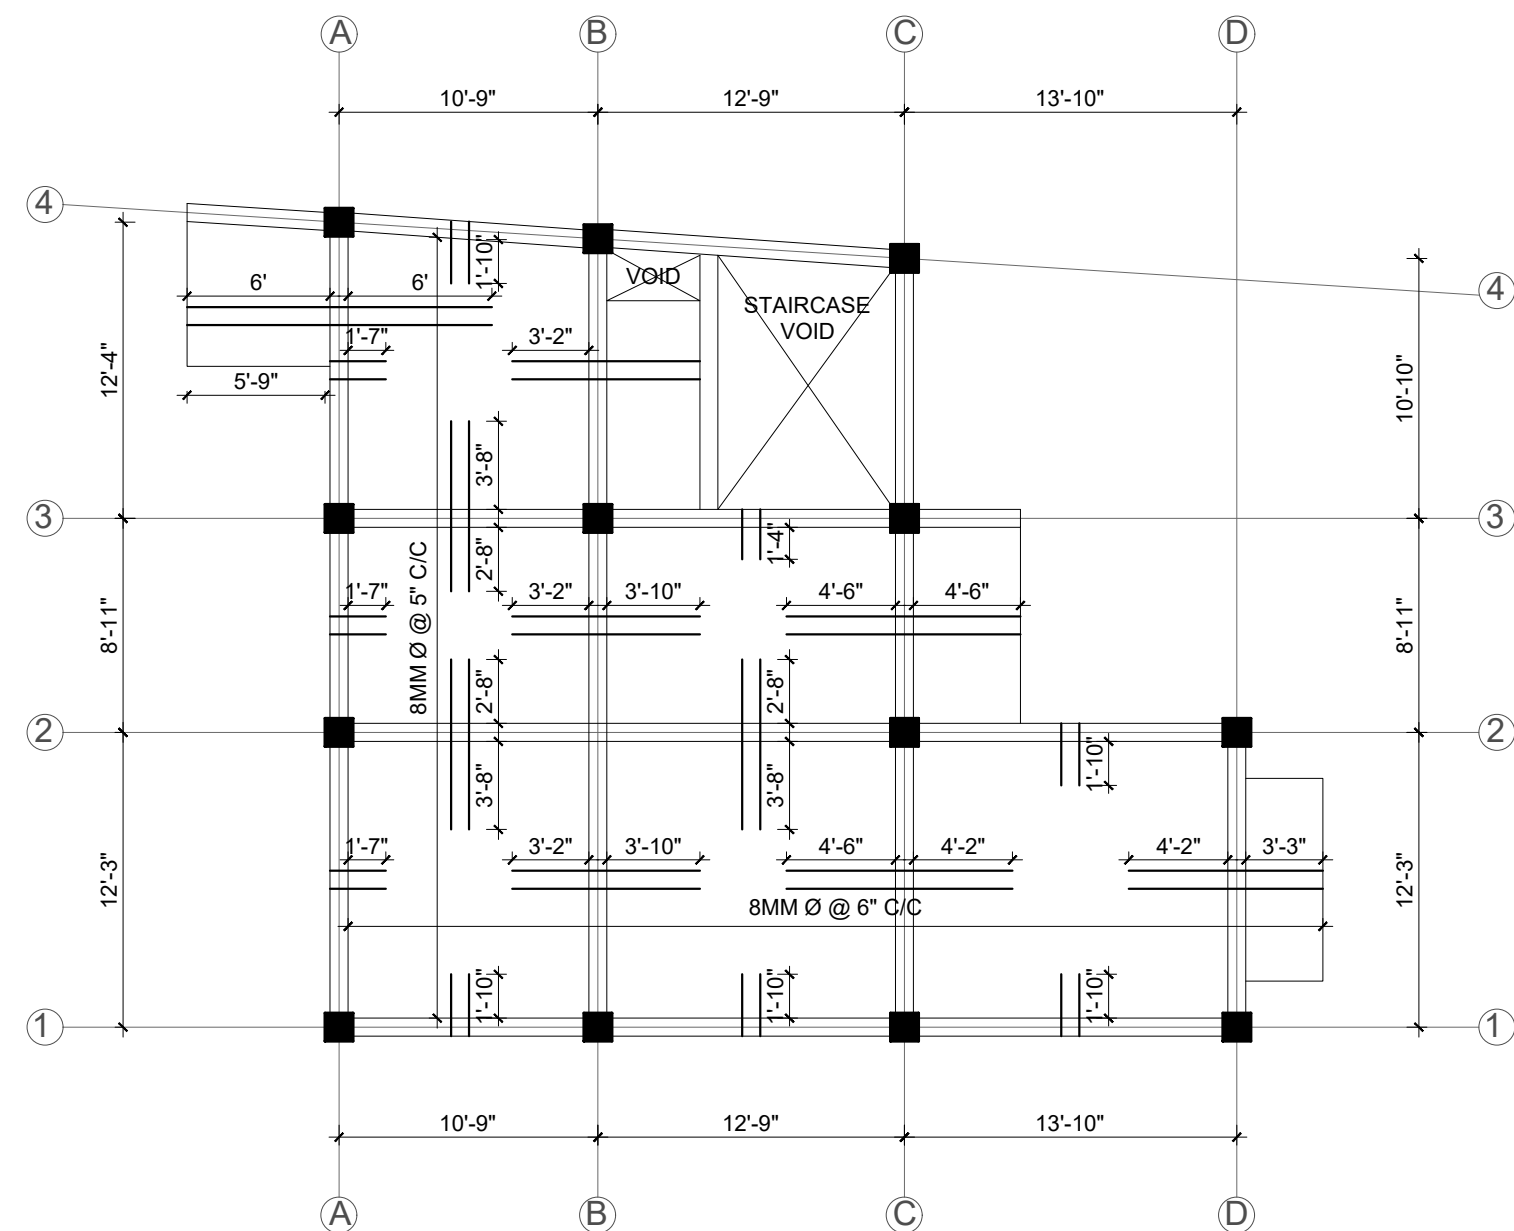


SLAB TOP REINFORCEMENT LAYOUT PLAN (GROUND AND FIRST FLOOR)

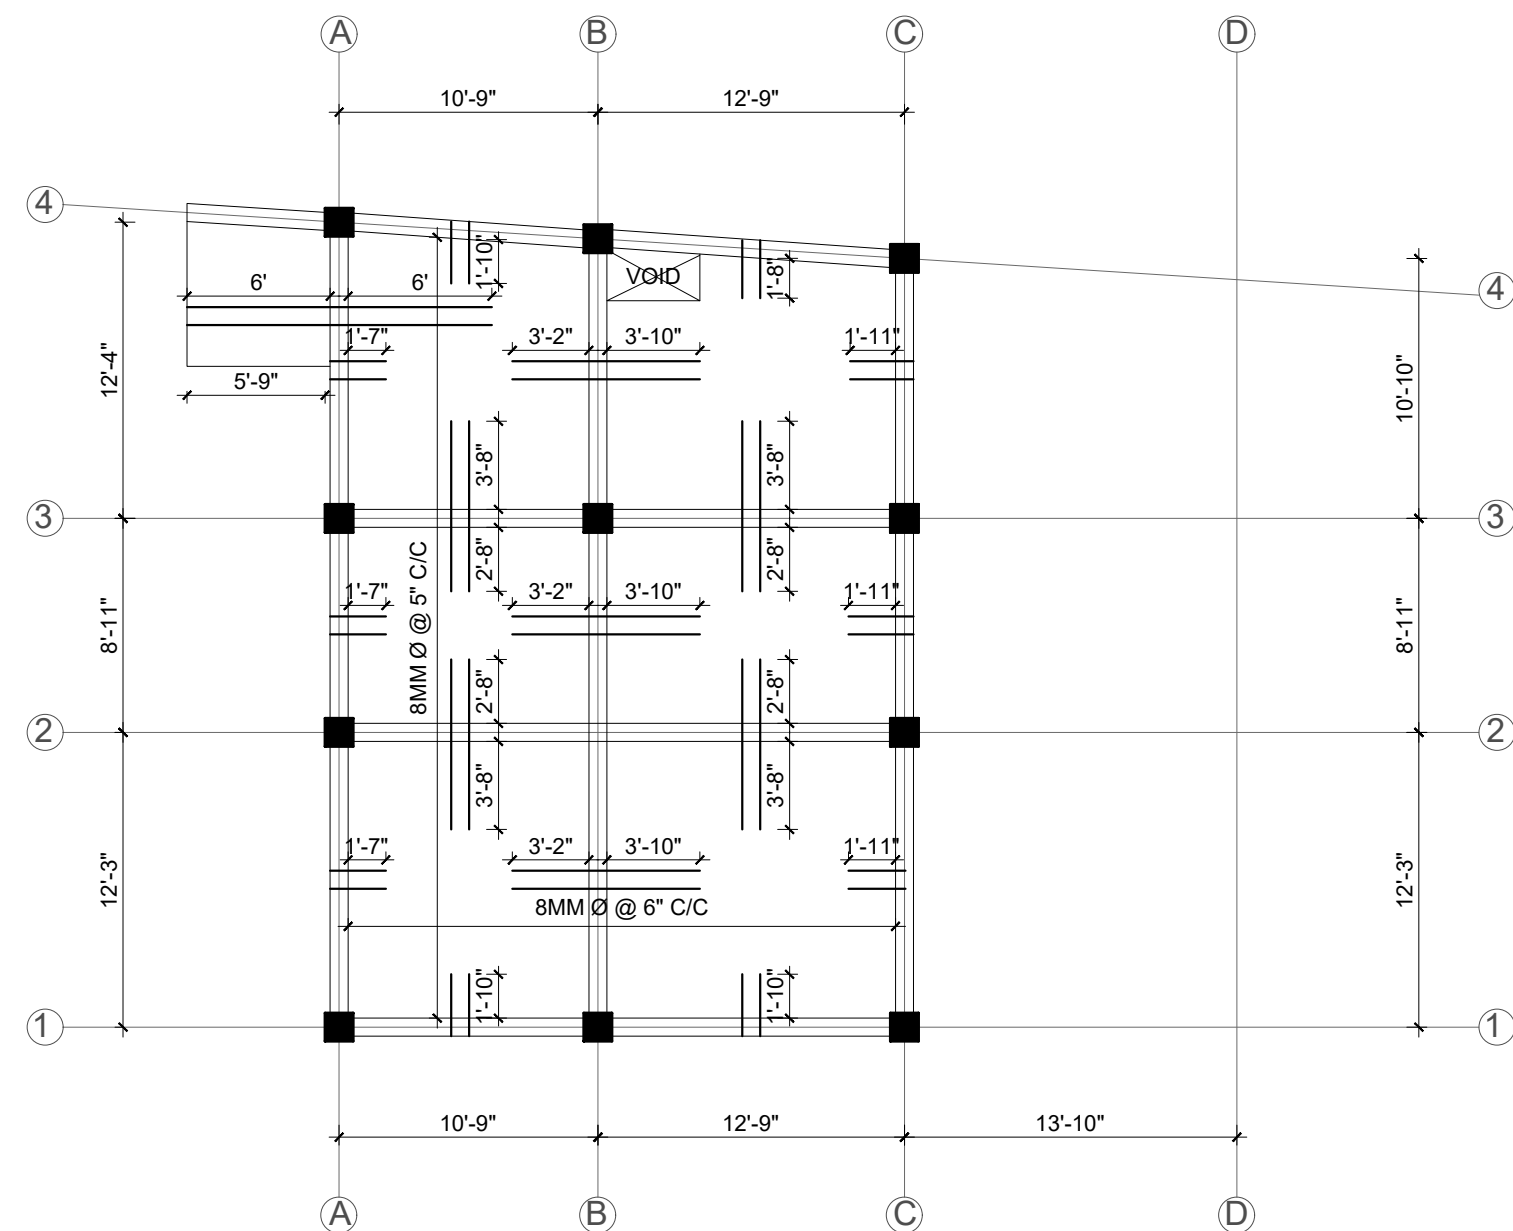



SLAB TOP REINFORCEMENT LAYOUT PLAN (TOP FLOOR)

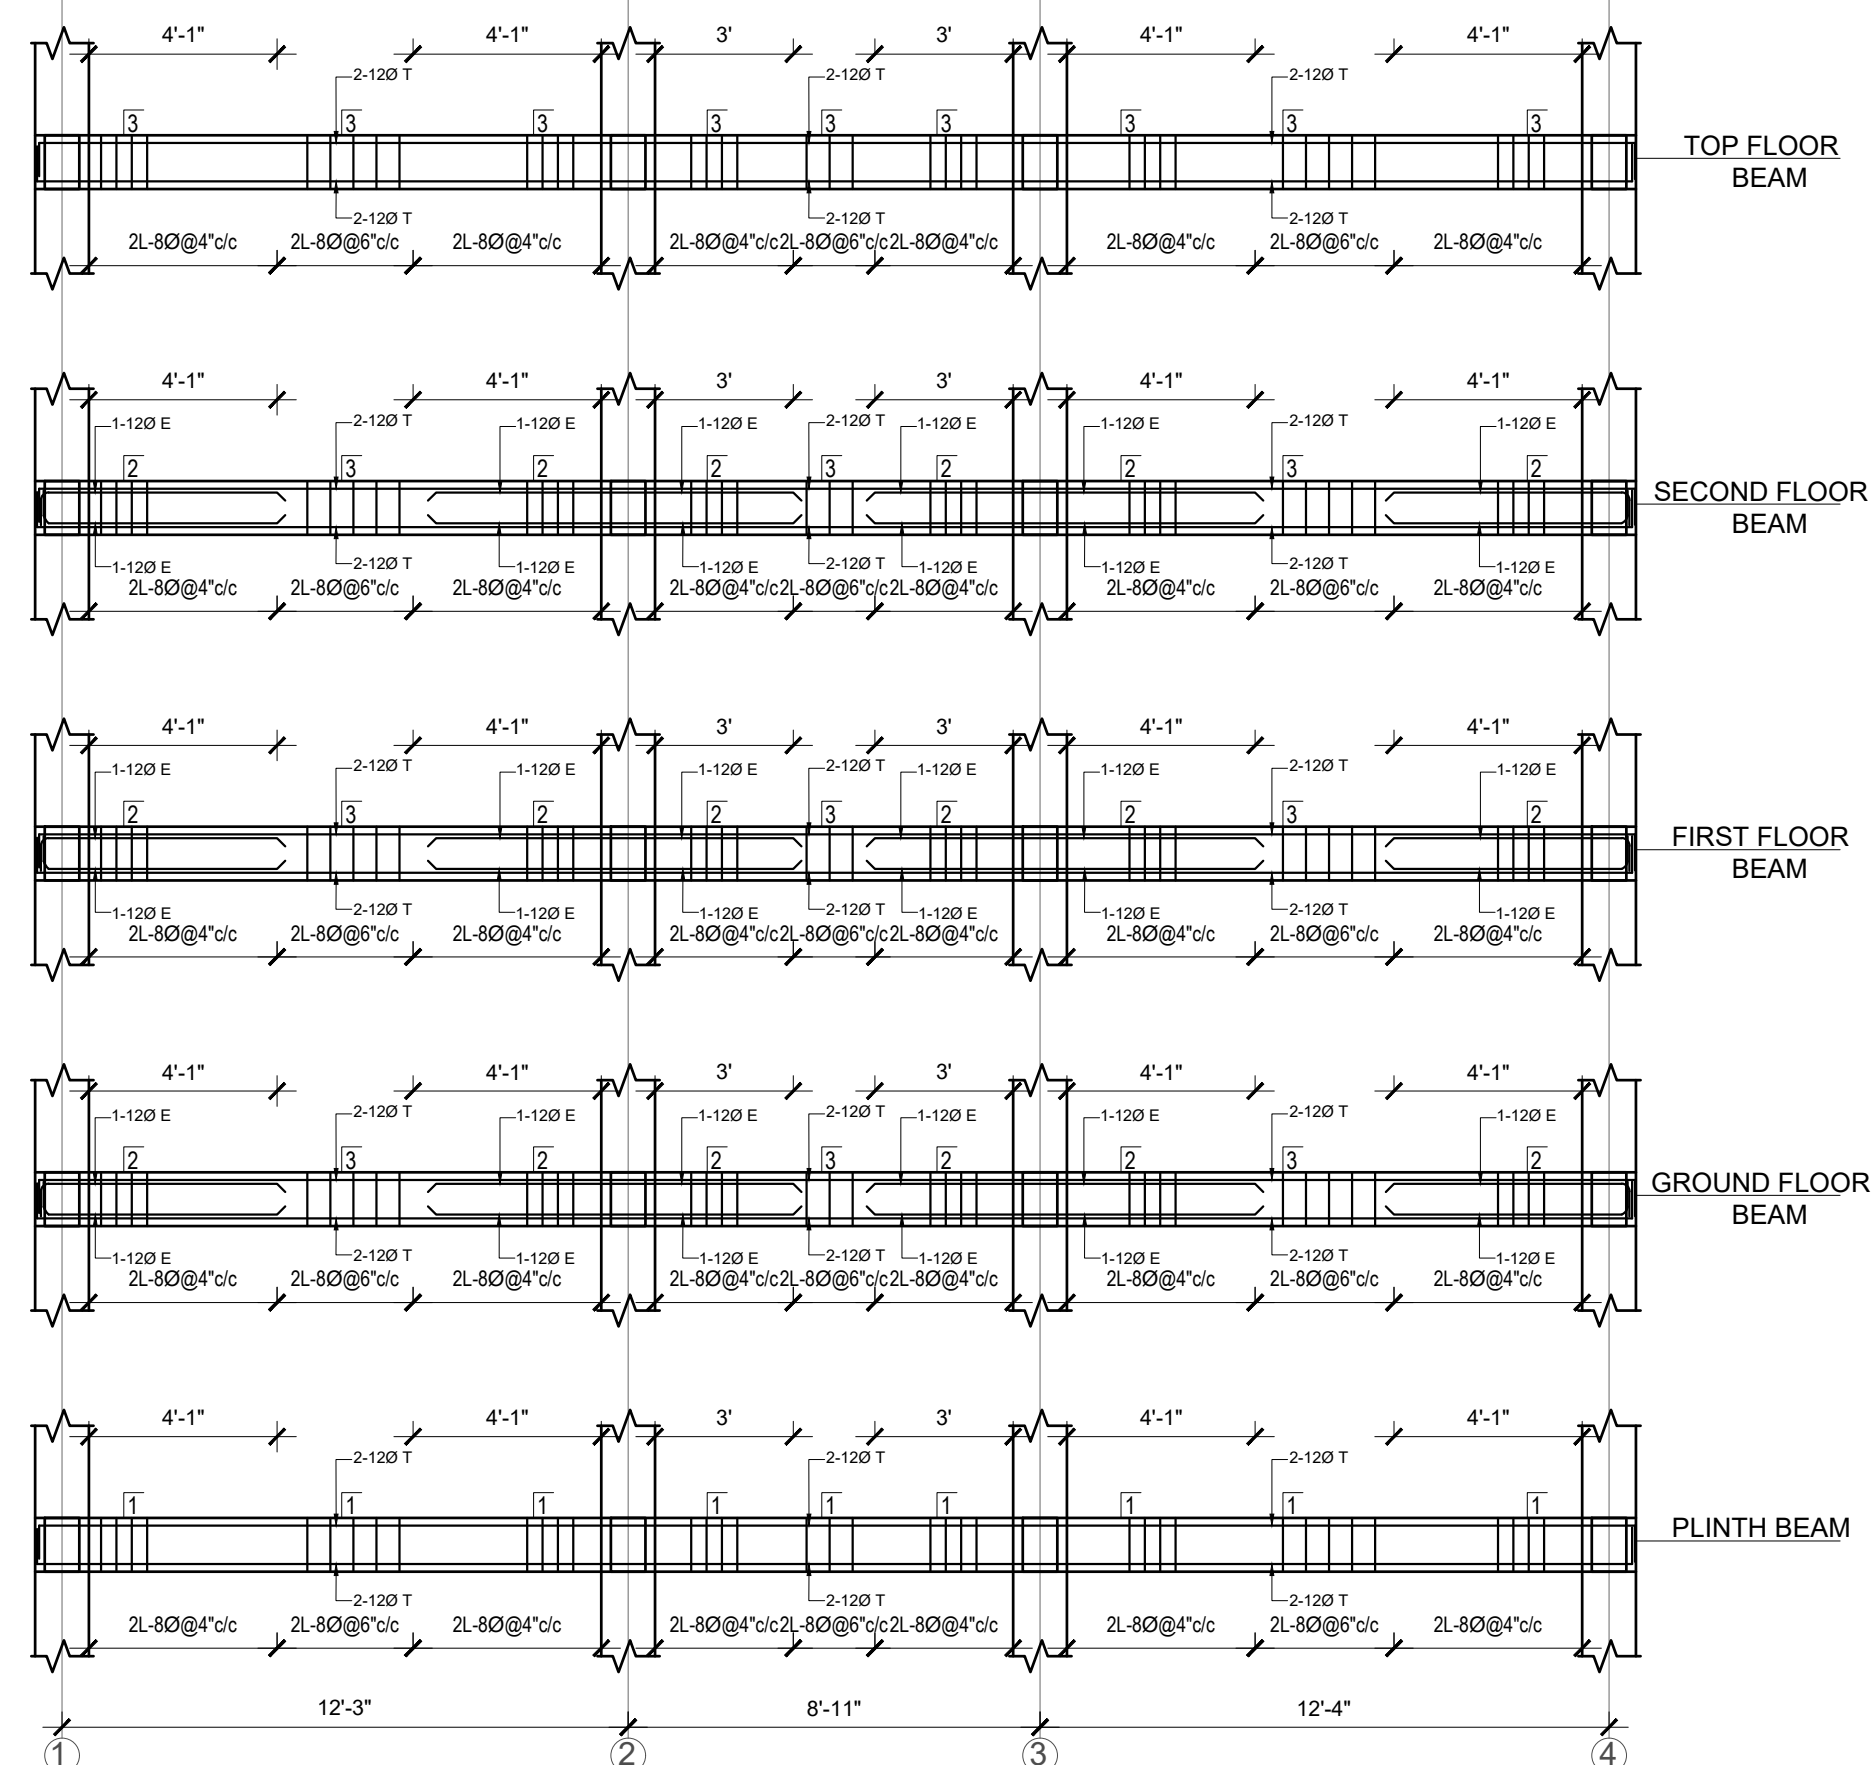

BEAM ELEVATION THROUGH A-A

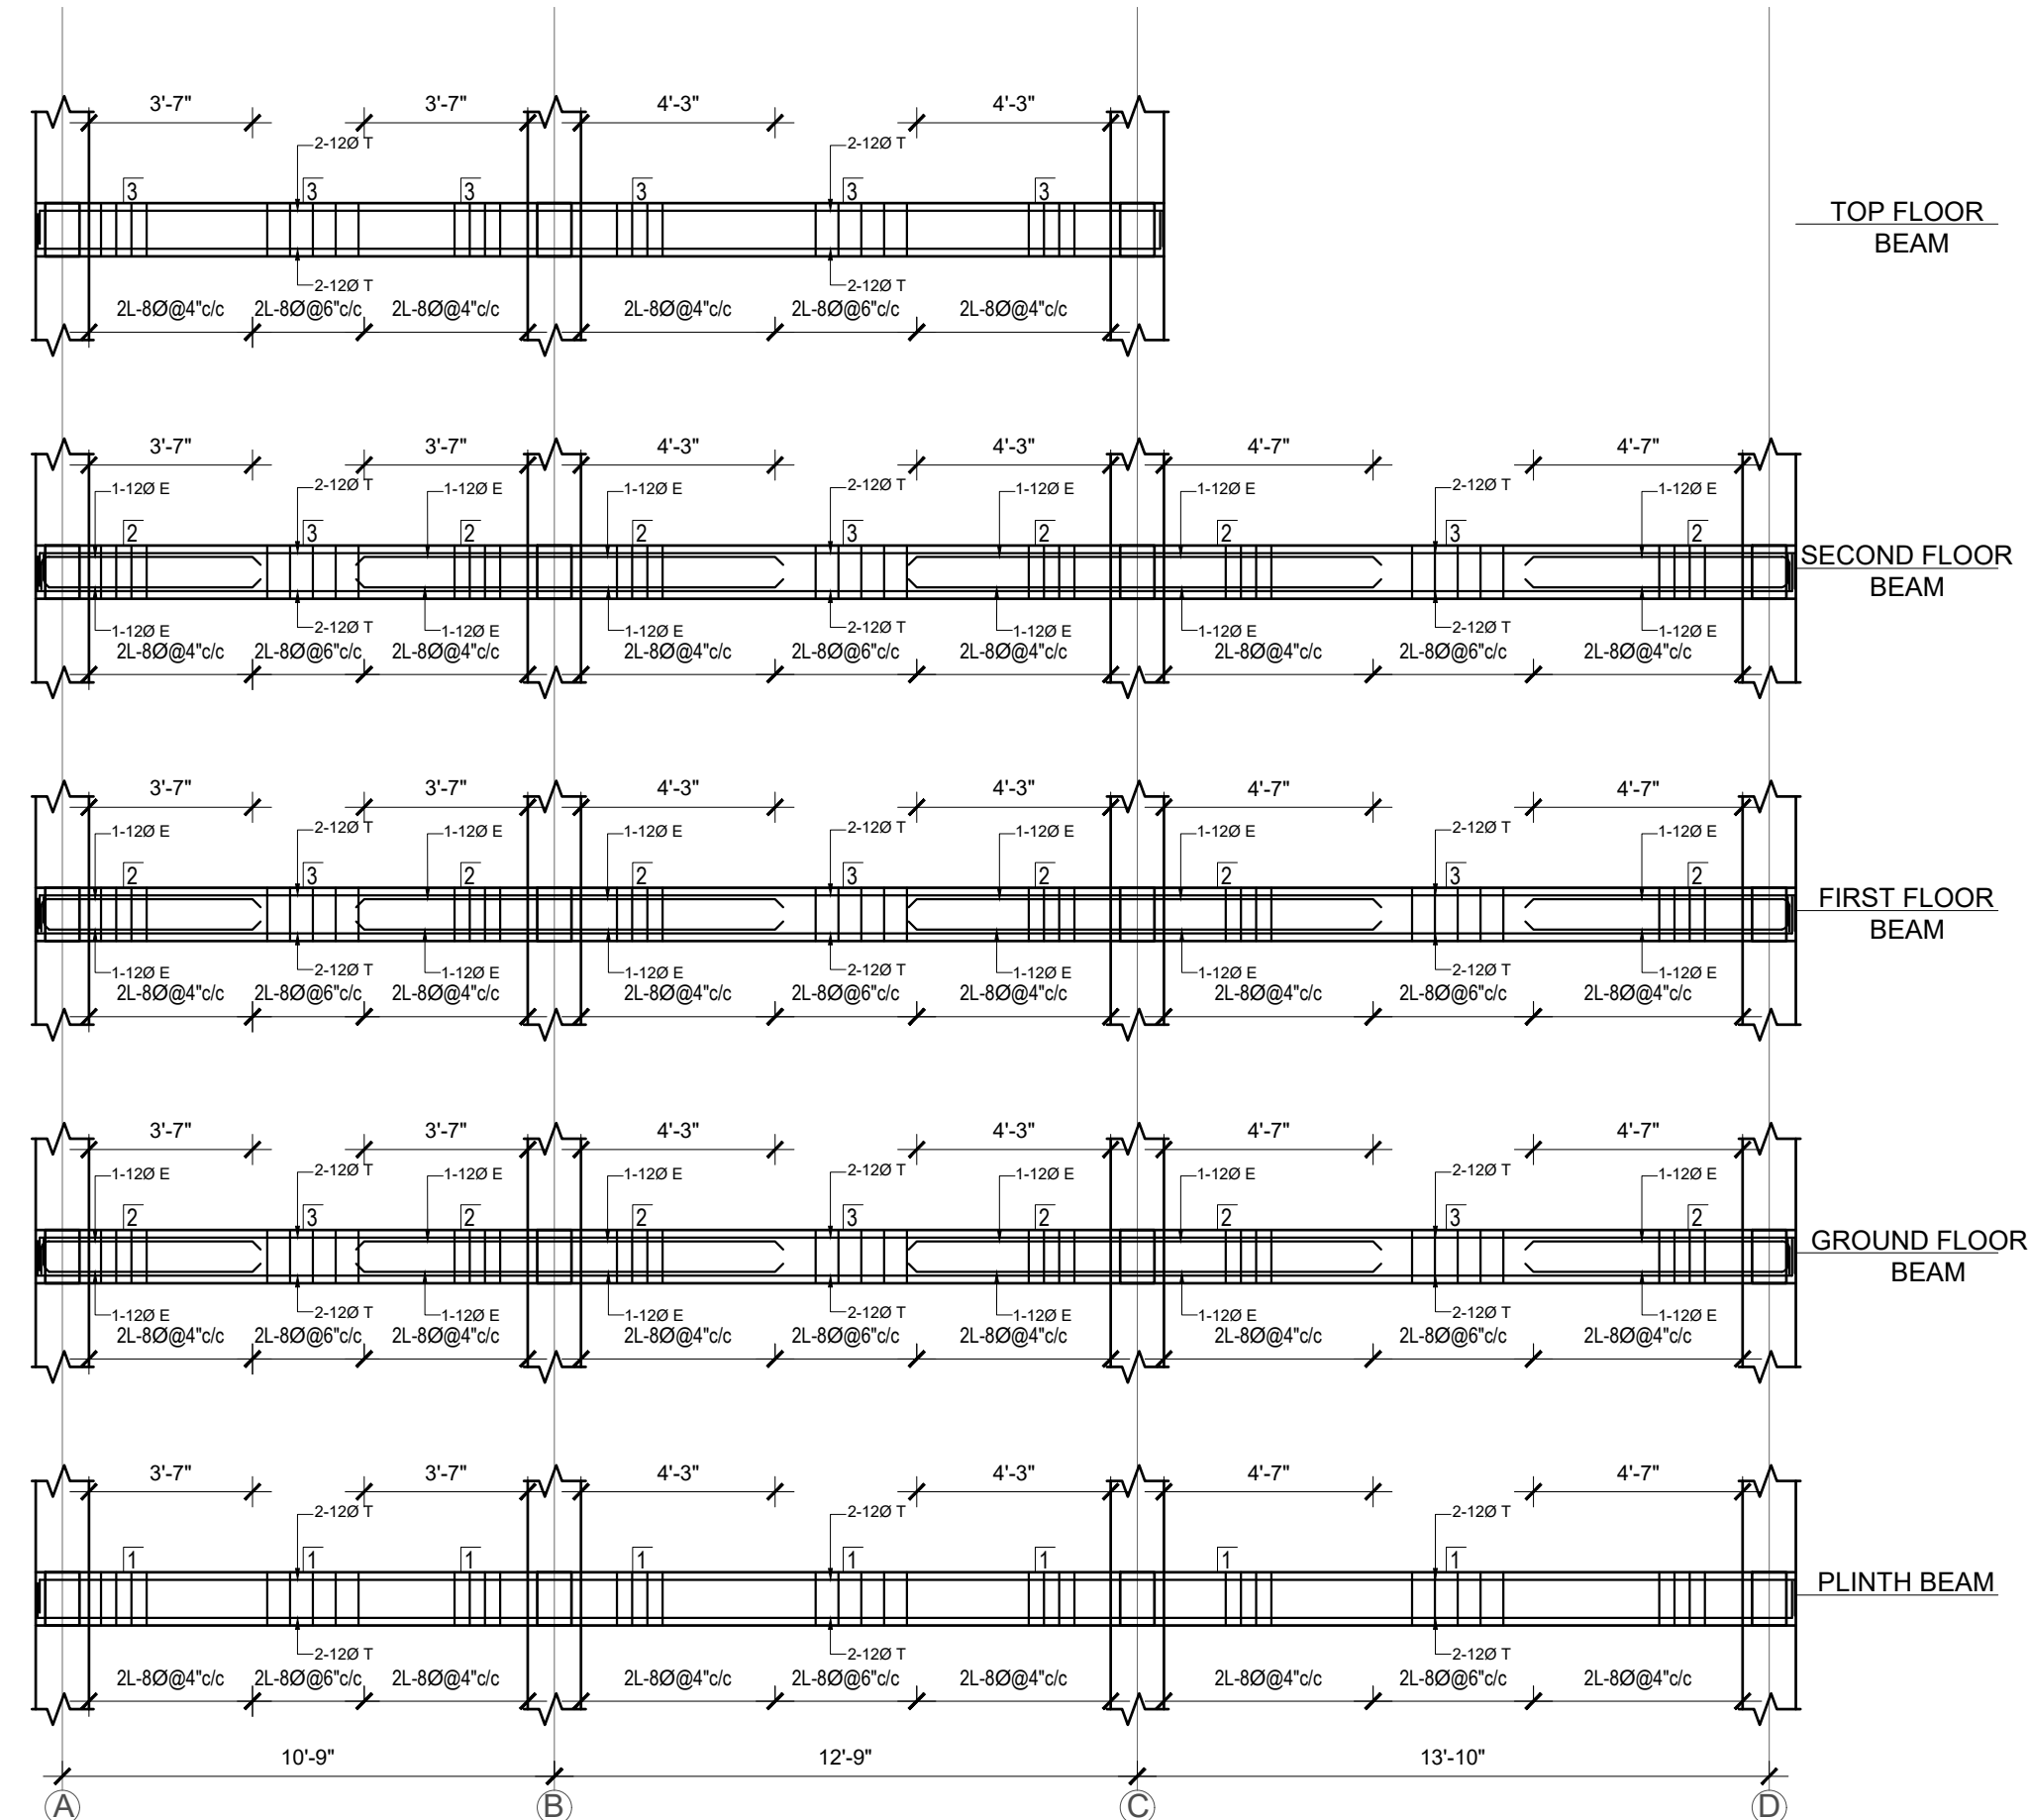

BEAM ELEVATION THROUGH I-1

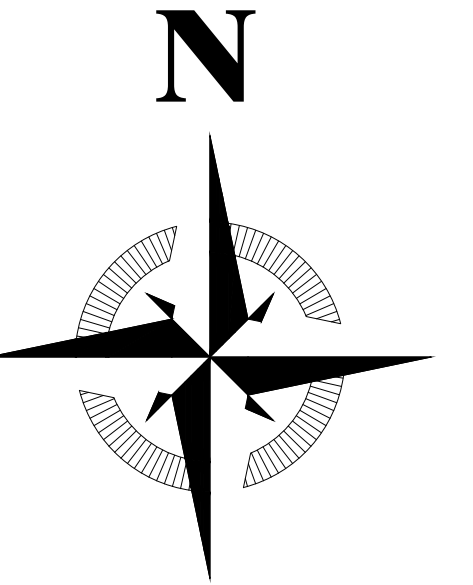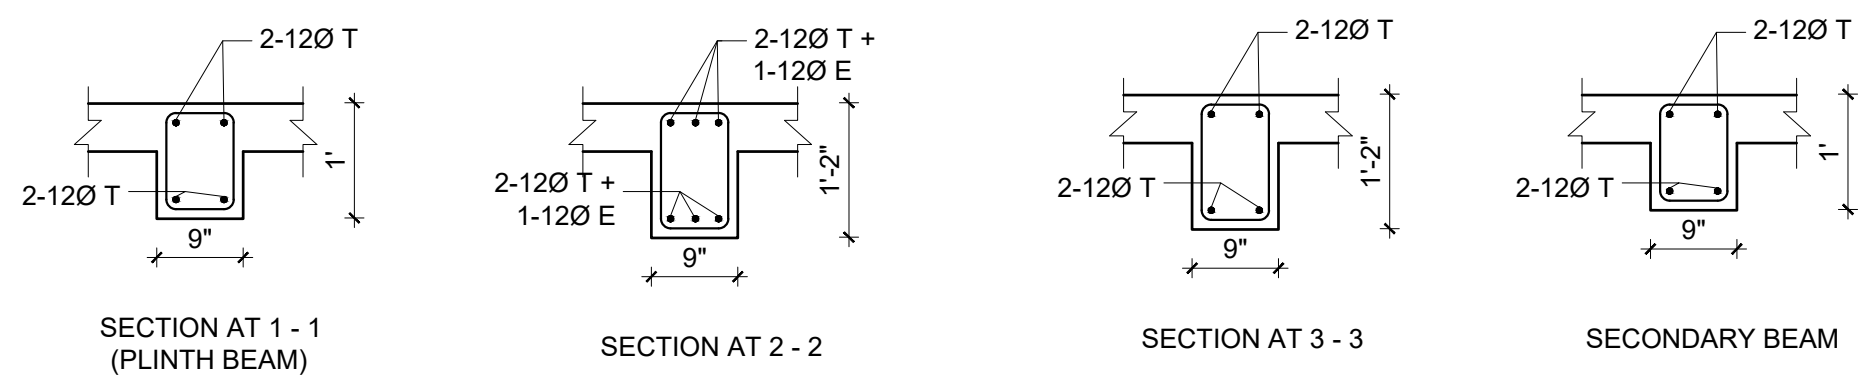

REVISIONS

REV.	DESCRIPTION	DATE
A		



URBAN PARK PVT. LTD.
KATHMANDU, NEPAL
urbanparknepal@gmail.com

OWNER: Mr. DHAN KUMARI KHATRI

SIGNATURE:


BUILDING TYPE: RESIDENTIAL	LOCATION: BUDHANILKANTHA, WARD NO. 3
PLOT NO: 125	AREA: 176.96 SQ.M. (0-5-2-1.05) 174.85 SQ.M. (0-5-2-0) ACCORDING TO LALPURA

DETAILS:
STRUTURAL DRAWINGS


ARCHITECT: AR. APIL K. C.

DATE: SEP 2021
SCALE: 1"=8'-0" (1:96)
SIGNATURE :


NEC REGISTRATION NO.
1070 "A"
REMARKS:

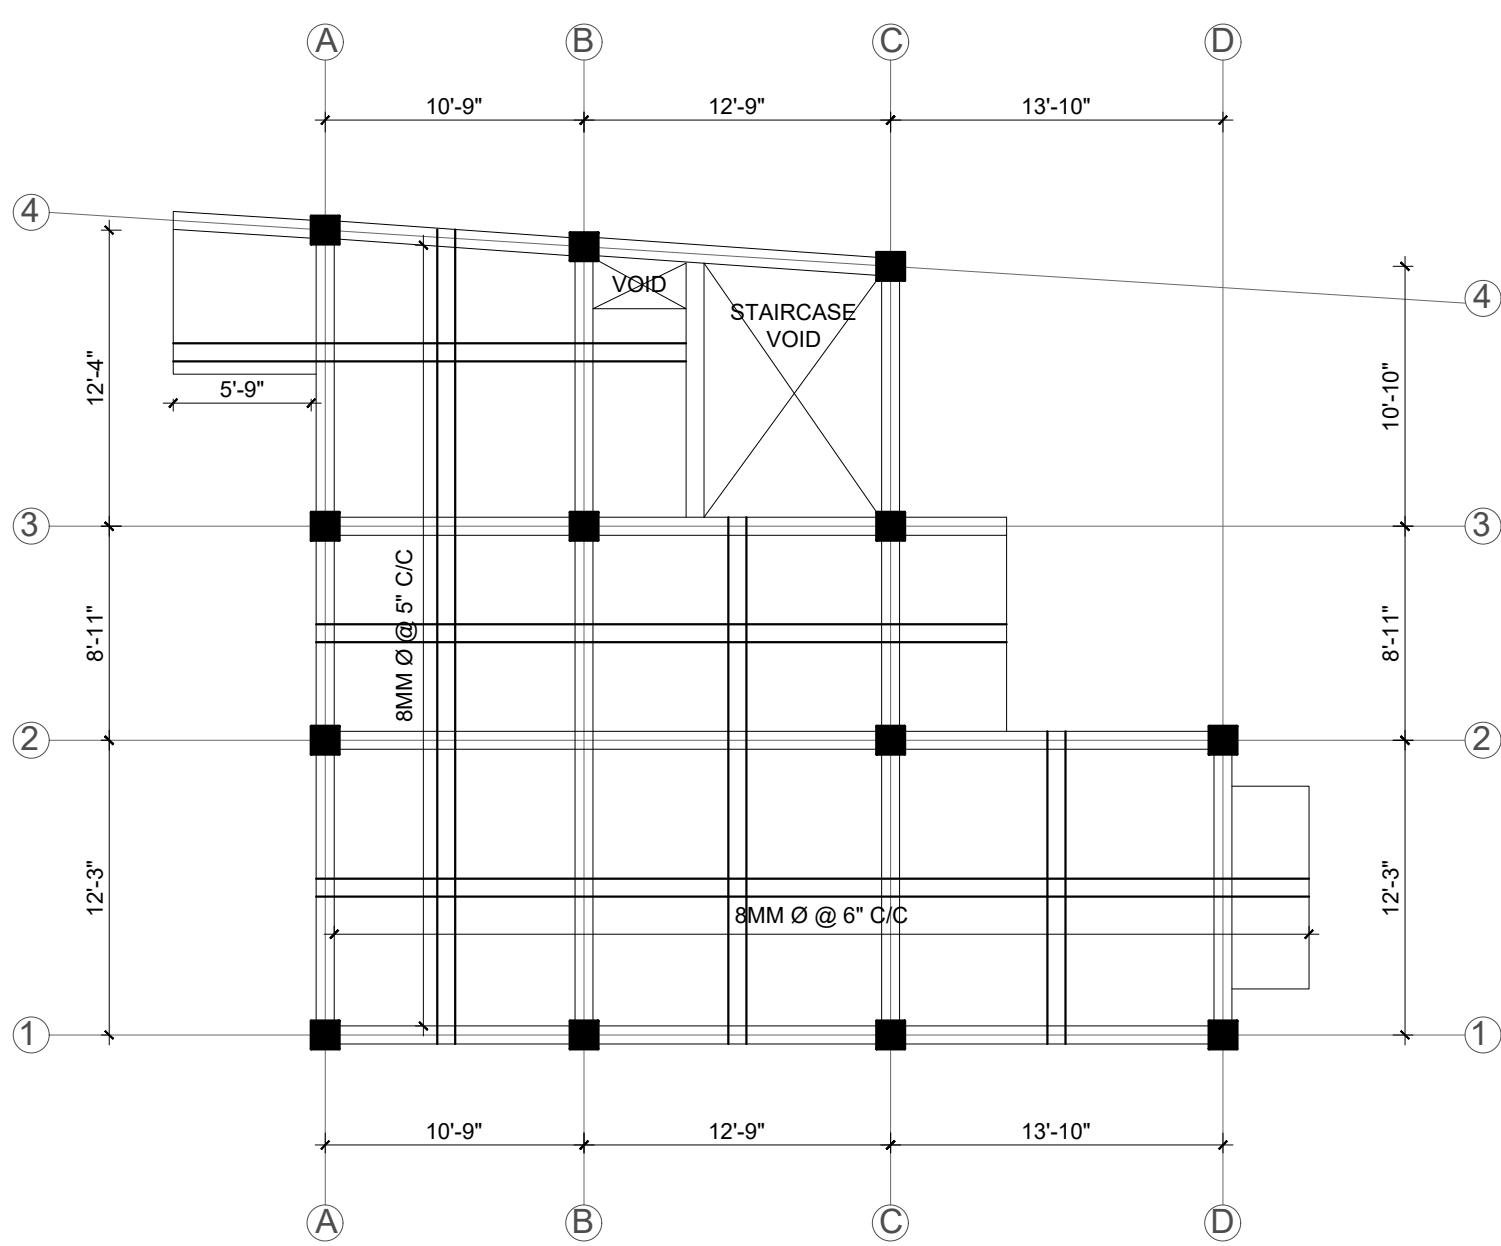


SLAB BOTTOM REINFORCEMENT LAYOUT PLAN (GROUND AND FIRST FLOOR)

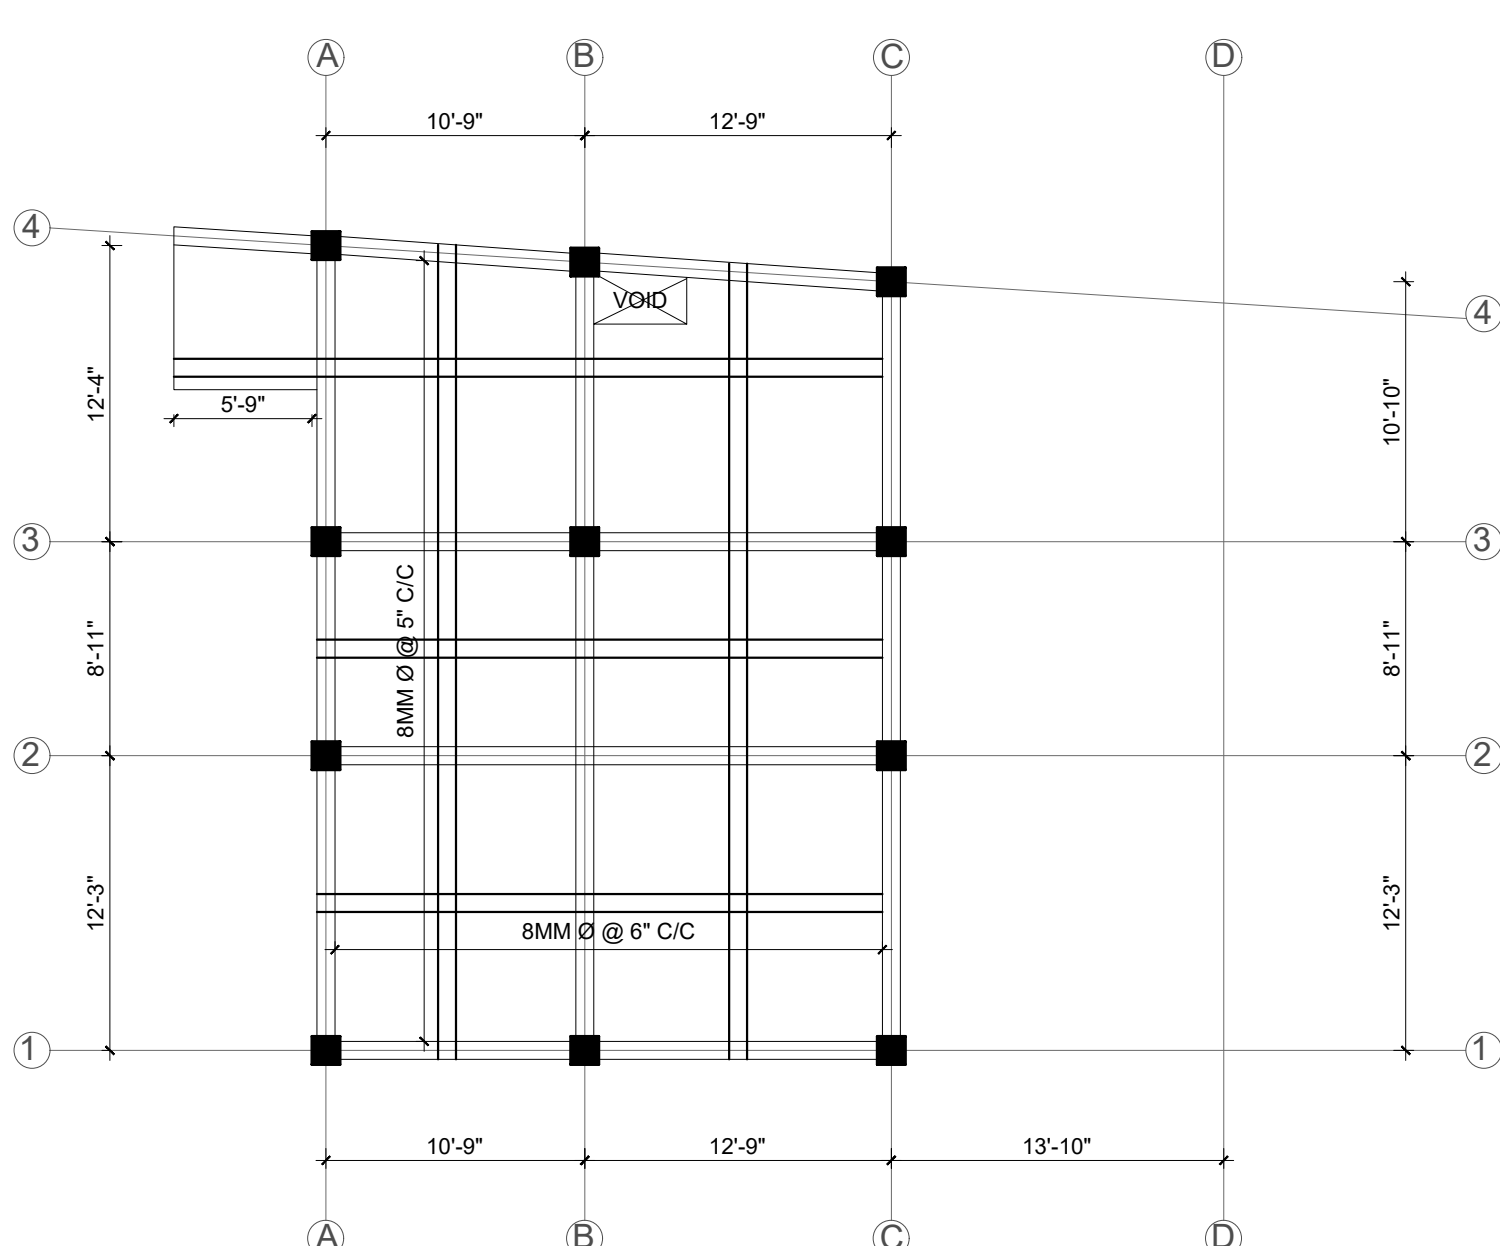


SLAB BOTTOM REINFORCEMENT LAYOUT PLAN (TOP FLOOR)

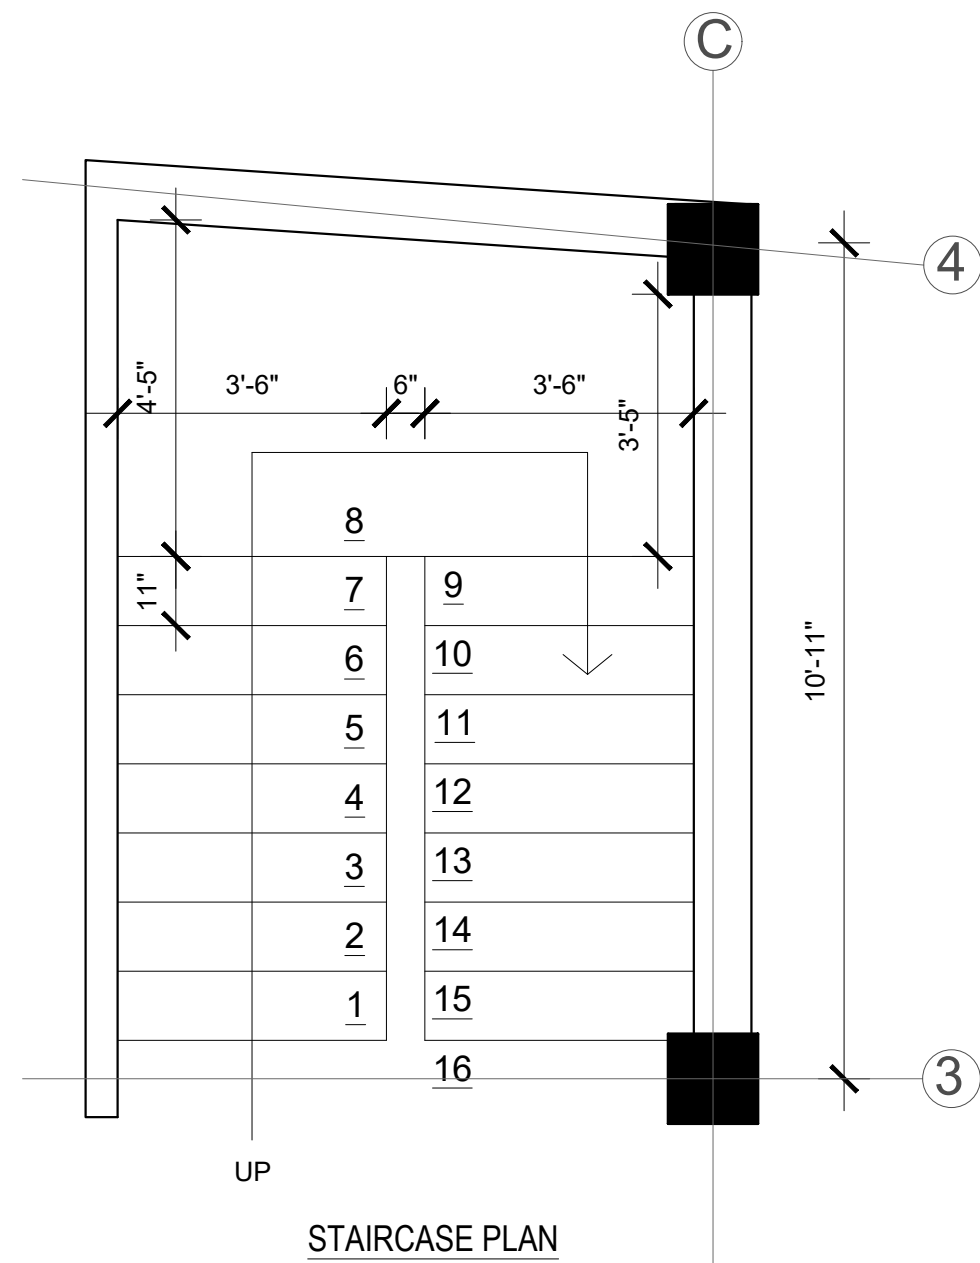


STAIRCASE PLAN

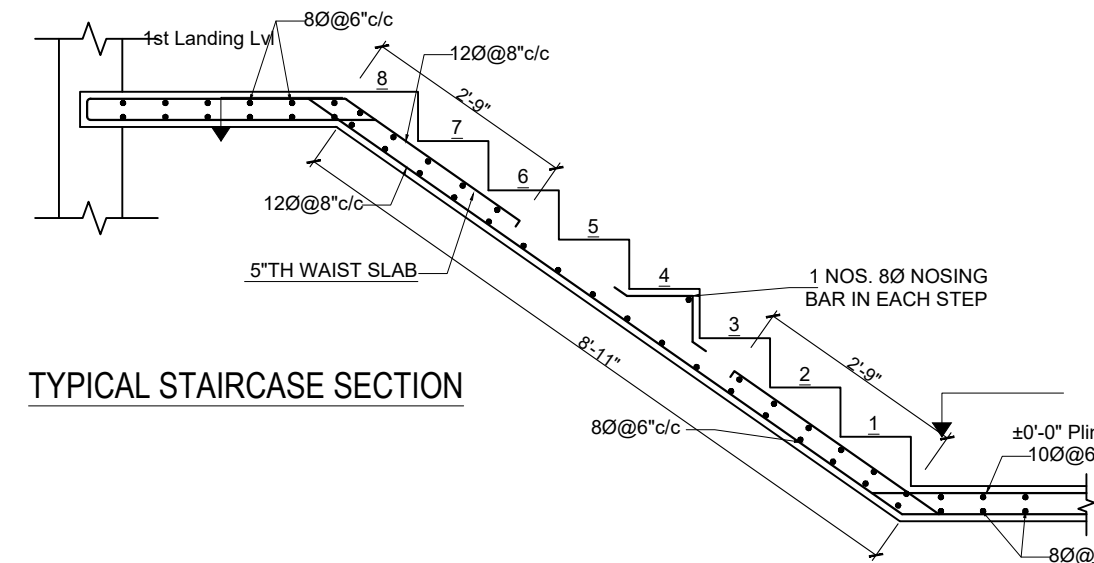


TYPICAL STAIRCASE SECTION

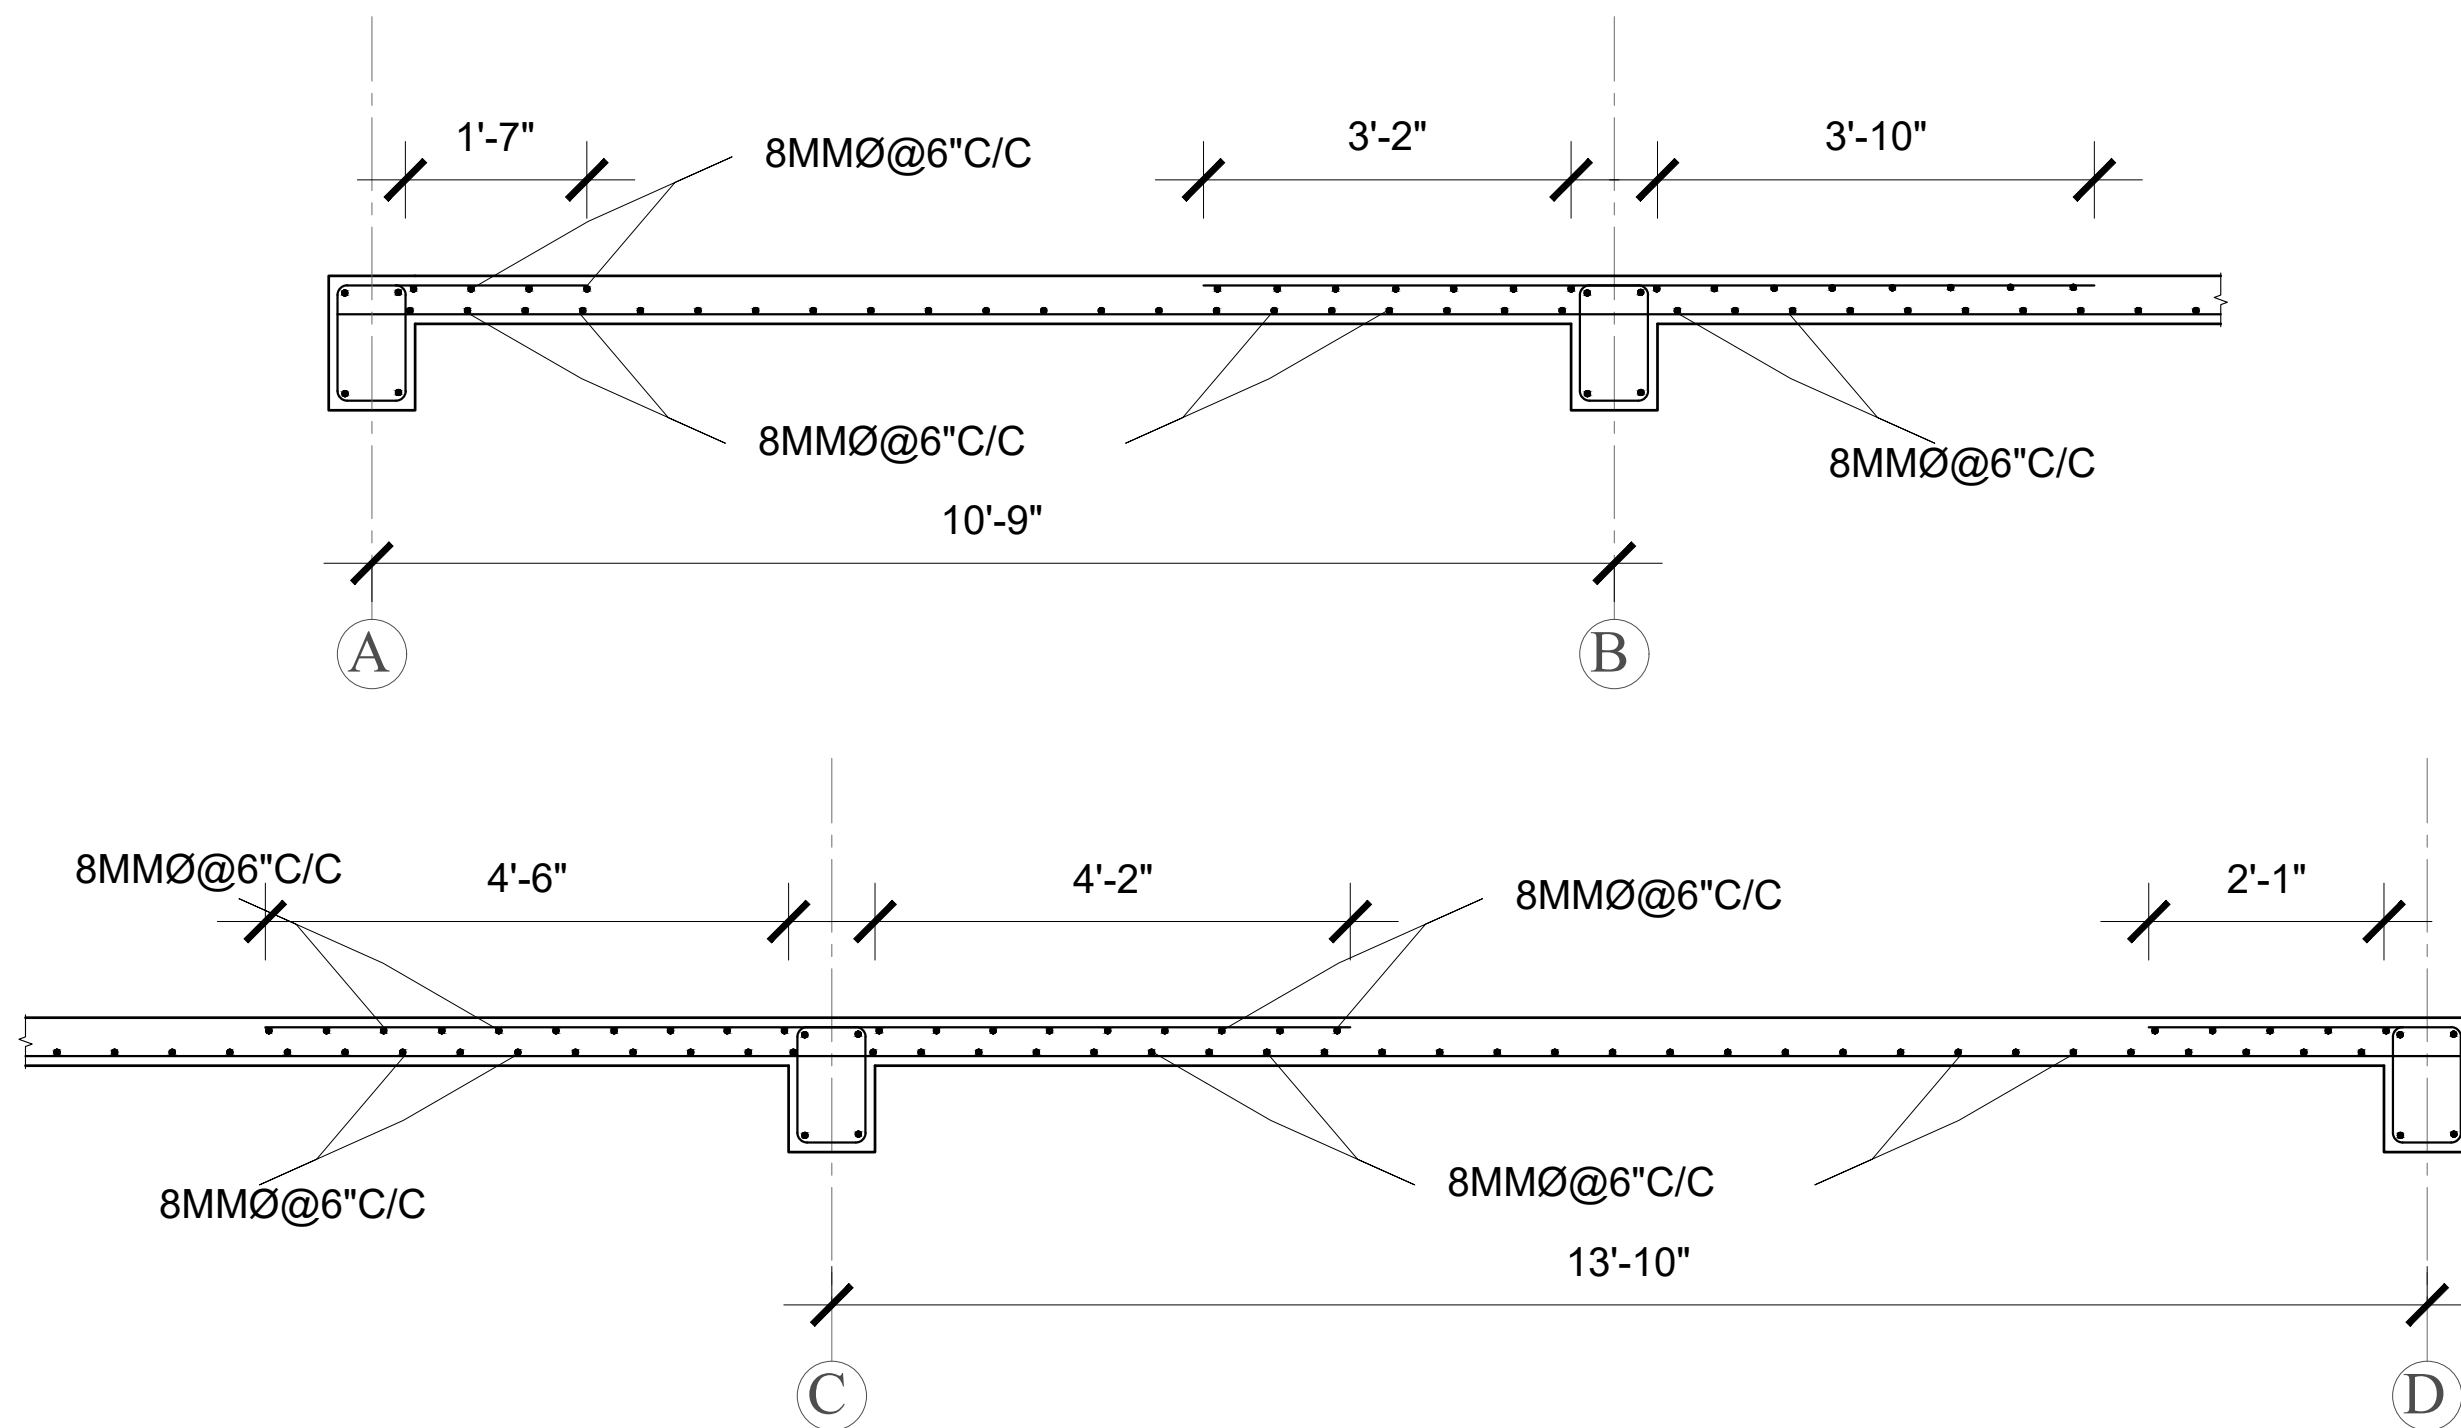


TYPICAL SLAB SECTION AT 1-1

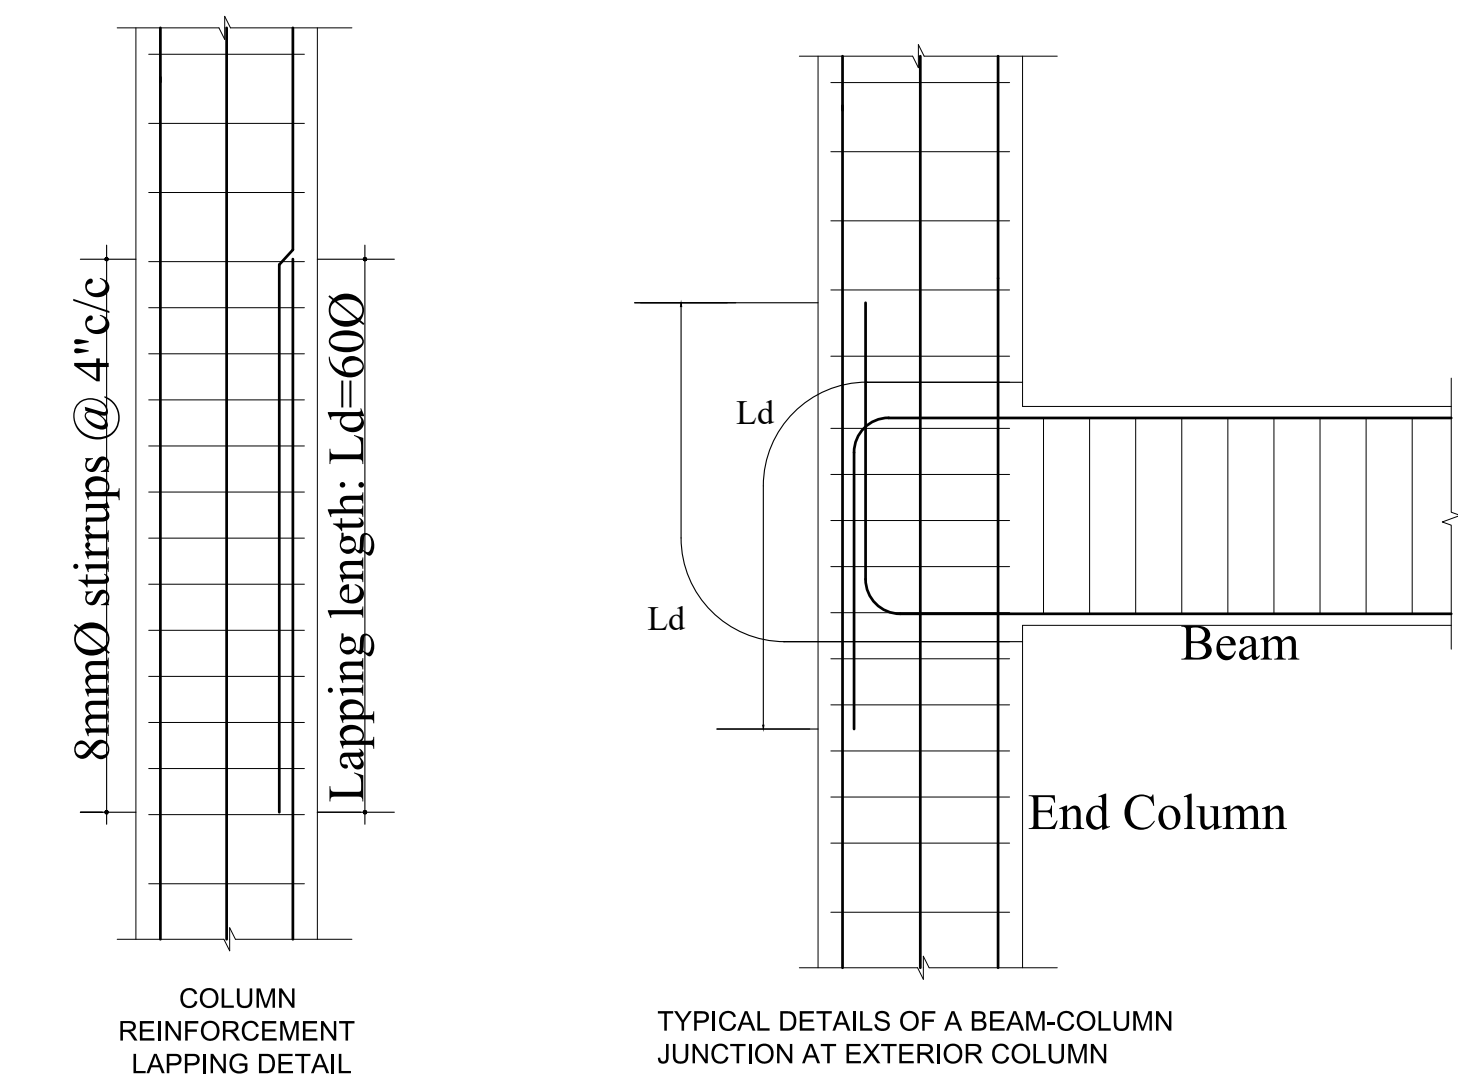

TYPICAL DETAILS OF A BEAM-COLUMN JUNCTION AT EXTERIOR COLUMN

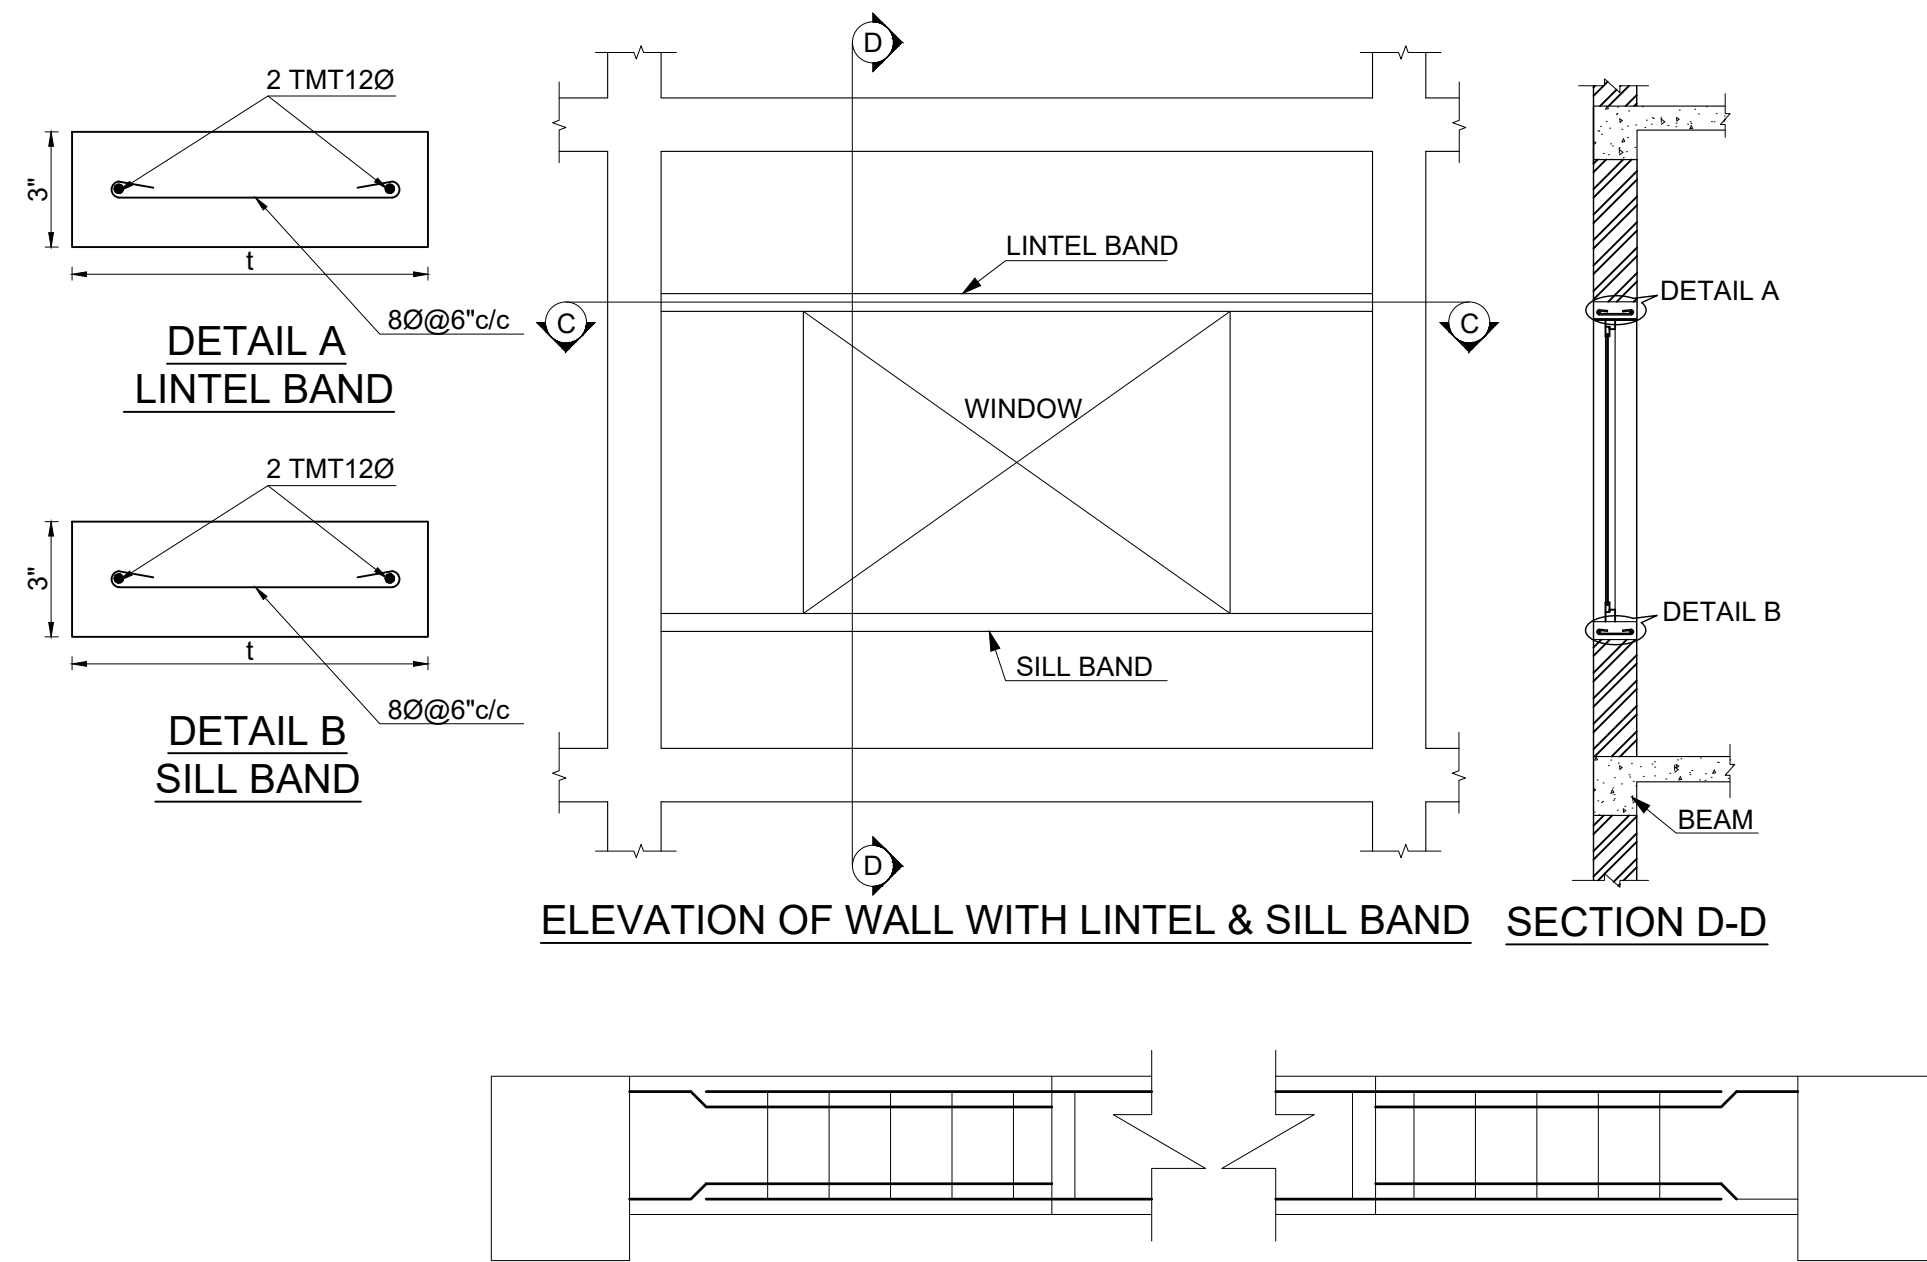

ELEVATION OF WALL WITH LINTEL & SILL BAND

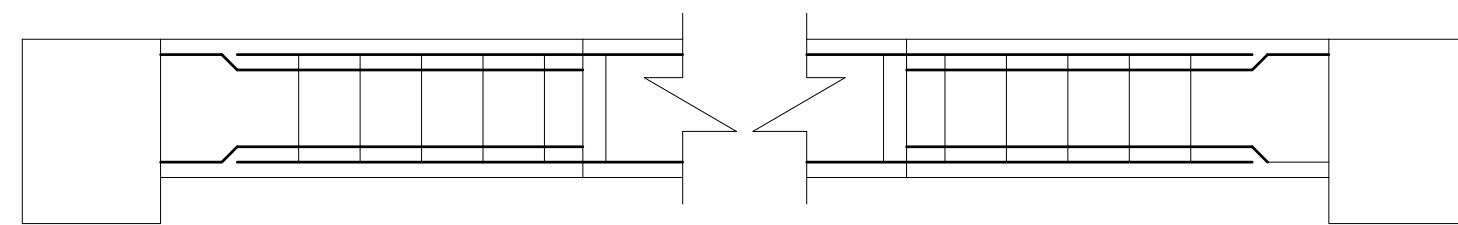


BEAM LAPPING DETAILS

LAPPING FOR BEAM BAR

SCALE=NTS

LAPPING NOTES FOR BEAM
LAP LENGTH SHALL NOT BE LESS THAN BAR DEVELOPMENT LENGTH IN TENSION
NOT MORE THAN 50% OF THE BARS SHALL BE SPLICED AT ONE SECTION.
LAP SPLICE SHALL NOT BE PROVIDED:-


2. WITHIN A DISTANCE OF 2d FROM JOINT FACE
3. WITHIN A QUARTER LENGTH OF THE MEMBER

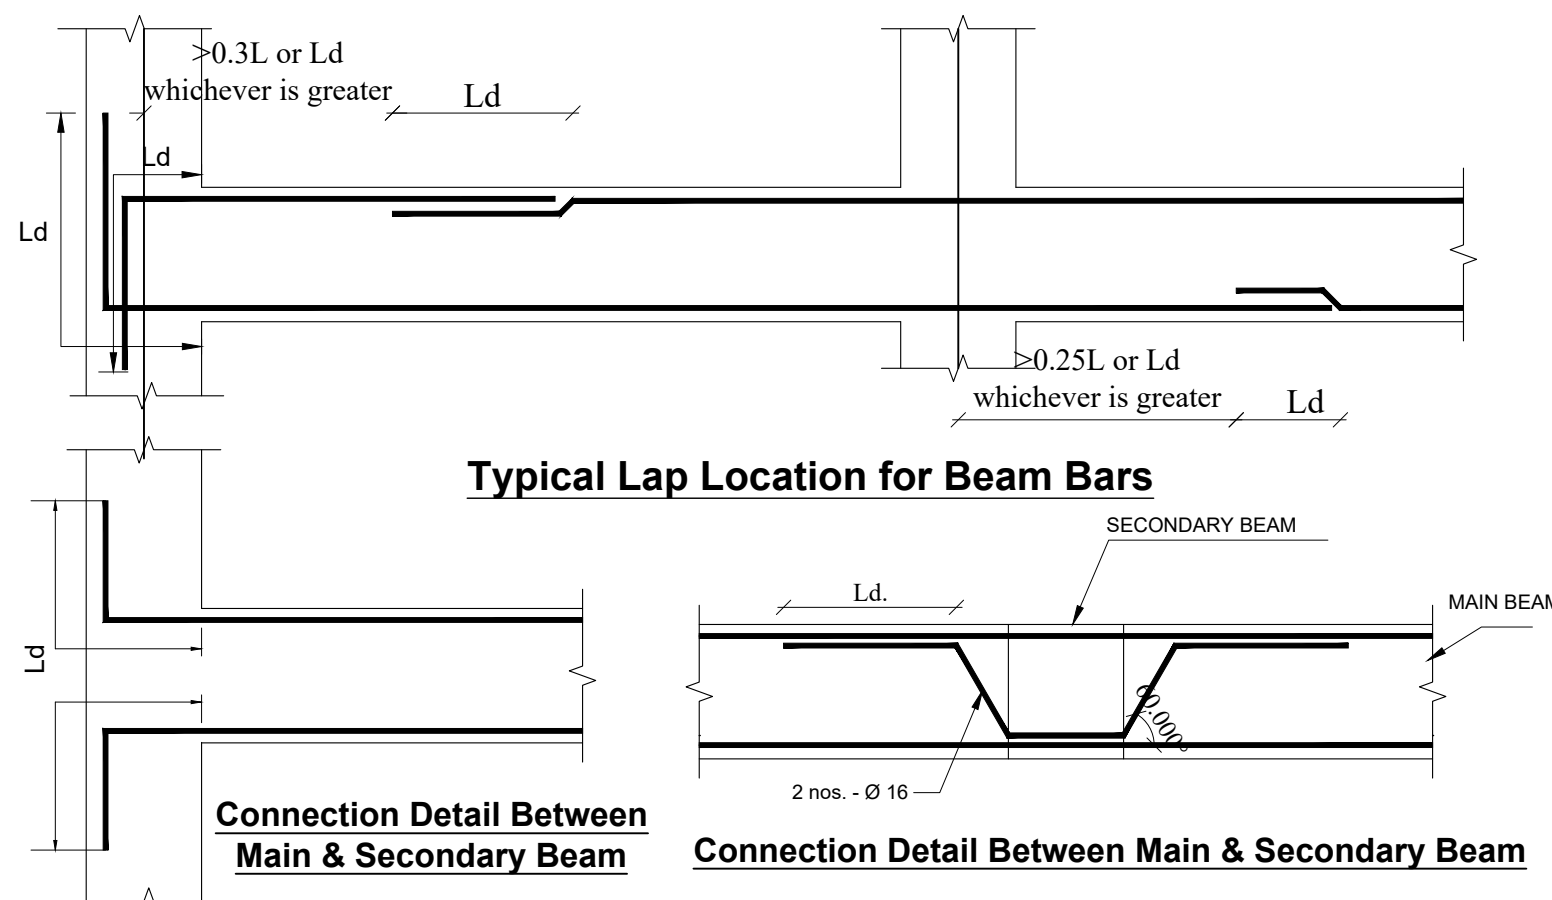


Typical Lap Location for Beam Bars

Connection Detail Between Main & Secondary Beam

Connection Detail Between Main & Secondary Beam

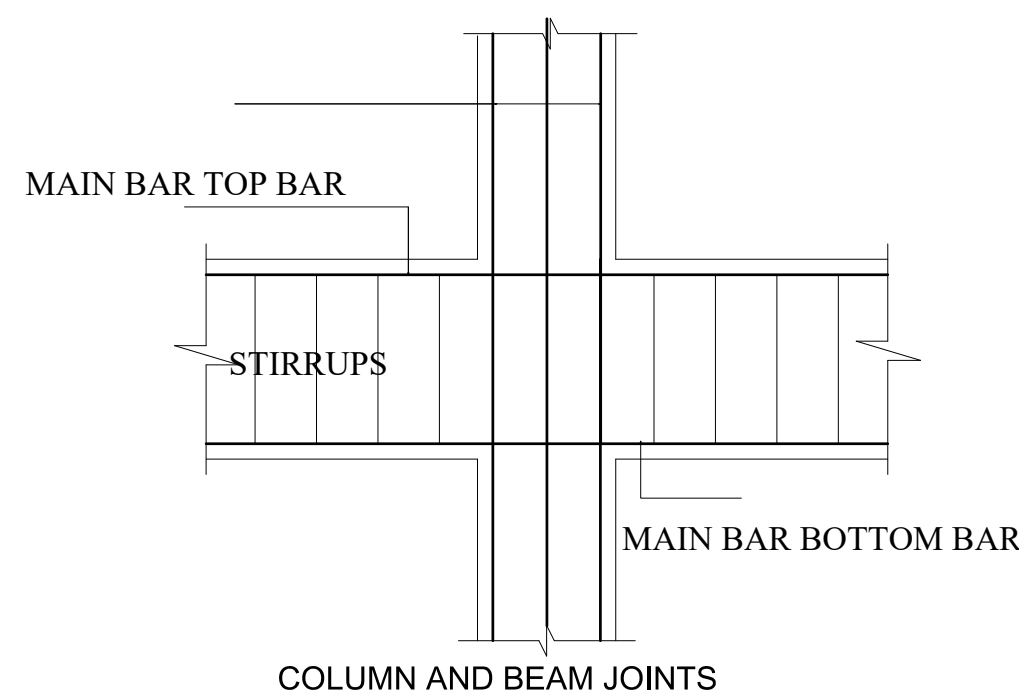

COLUMN AND BEAM JOINTS

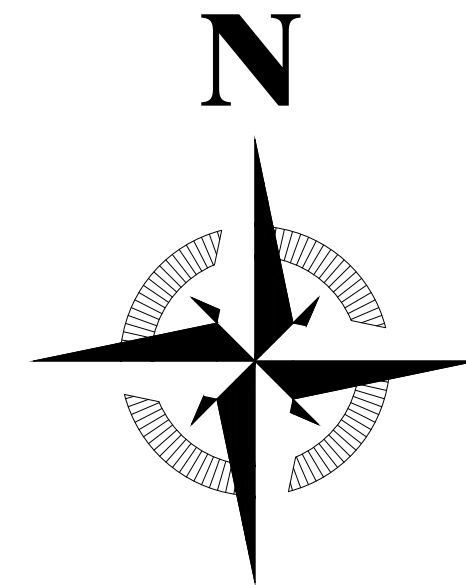

REVISIONS

REV.	DESCRIPTION	DATE
A		



URBAN PARK PVT. LTD.
KATHMANDU, NEPAL
urbanparknepal@gmail.com

OWNER: Mr. DHAN KUMARI KHATRI

SIGNATURE:

BUILDING TYPE: RESIDENTIAL	LOCATION: BUDHANILKANTHA, WARD NO. 3
PLOT NO: 125	AREA: 176.96 SQ.M. (0-5-2-1.05) 174.85 SQ.M. (0-5-2-0) ACCORDING TO LALPURA

DETAILS:
STRUCTURAL DRAWINGS

ARCHITECT: AR. APIL K. C.

DATE: SEP 2021
SCALE: 1"=8'-0" (1:96)
SIGNATURE :

NEC REGISTRATION NO.
1070 "A"
REMARKS: